
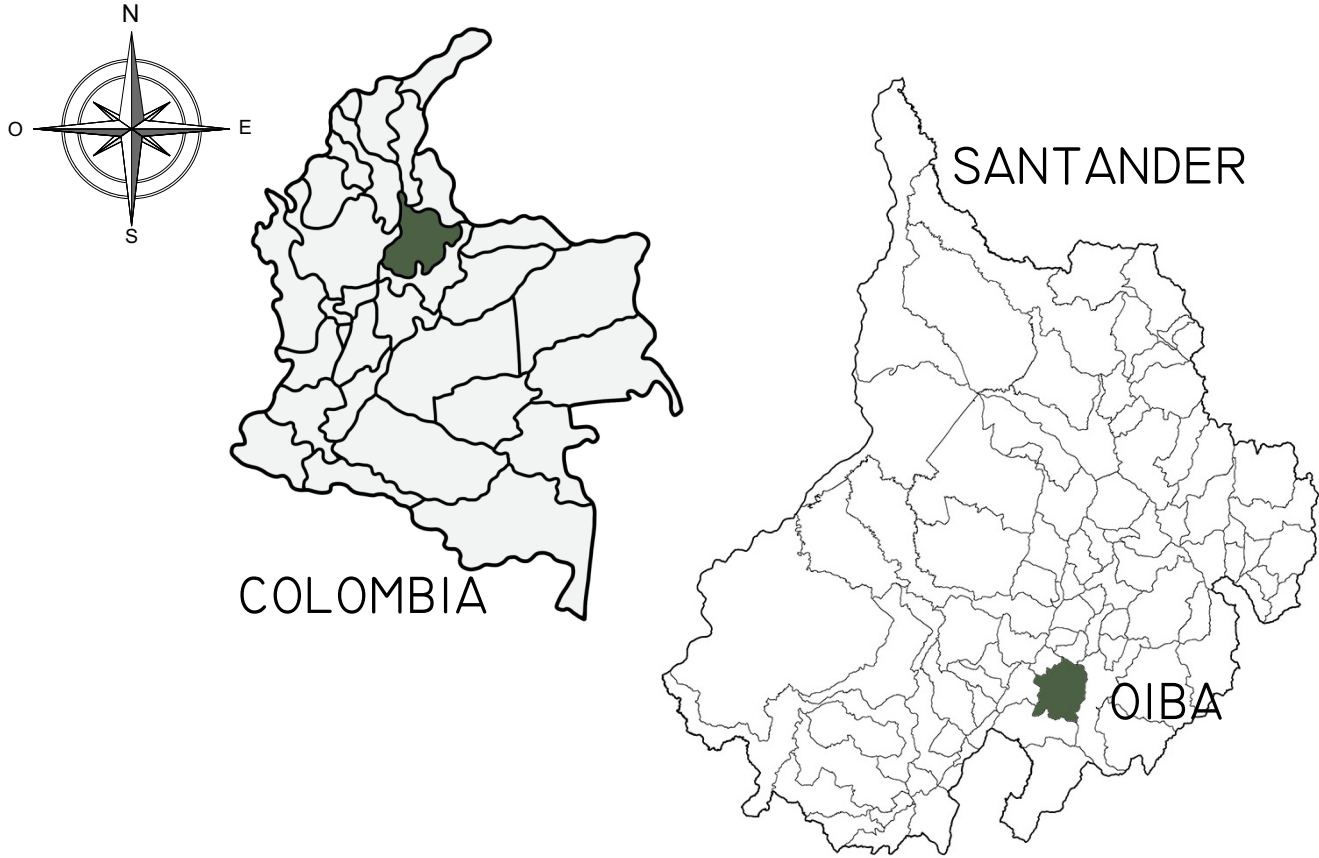
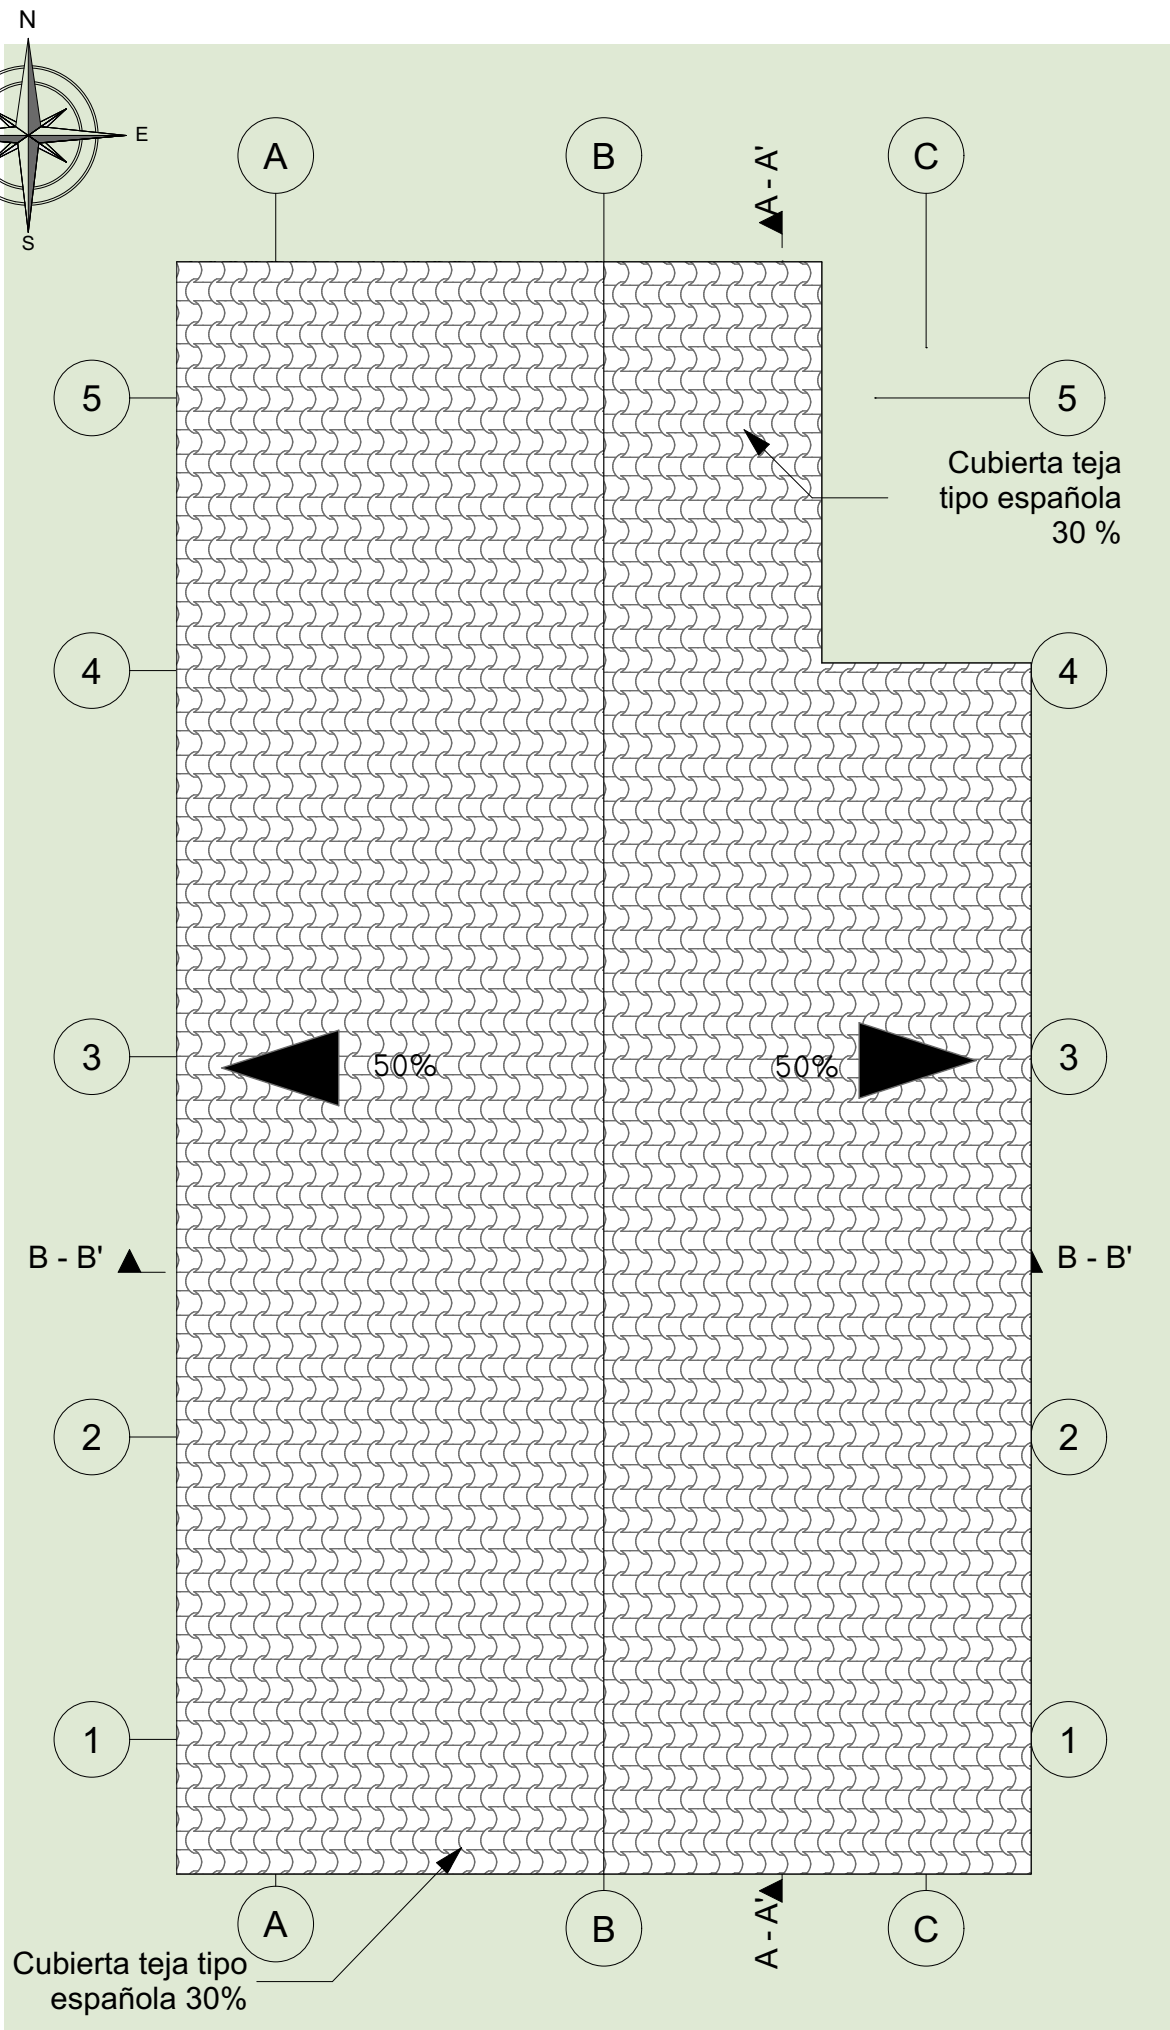


PLANTA PRIMER PISO



PLANTA DE CUBIERTA

LOCALIZACIÓN

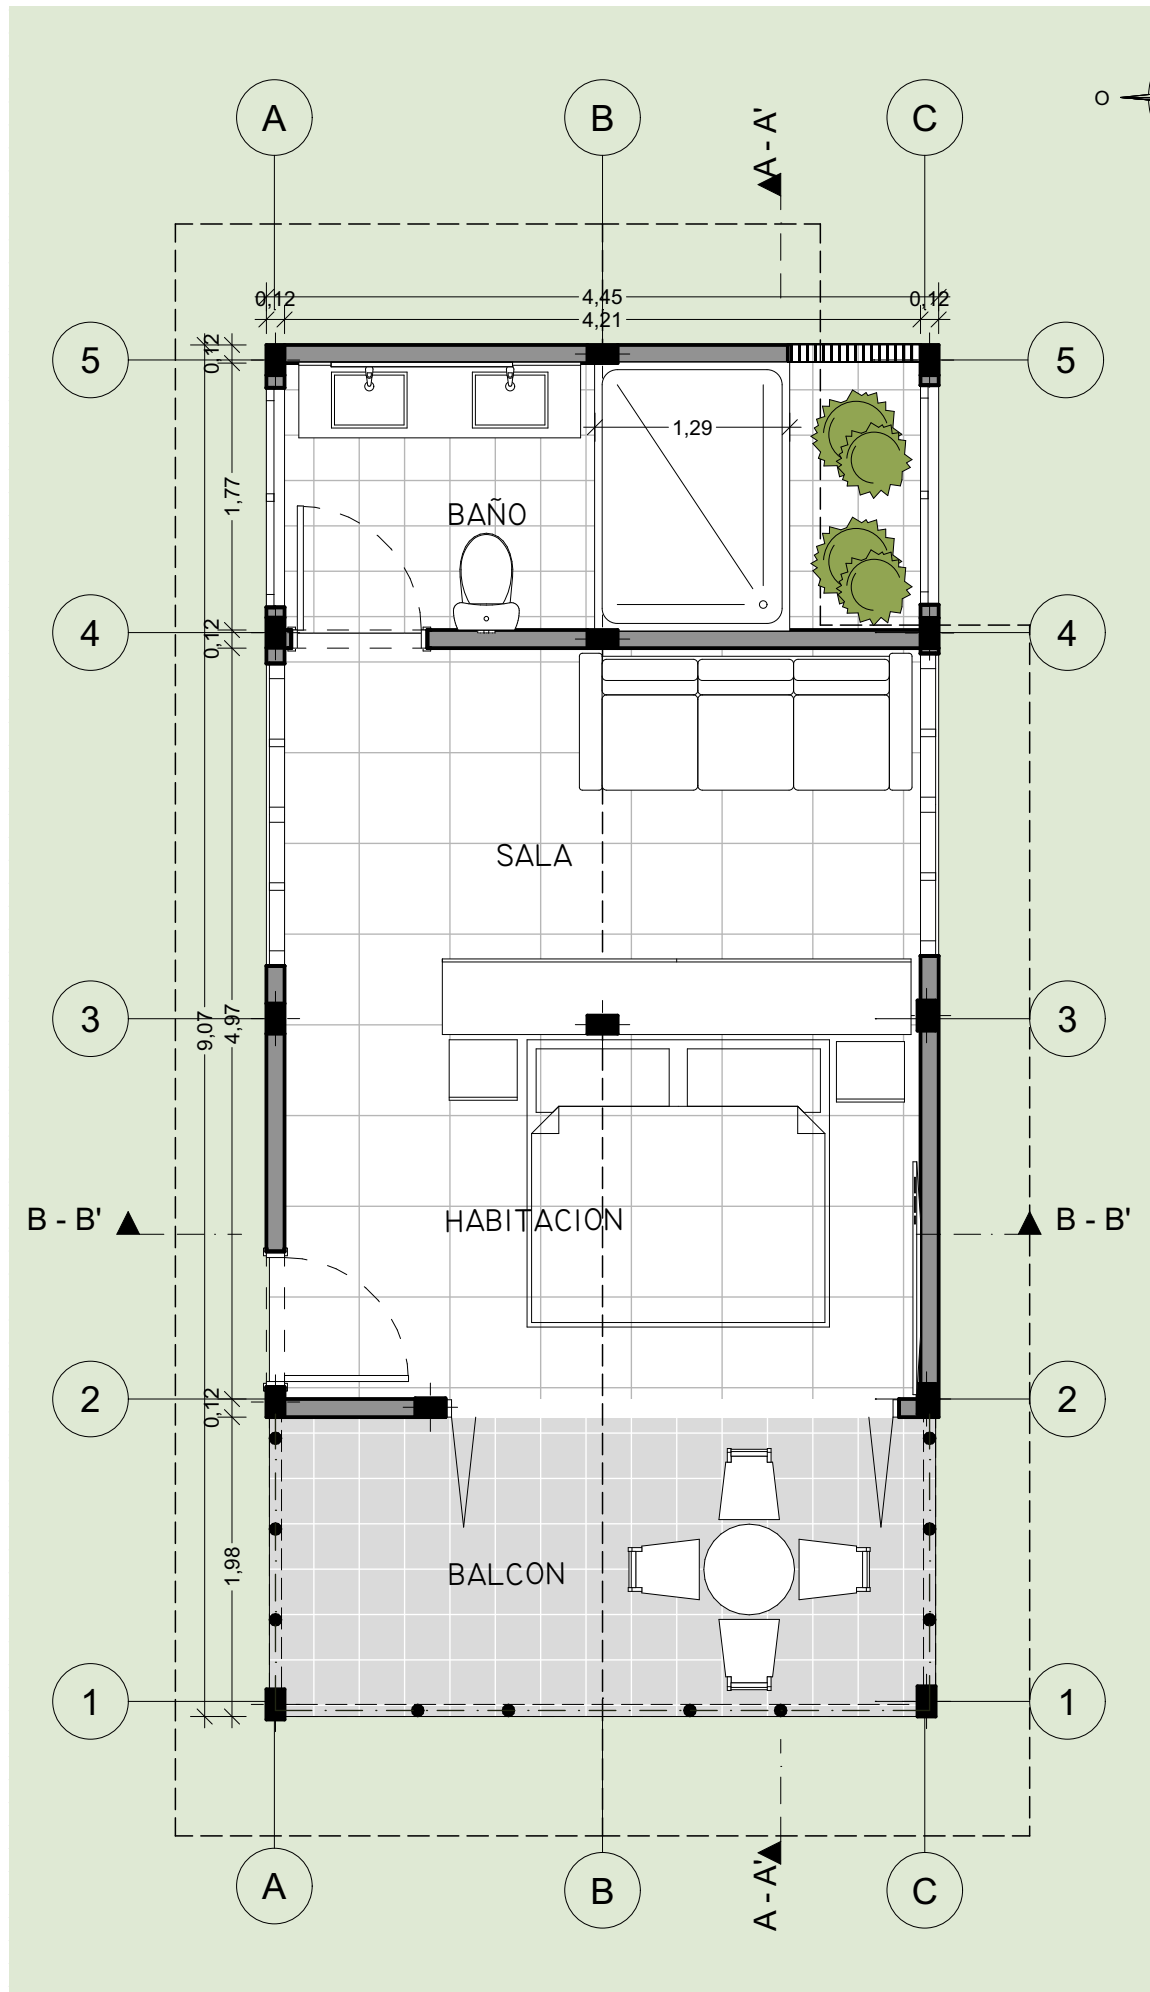


CUADRO DE AREAS	
ÁREA TOTAL DEL PREDIO	1 HA
ÁREA CONSTRUIDA POR MODULO	39.17 M2
ÁREA TOTAL CONSTRUIDA	122 M2

FACHADA LATERAL IZQUIERDA

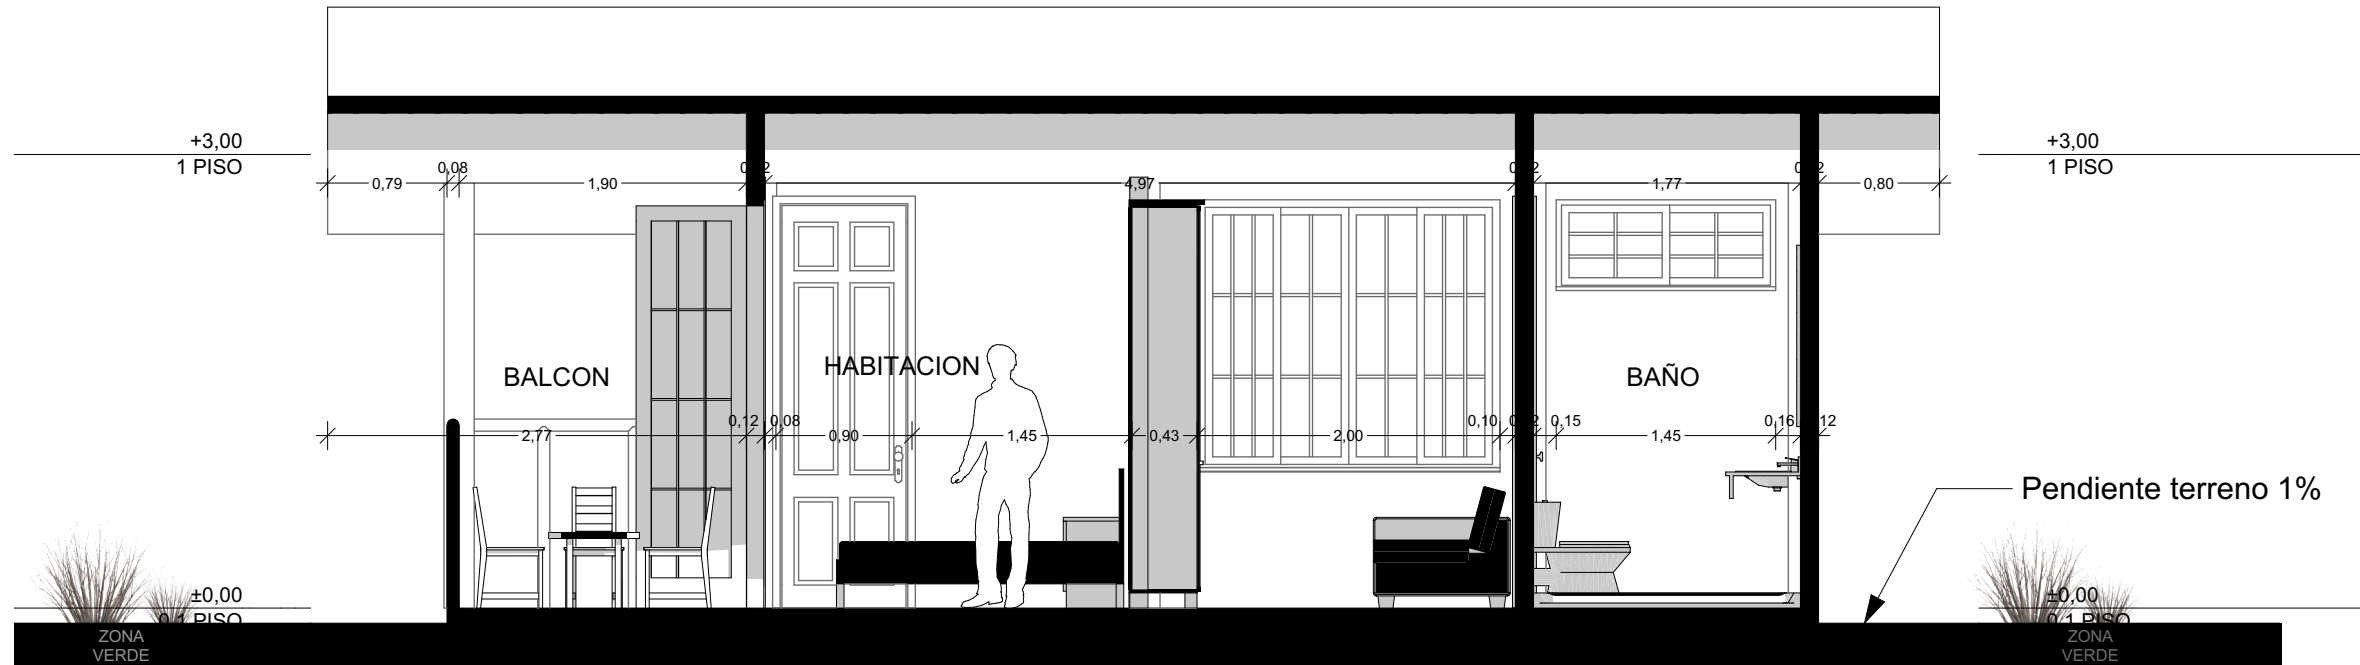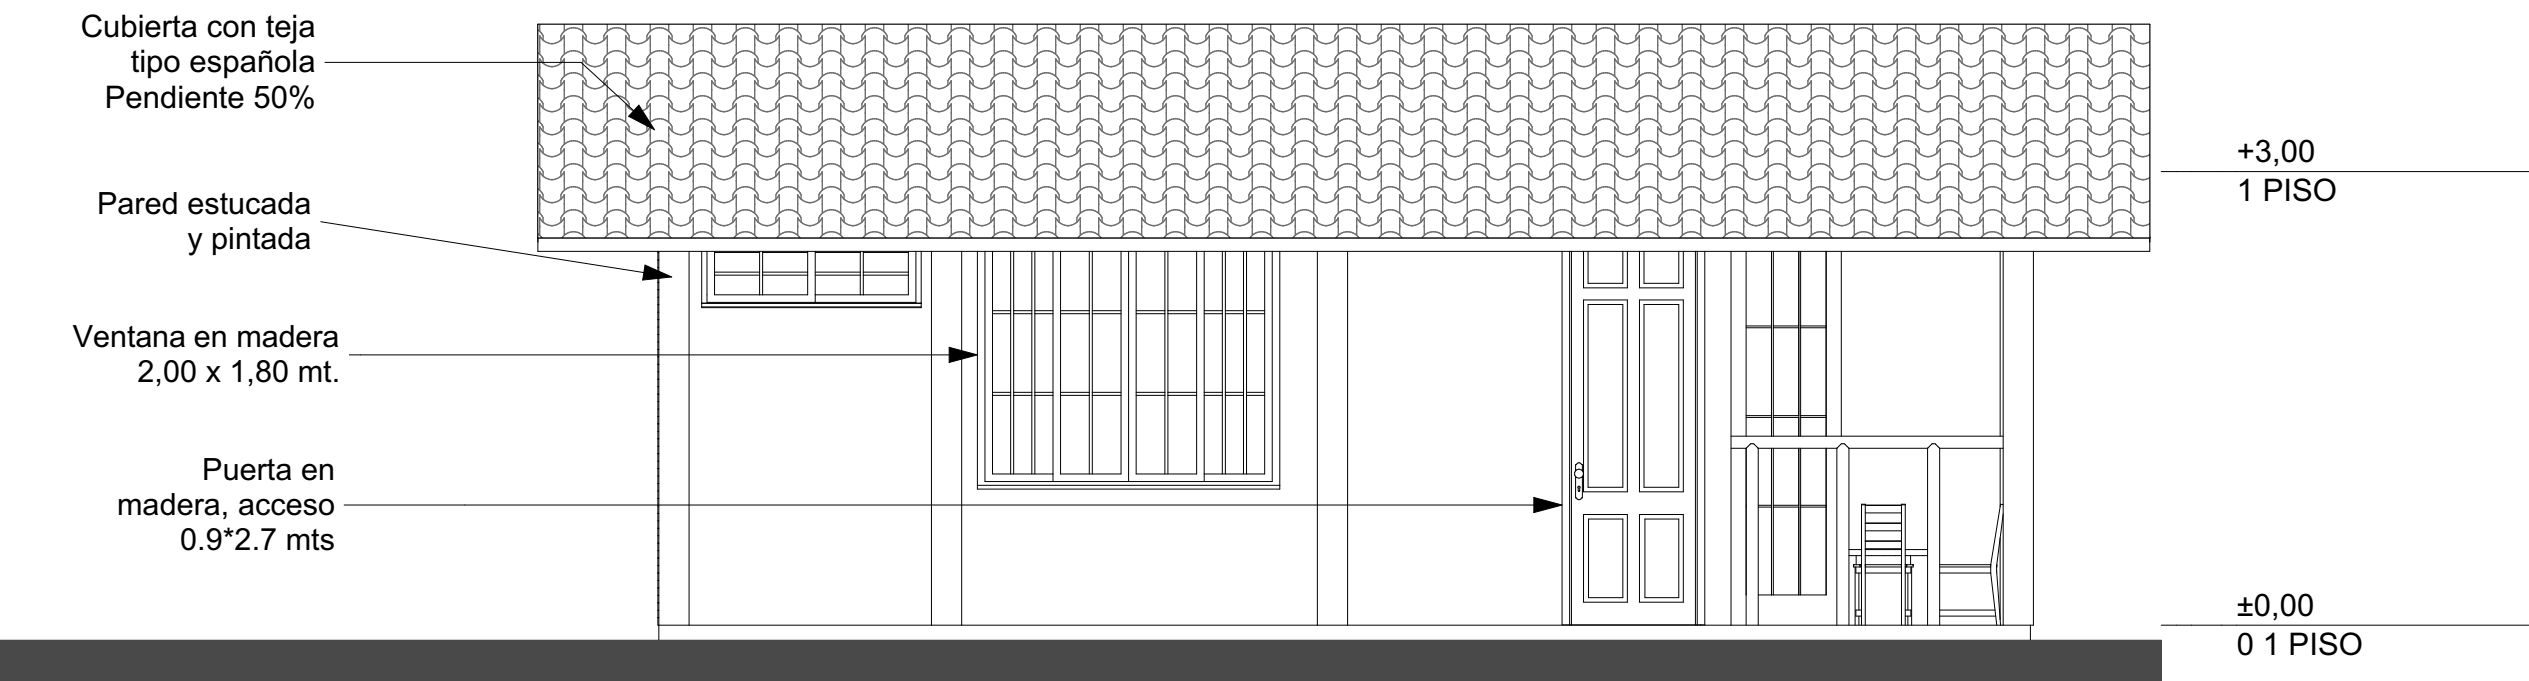

CORTE A-A'

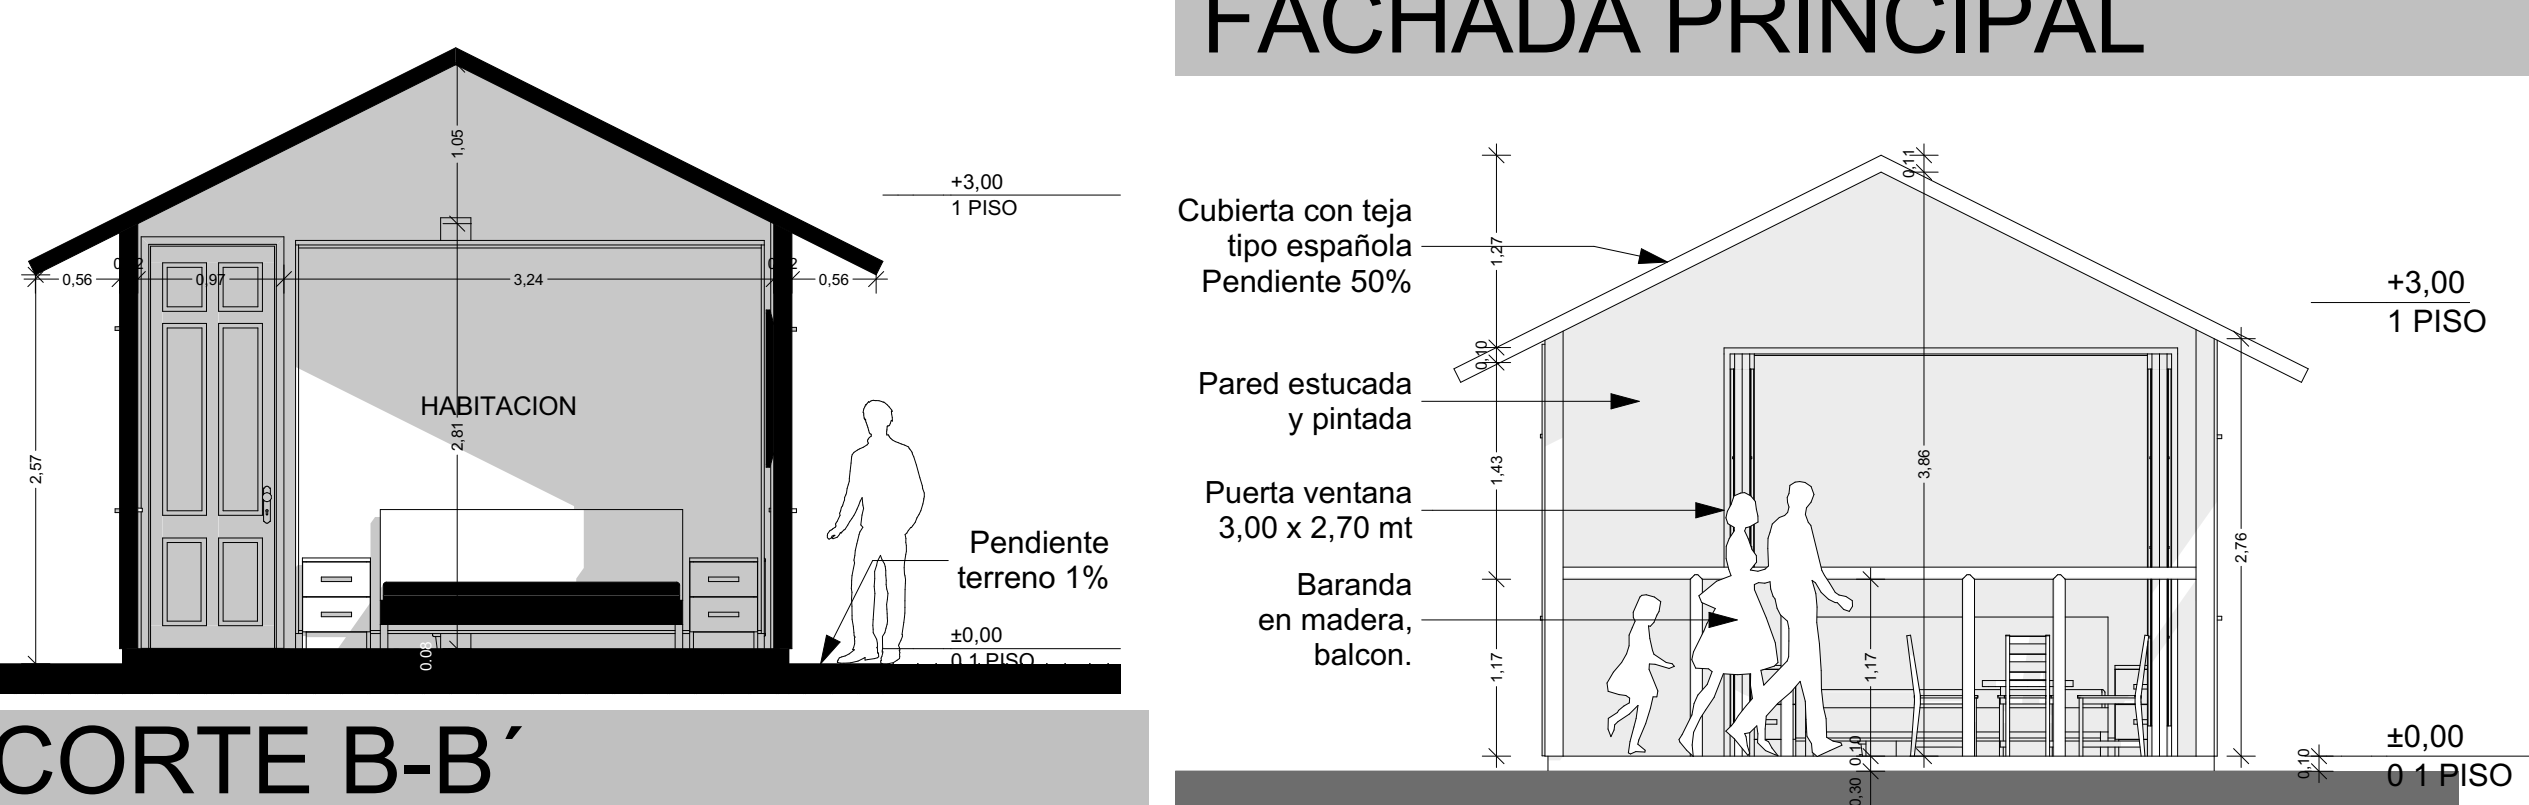

CORTE B-B'

PROPIETARIOS: FERNANDO LAGOS RODRIGUEZ MARIA ELSA RODRIGUEZ JIMENEZ	DIRECCIÓN: PREDIO MI HEREDAD, VEREDA EL VOLADOR OIBA, SANTANDER	APROBÓ: 	CONTIENE: PLANTAS ARQUITECTONICAS, CORTES, FACHADA, CUADRO DE AREAS Y LOCALIZACION	FECHA NOVIEMBRE DE 2024	TRAMITA: ESPECI COL CONSTRUCCIONES
	ARQ. JESSICA VIVIANA RANGEL ESPINOSA M. A30632018-I09873588		LICENCIA DE CONTRUCCIÓN NUEVA	ESCALA 1:50	PLANO I DE I