

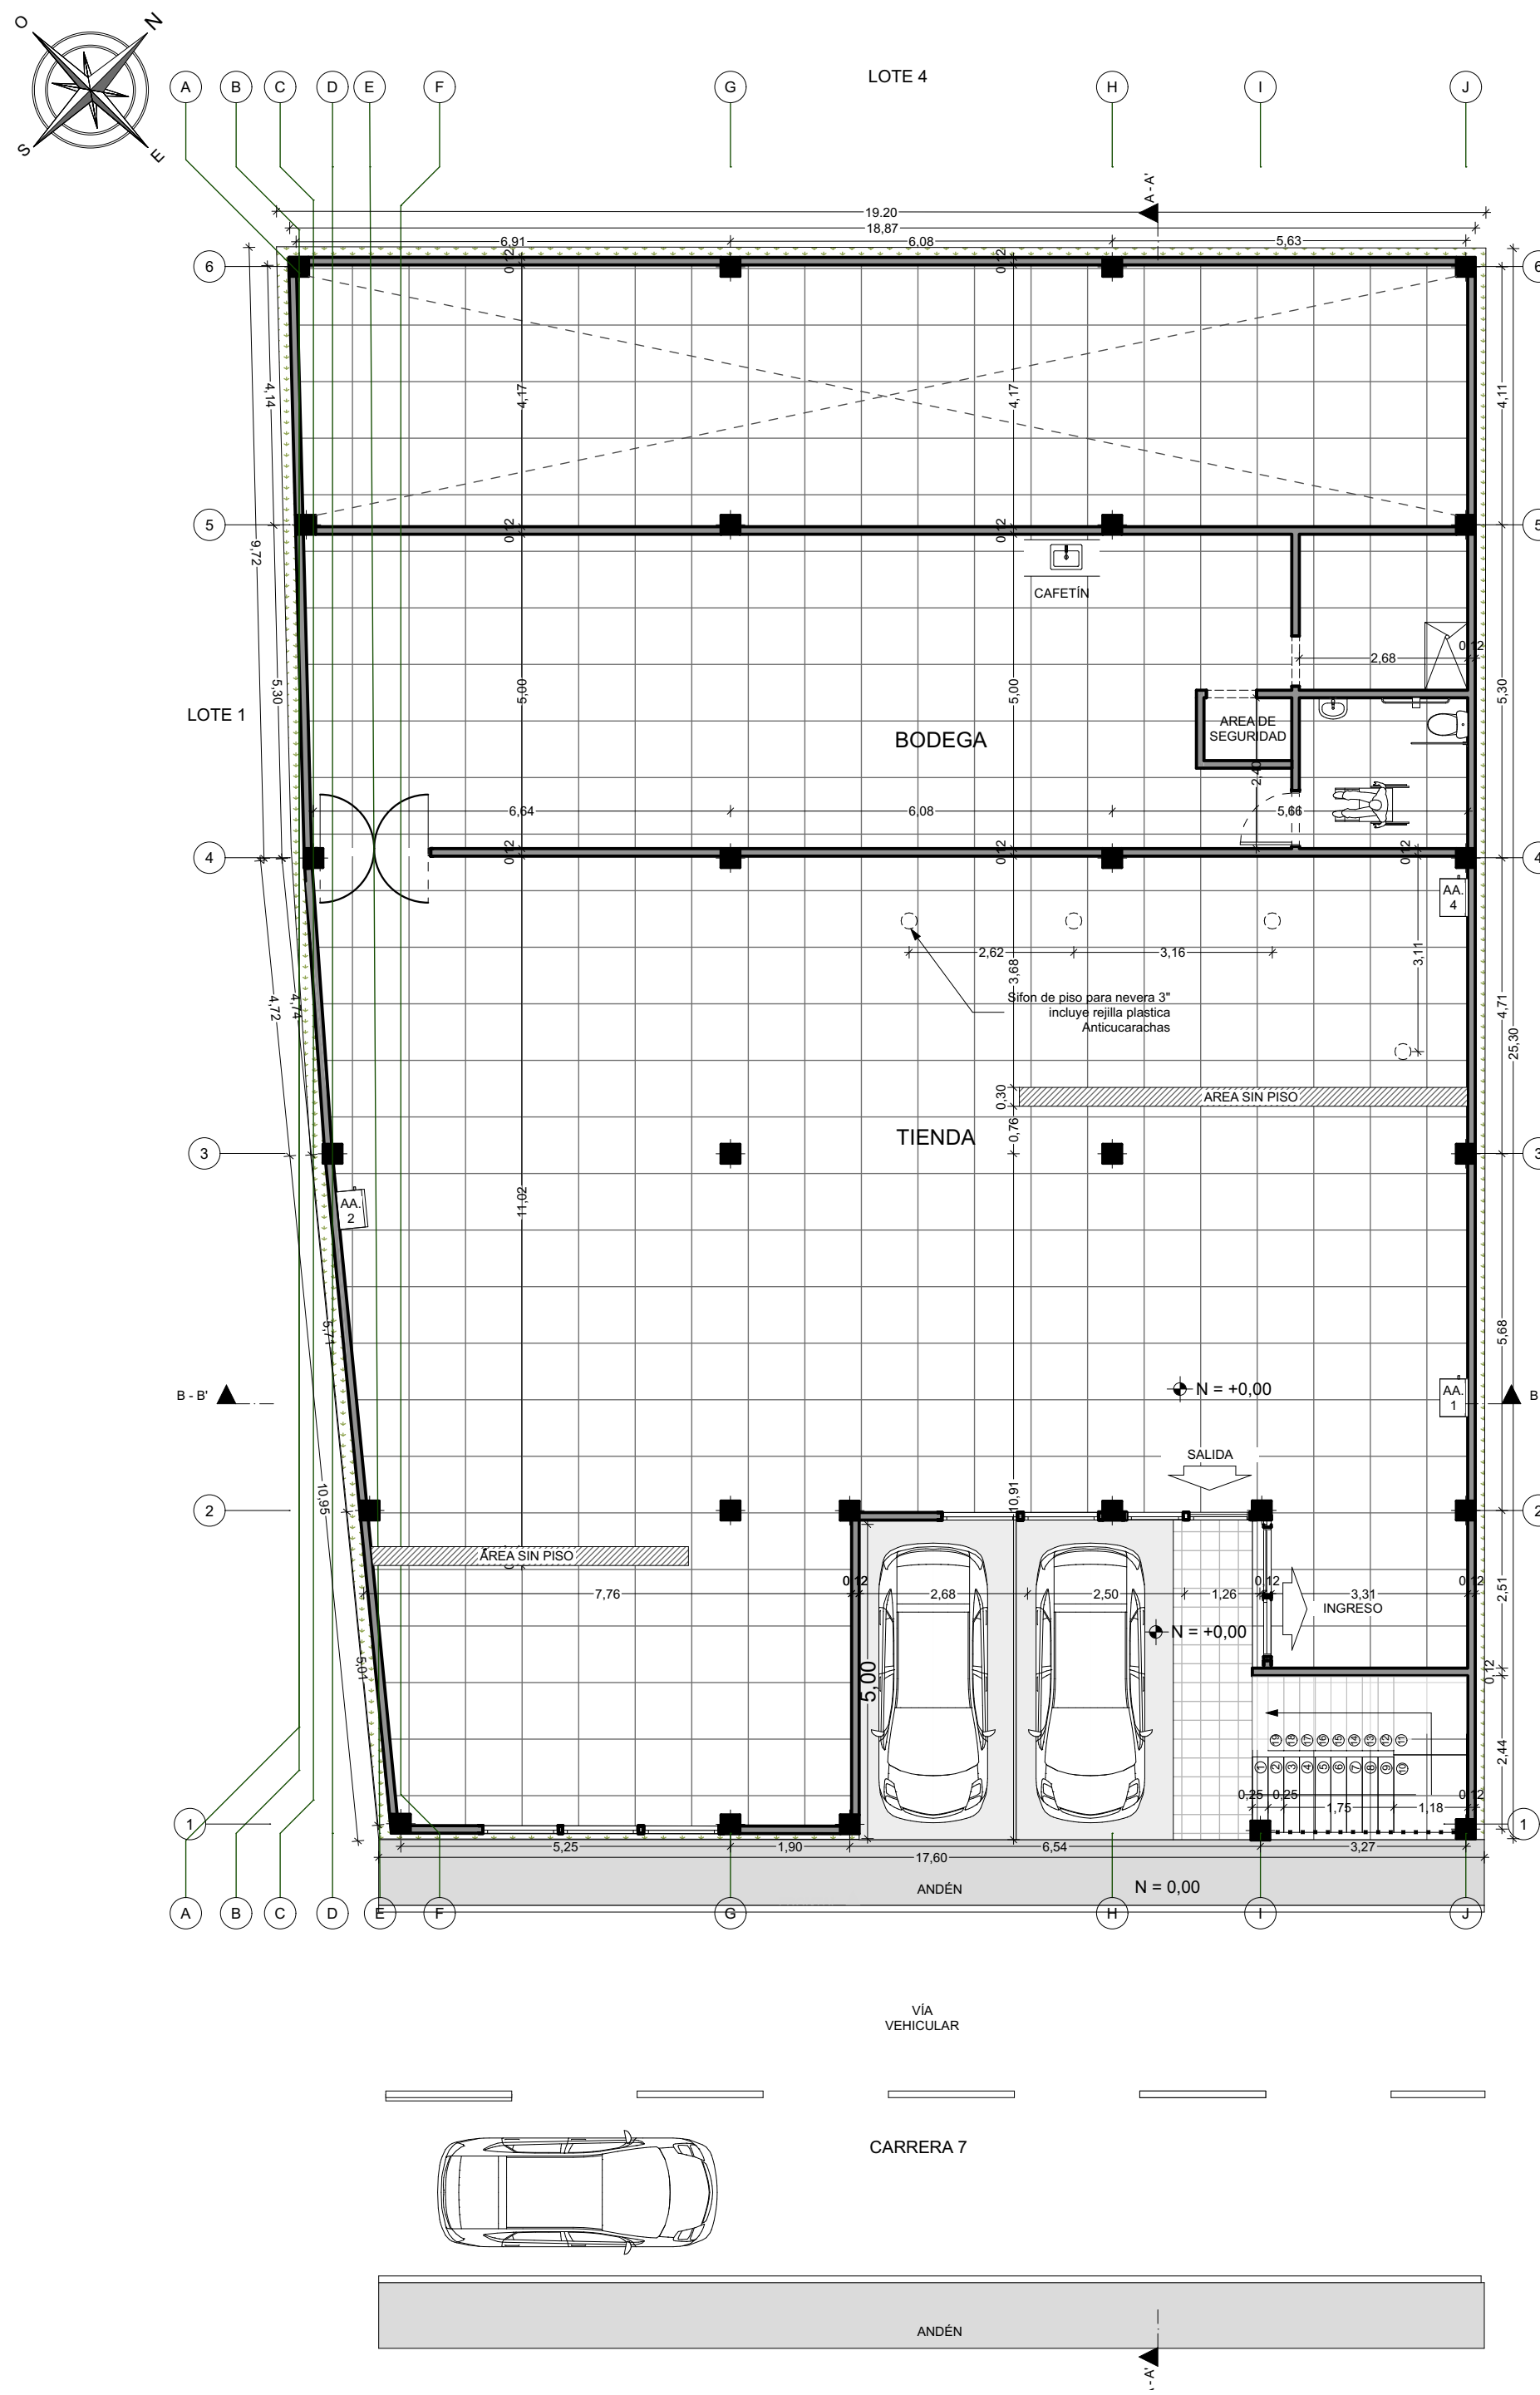


PLANTA PRIMER PISO

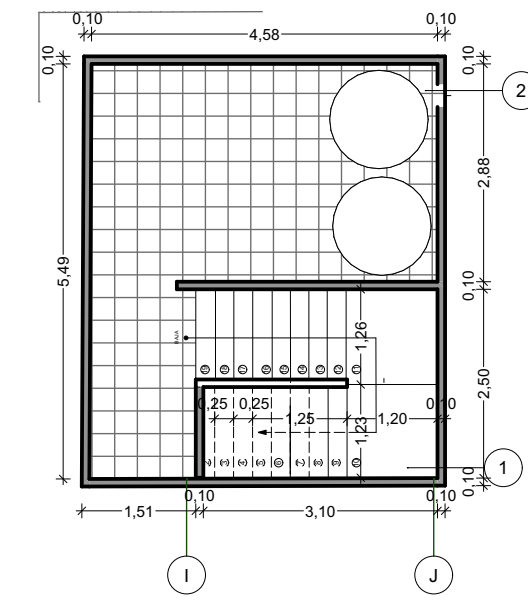


PLANTA DE CUBIERTA

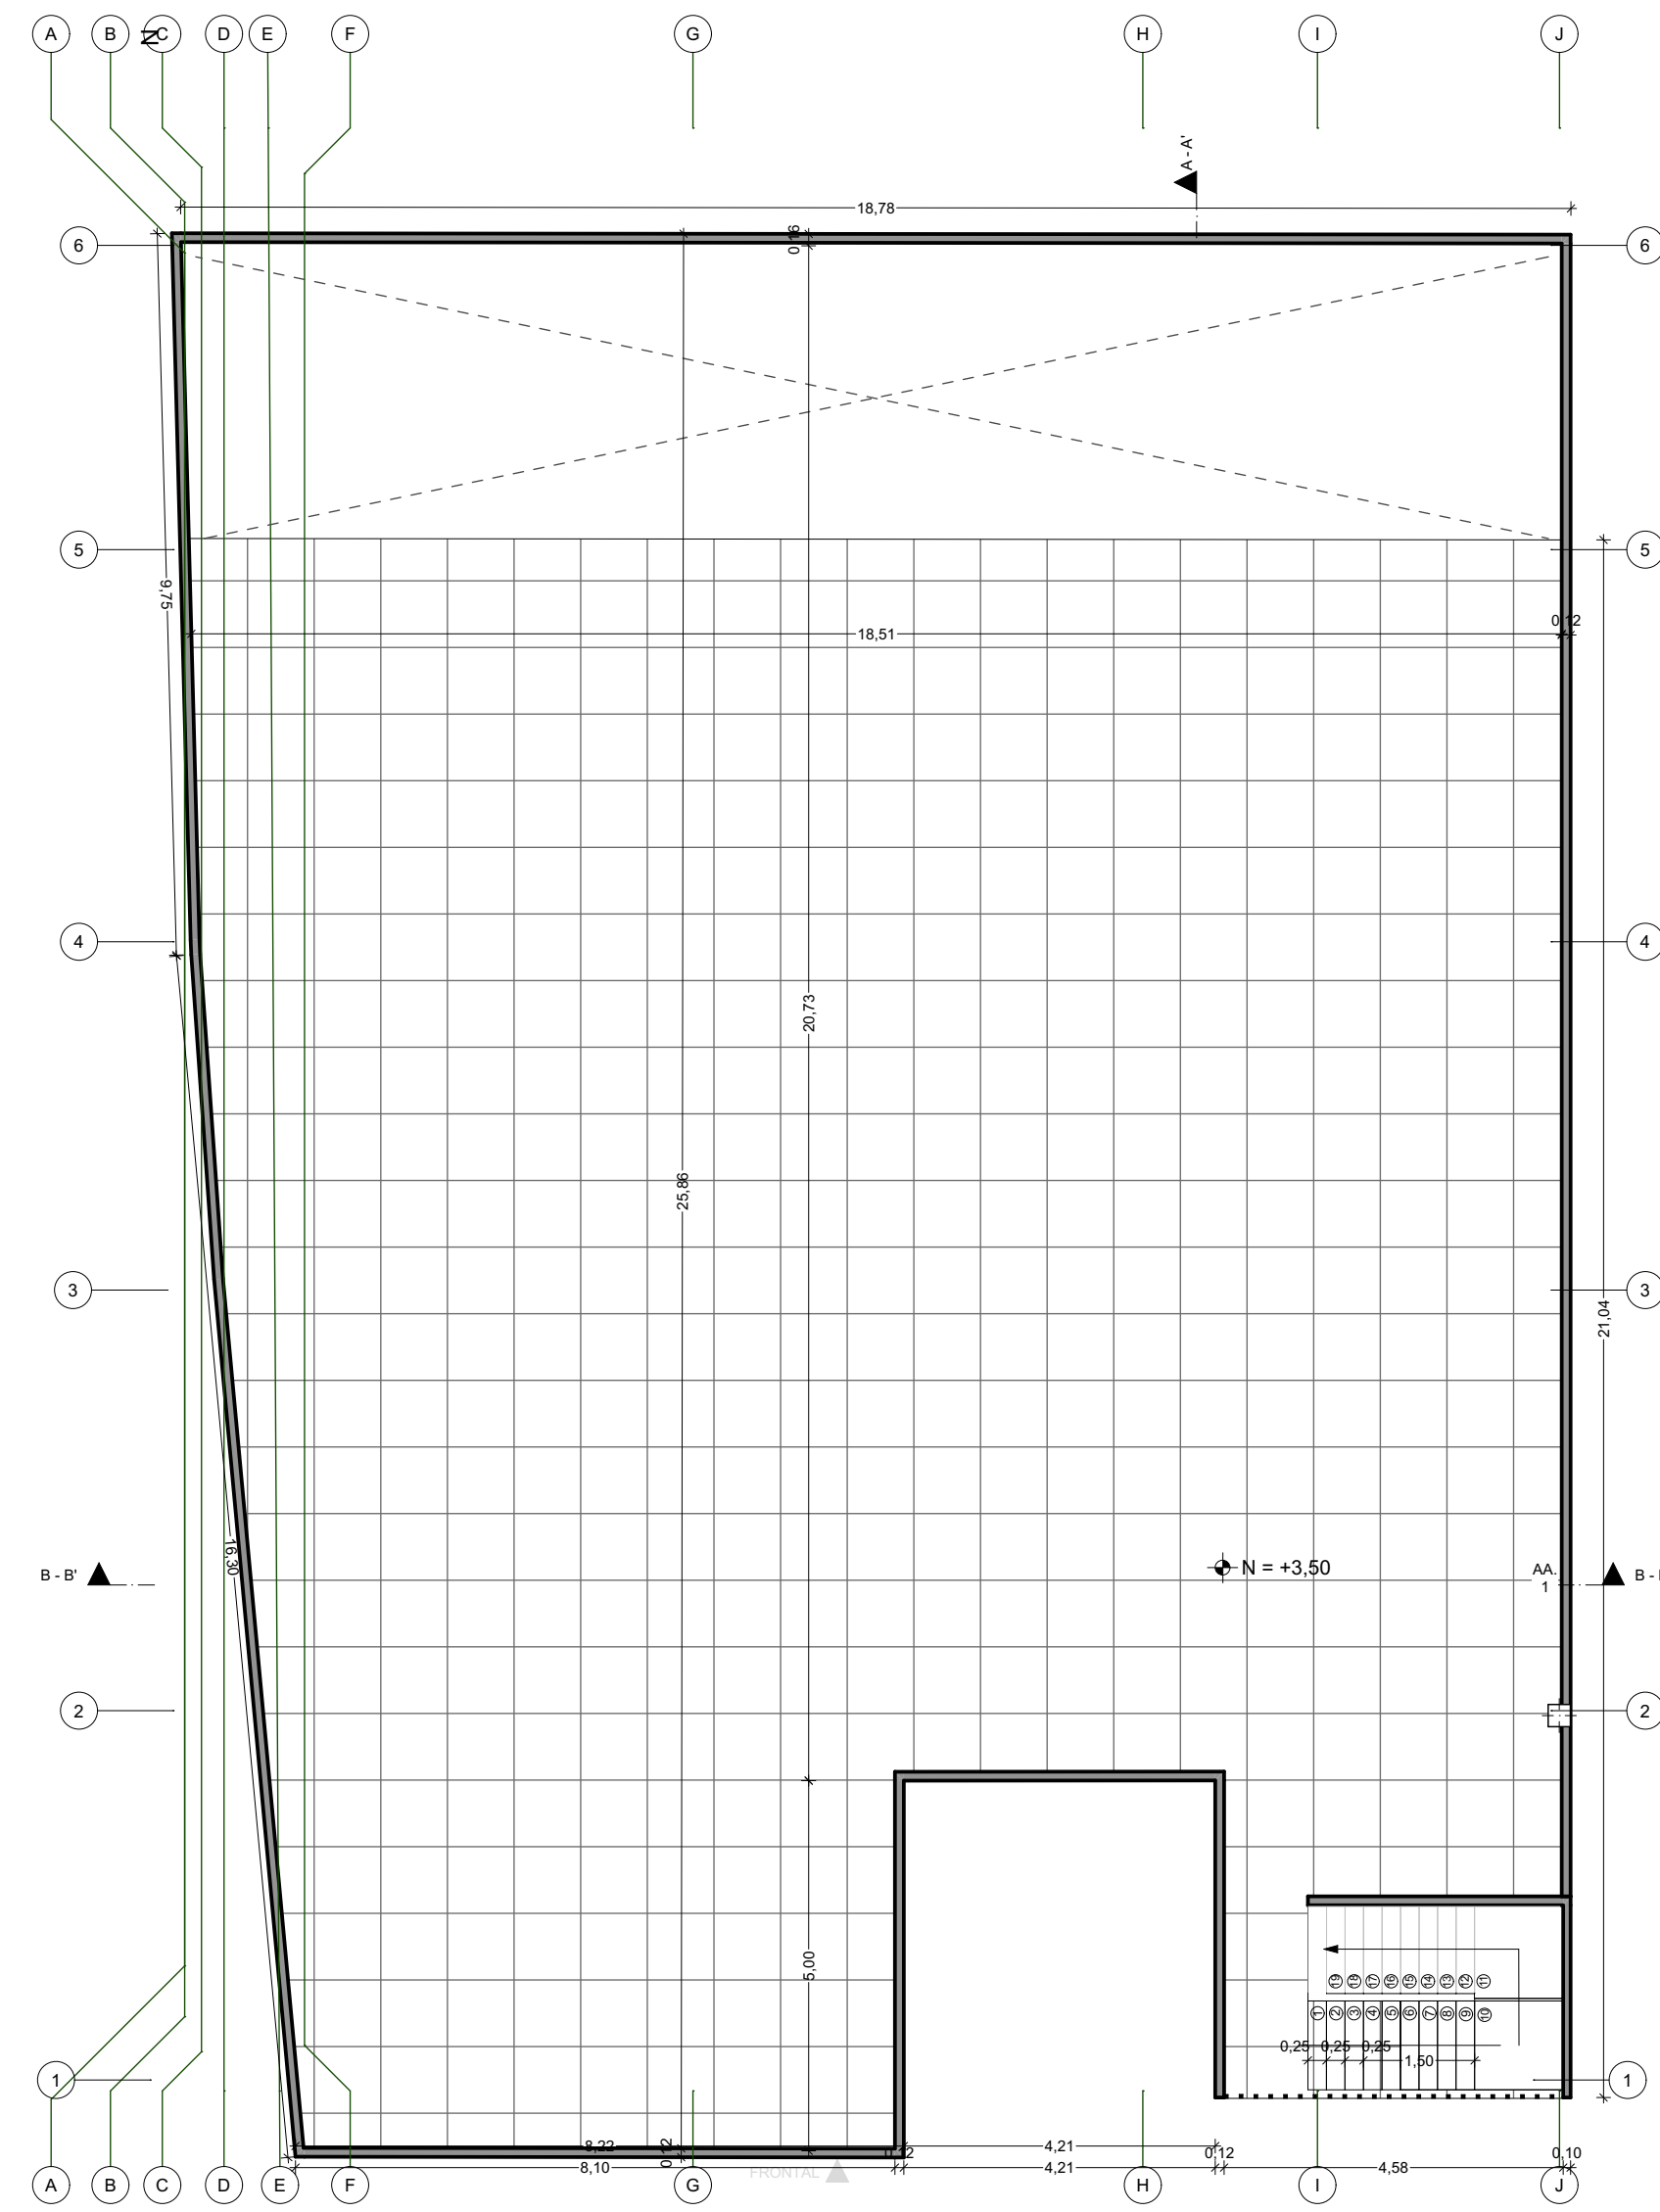

CUADRO DE AREAS

ÁREA TOTAL DEL LOTE	471 M2
ÁREA CONSTRUIDA 1 PISO	347.49 M2
ÁREA CONSTRUIDA ESCALERAS	27.12 M2
ÁREA TOTAL CONSTRUIDA	374.61 M2


LOCALIZACIÓN

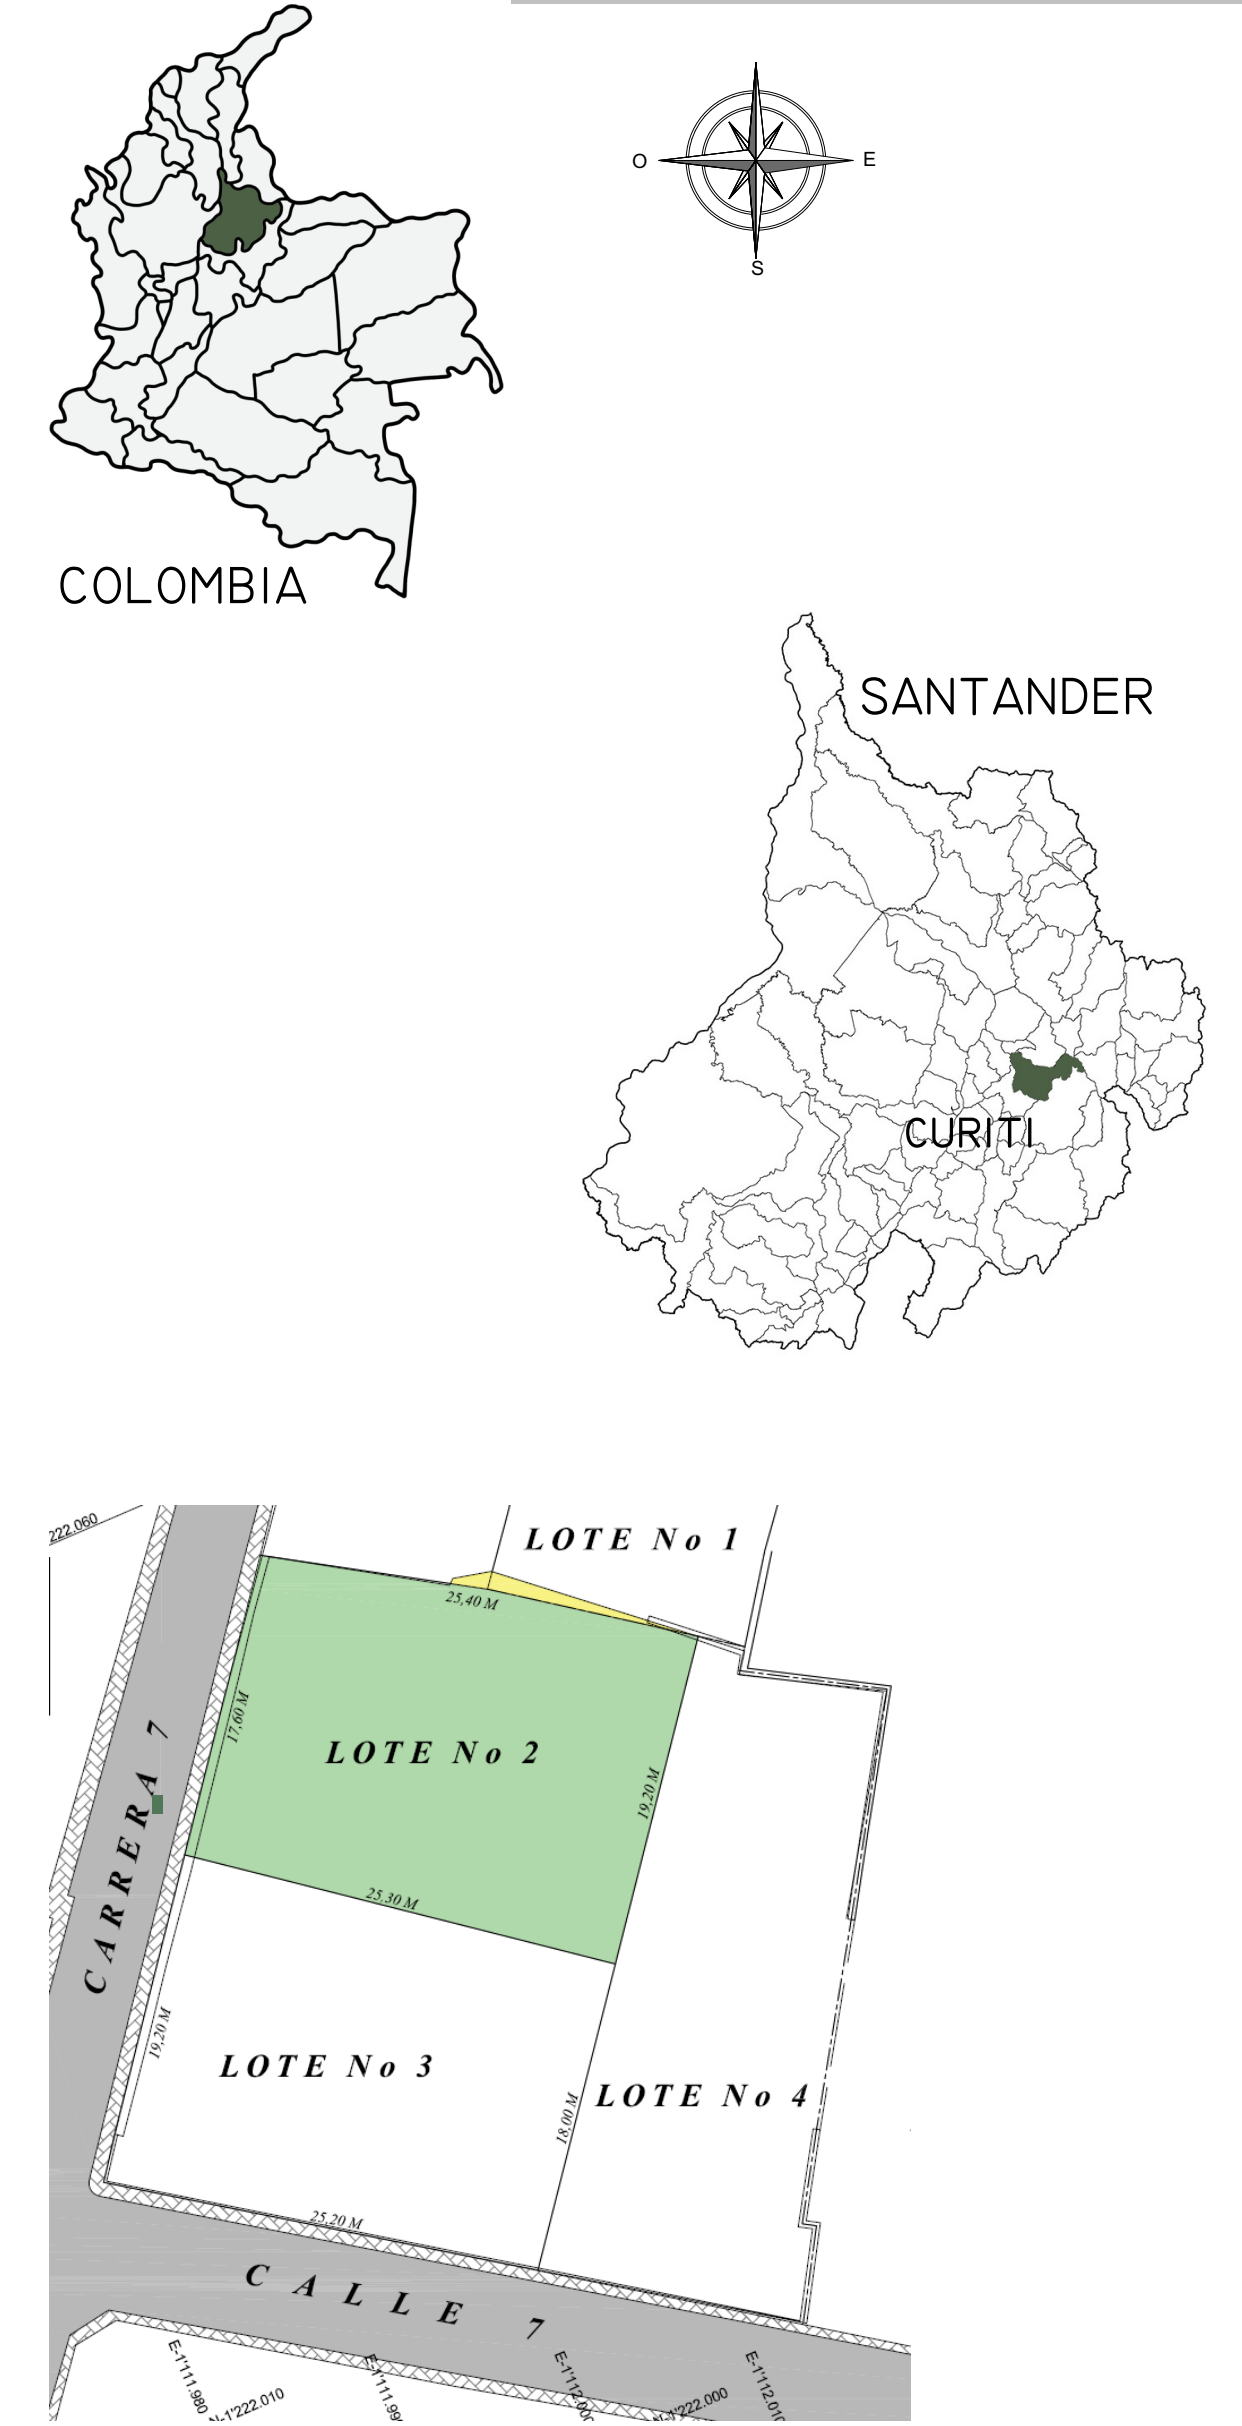


FACHADA FRONTAL



CORTE A - A'

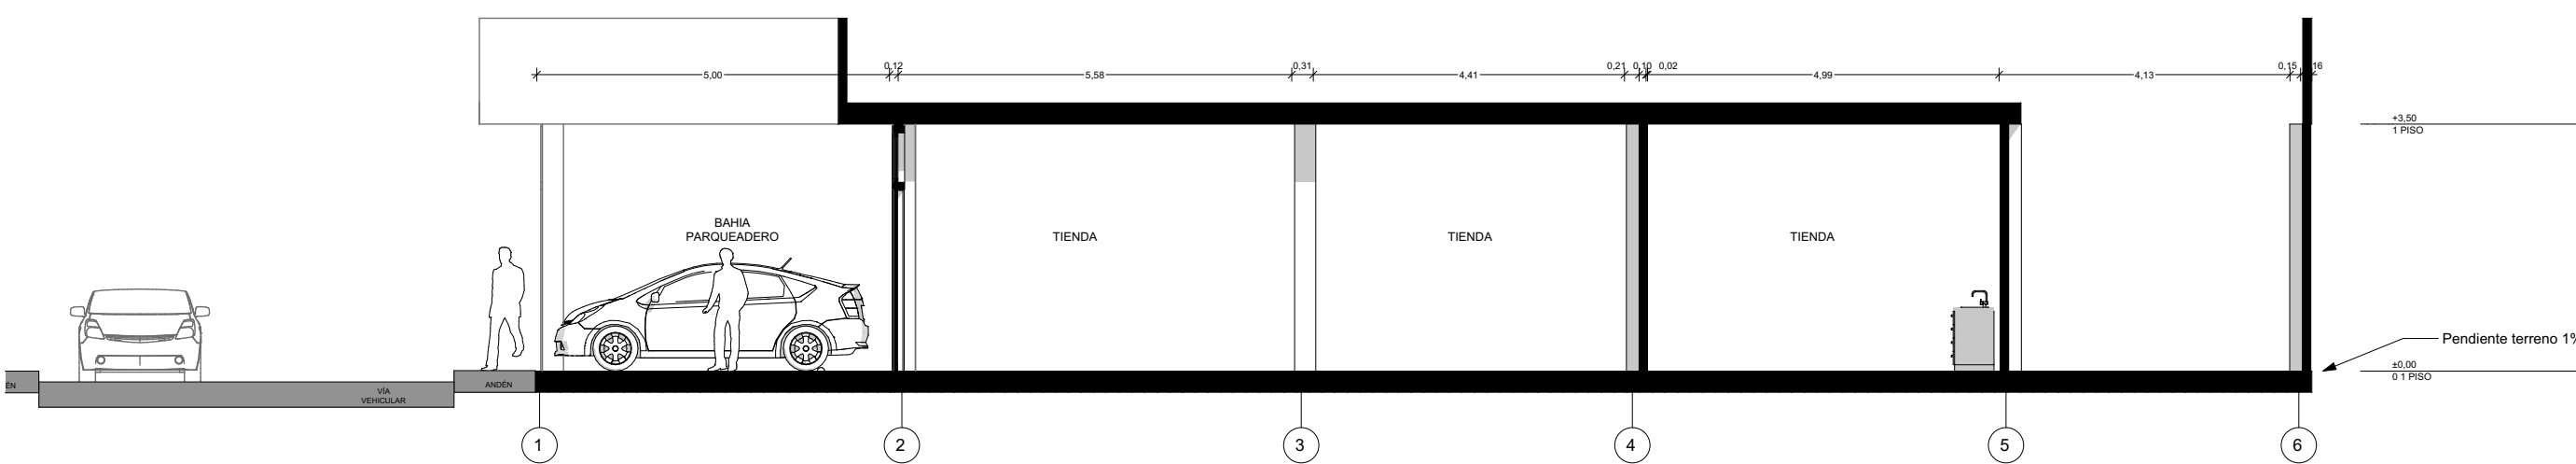

CORTE B - B'

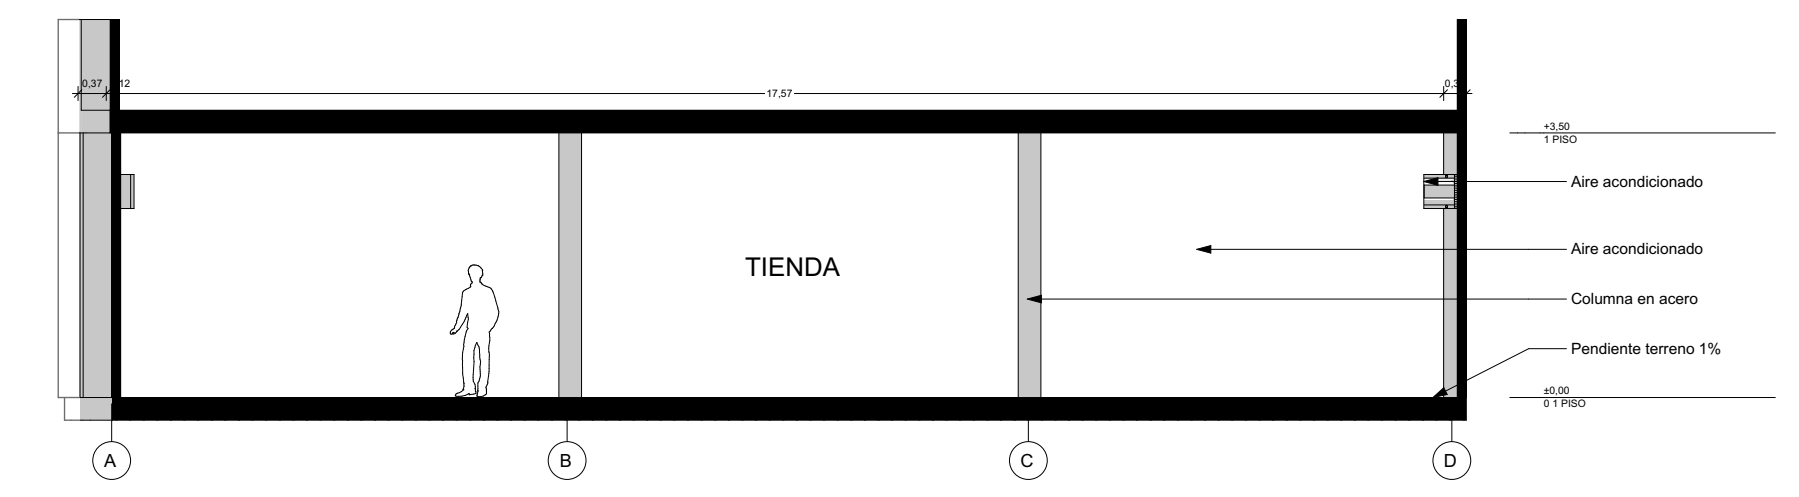

PROPIETARIOS: FABIO ARDILA RINCON	DISEÑO: ARQ. JESSICA VIVIANA RANGEL ESPINOSA M. A30632018-I09873588	APROBÓ:	CONTIENE: PLANTAS ARQUITECTÓNICAS, CORTES, FACHADA, CUADRO DE ÁREAS Y LOCALIZACIÓN	FECHA: DICIEMBRE DE 2024	OBSERVACIONES:
DIRECCIÓN: CARRERA 7 N° 7 - LOTE 2 CURITI, SANTANDER			TRAMITE: LICENCIA DE CONSTRUCCIÓN NUEVA	ESCALA: 1:100	PLANO: I DE I