




PLANTA PRIMER PISO

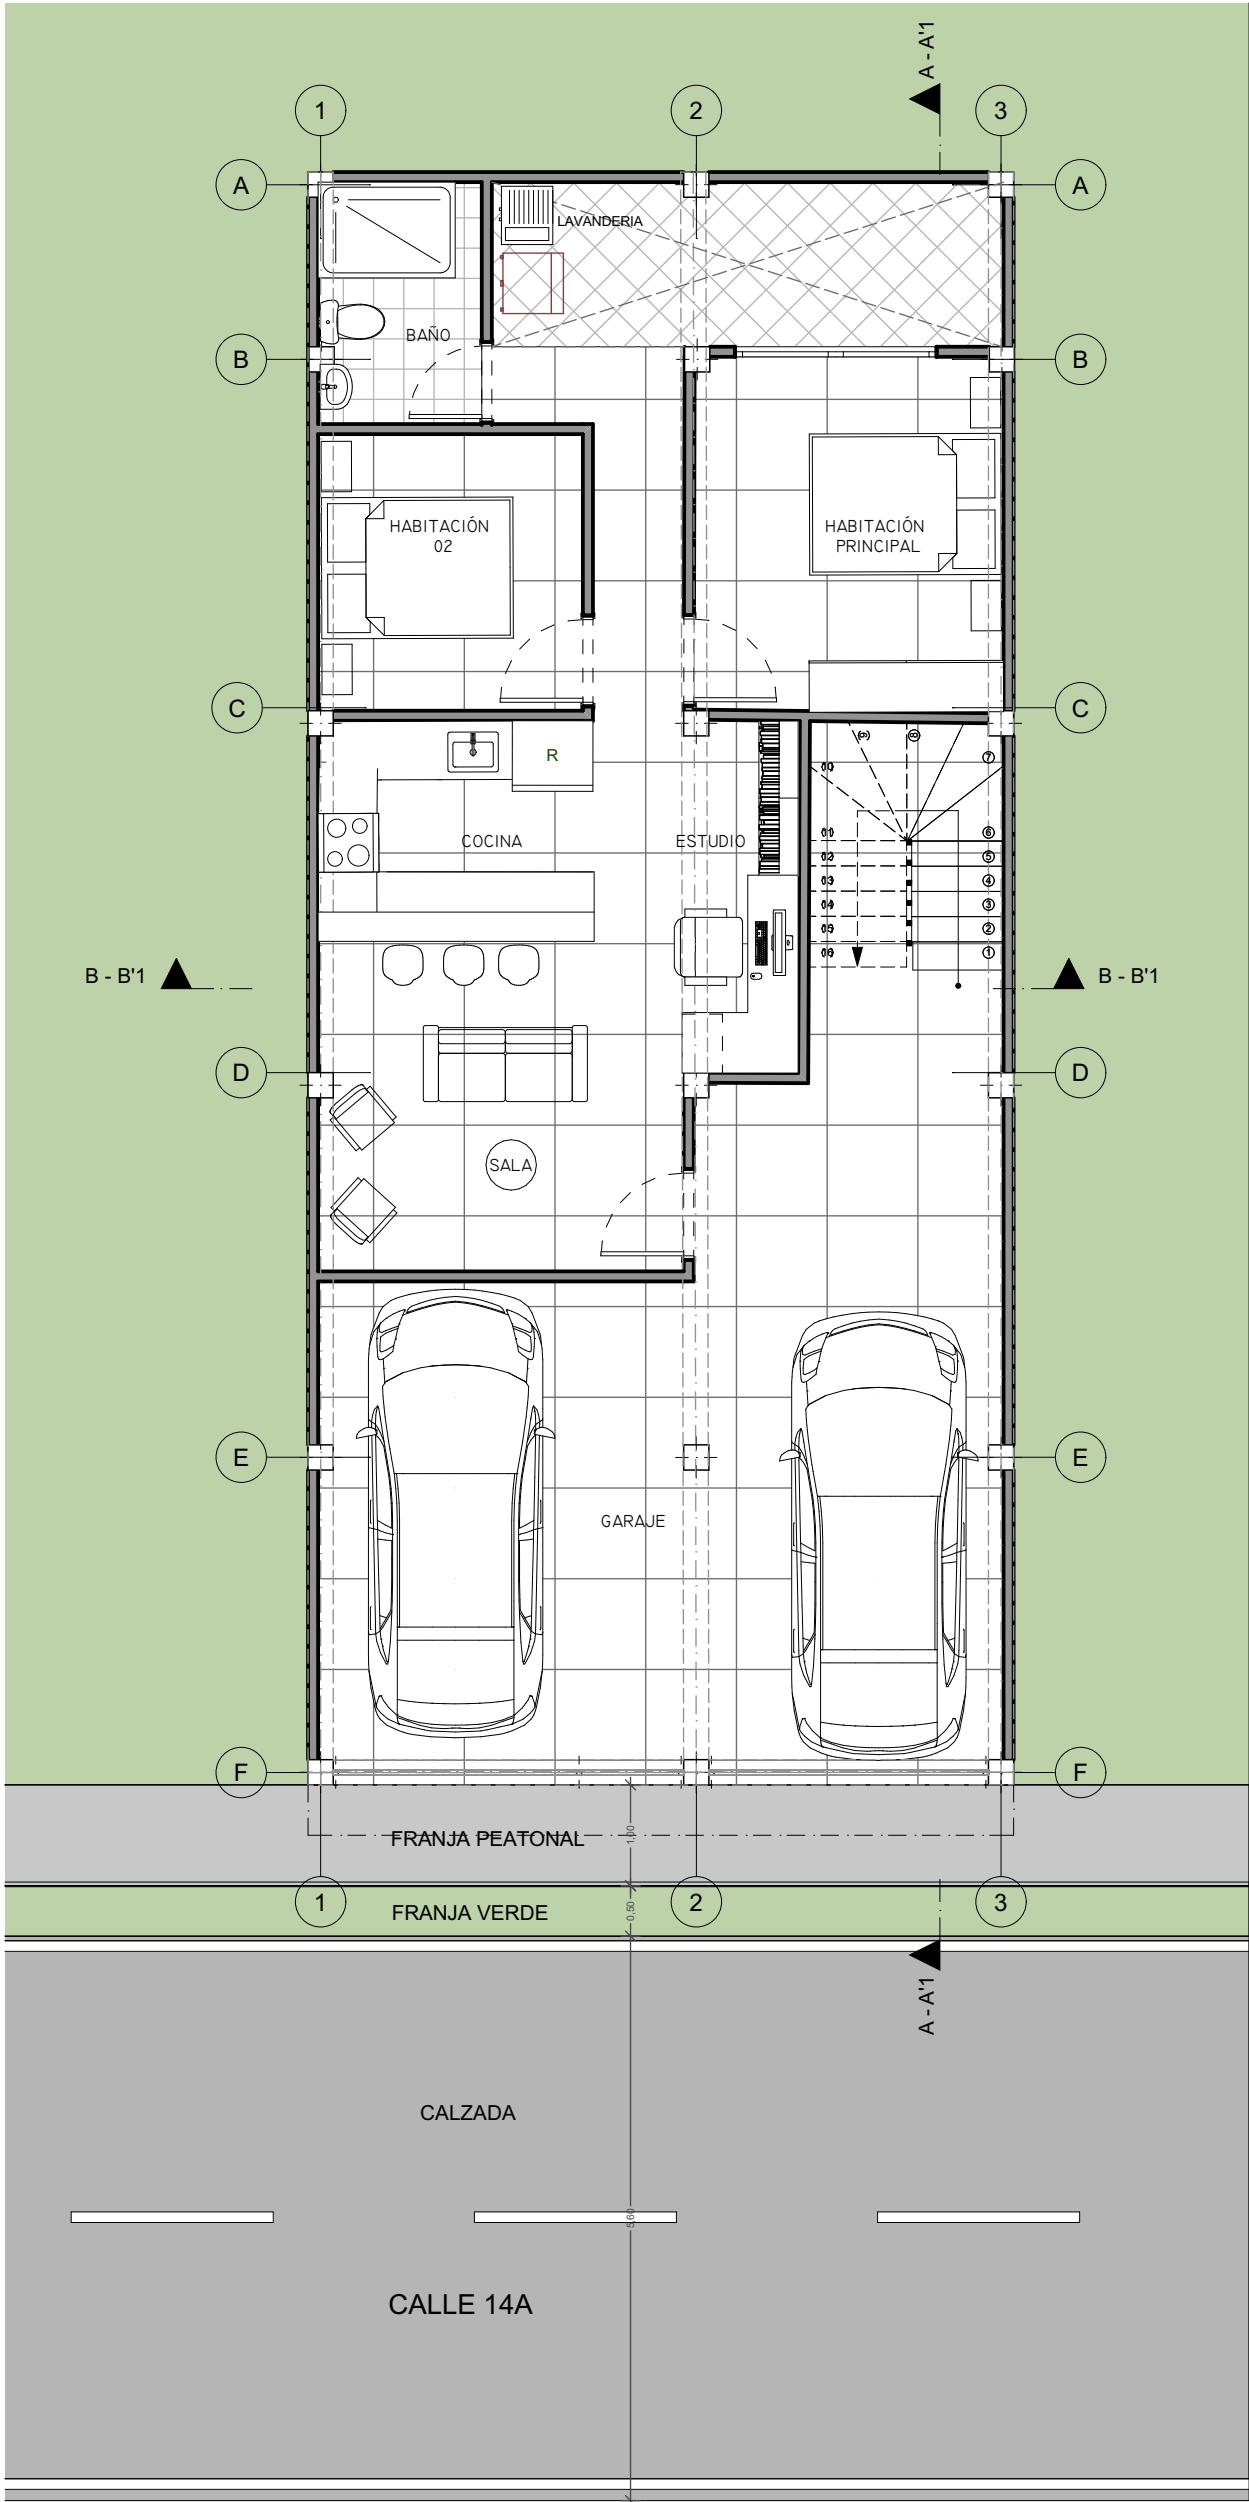


PLANTA DE CUBIERTA

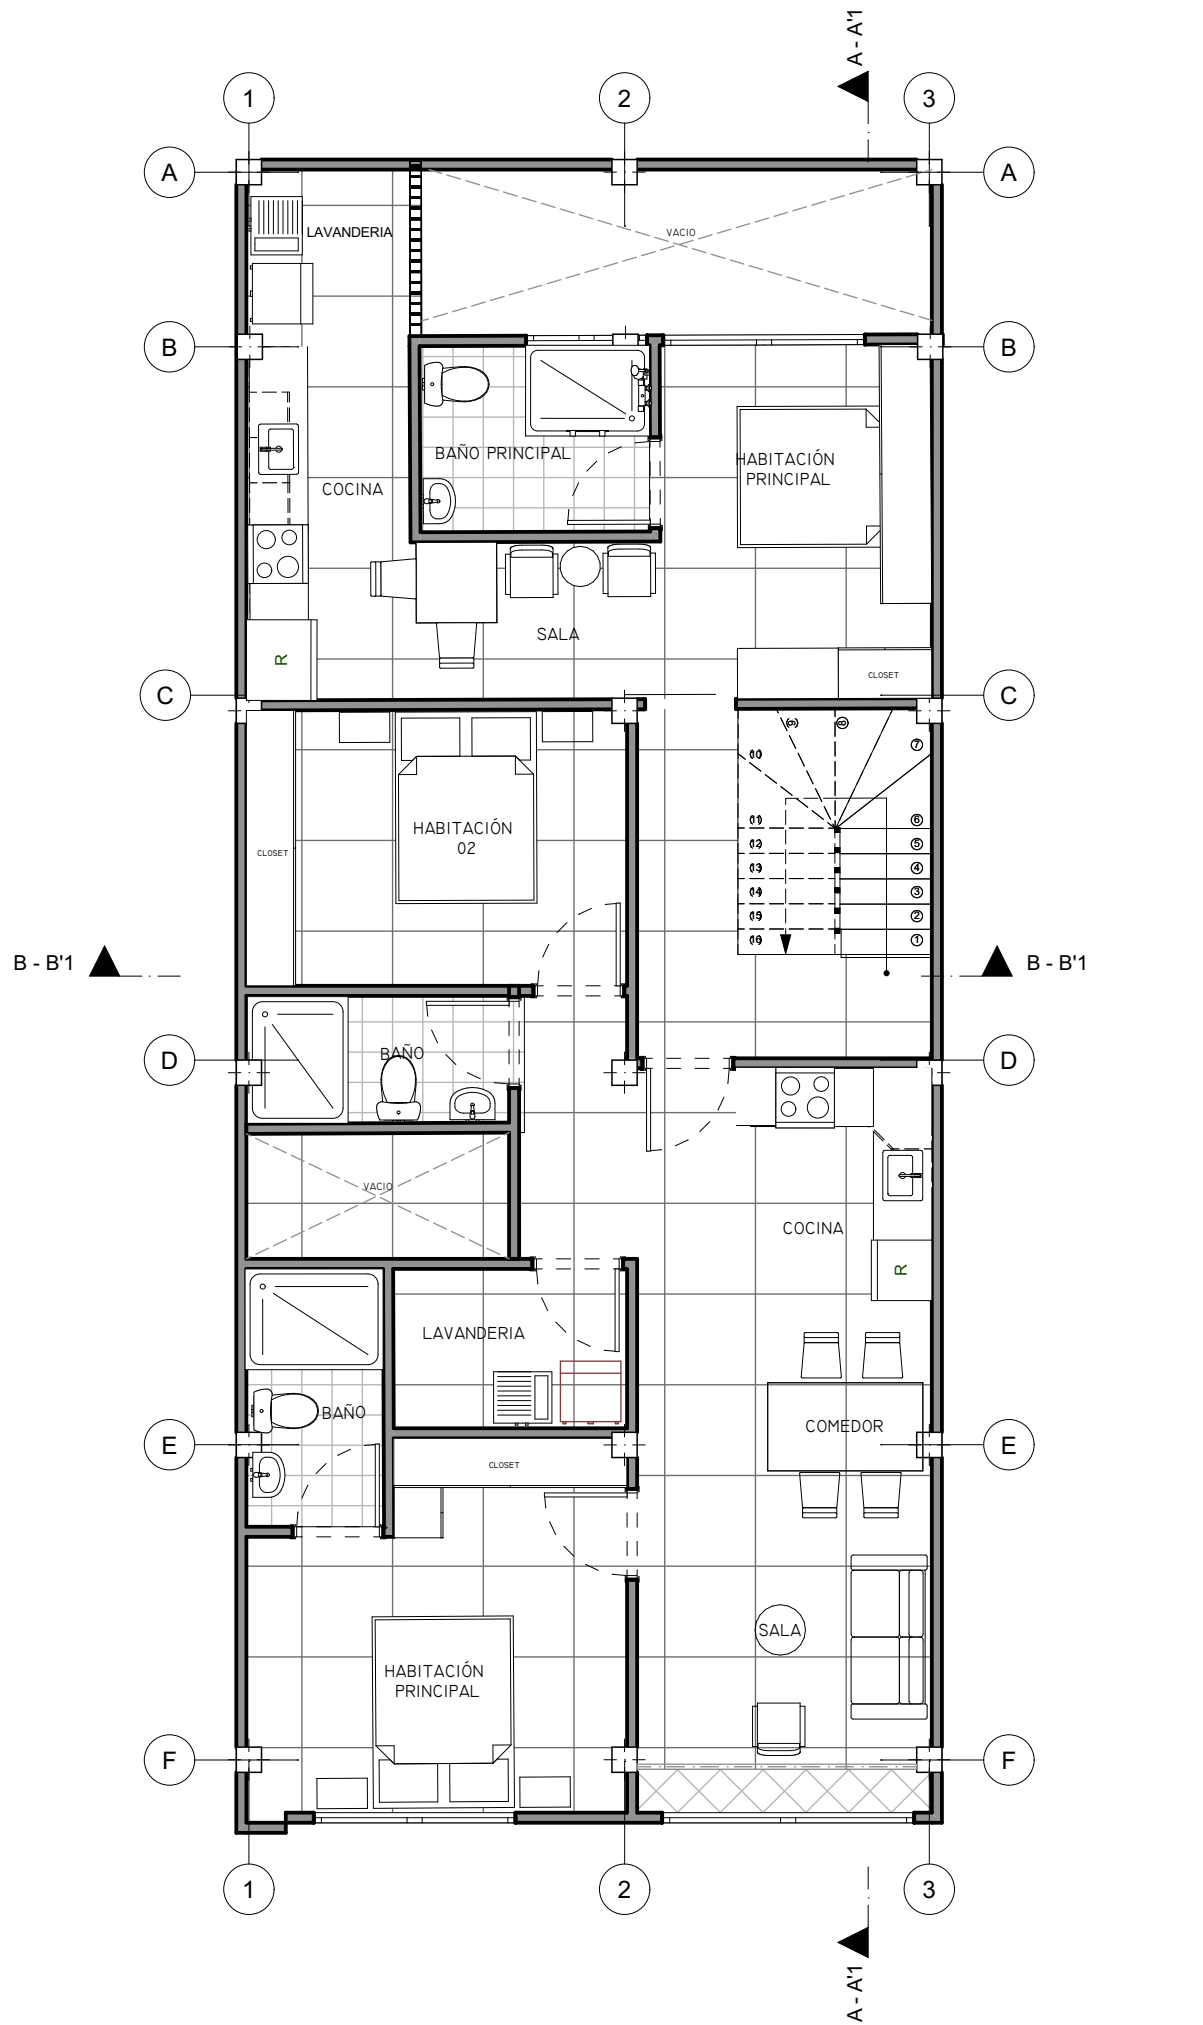


PLANTA TERCER PISO

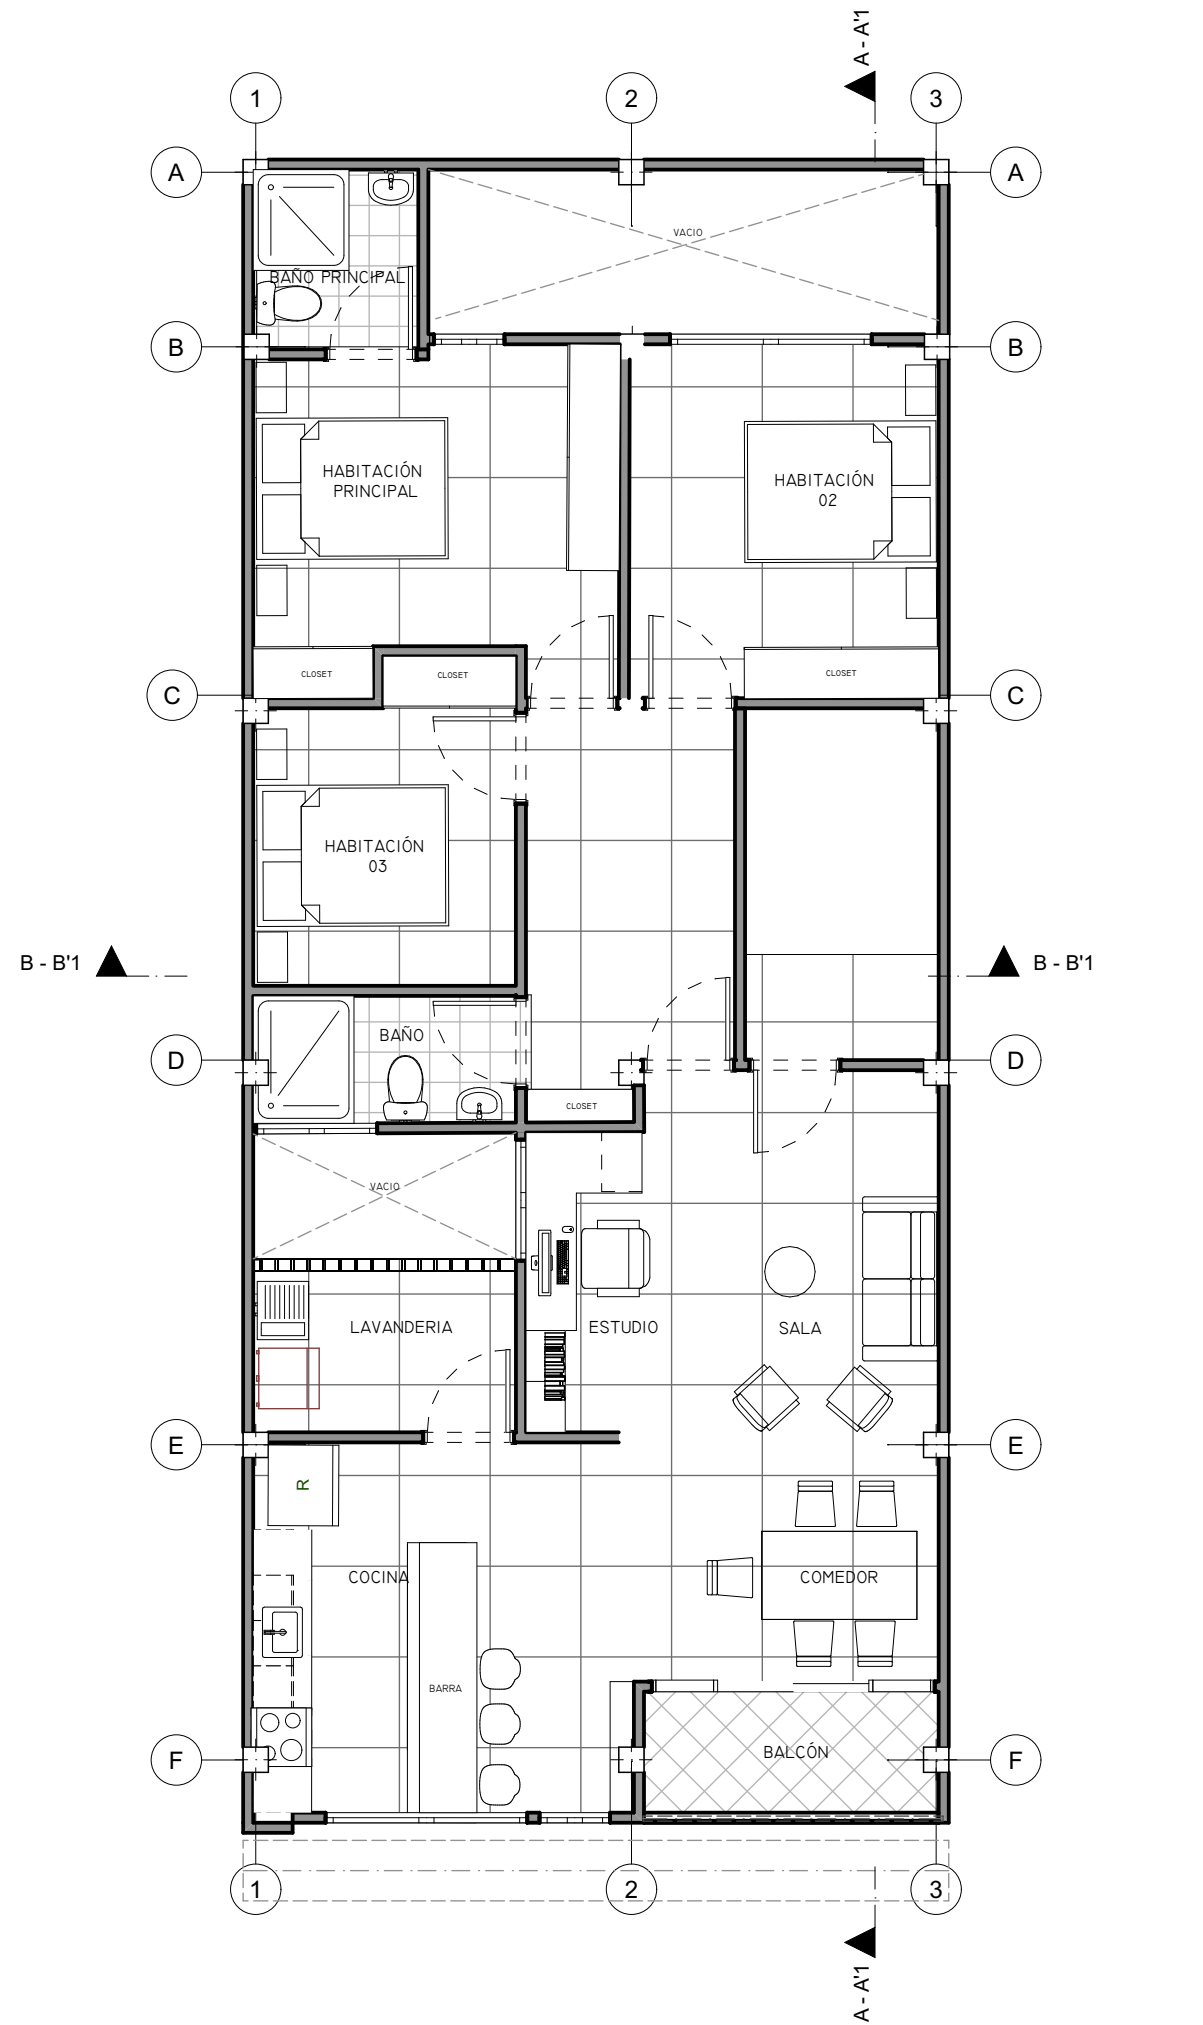


PLANTA DE CUBIERTA

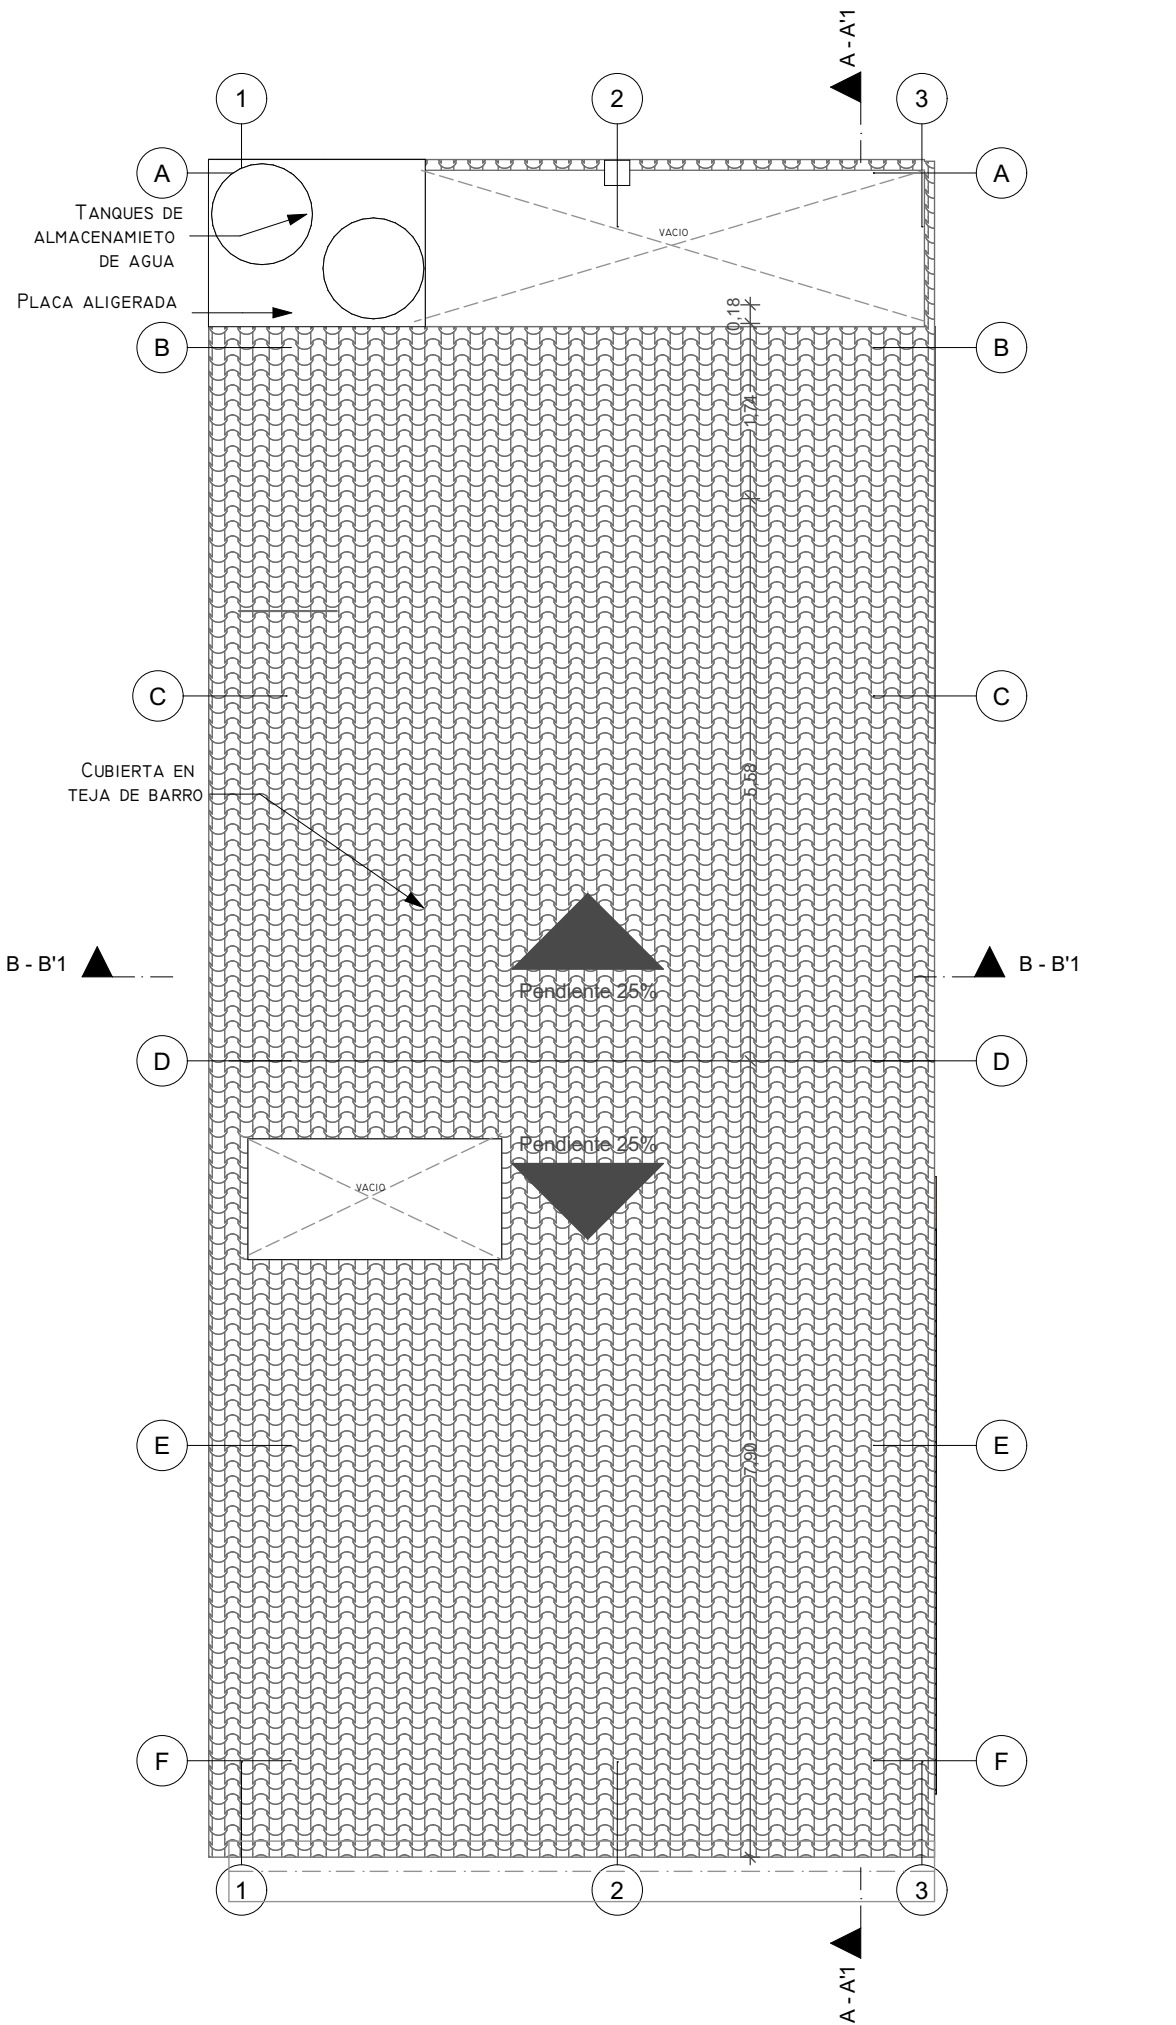


LOCALIZACIÓN

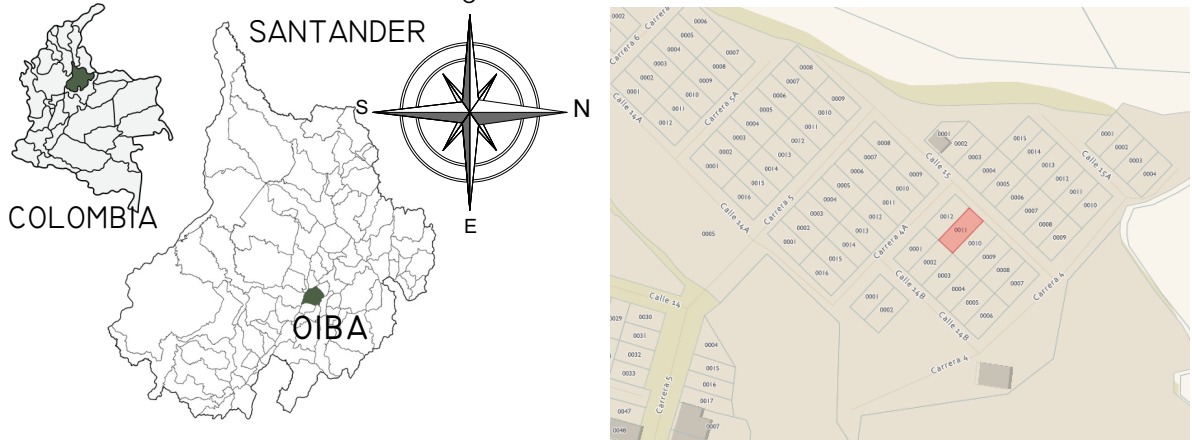

CORTE A-A'

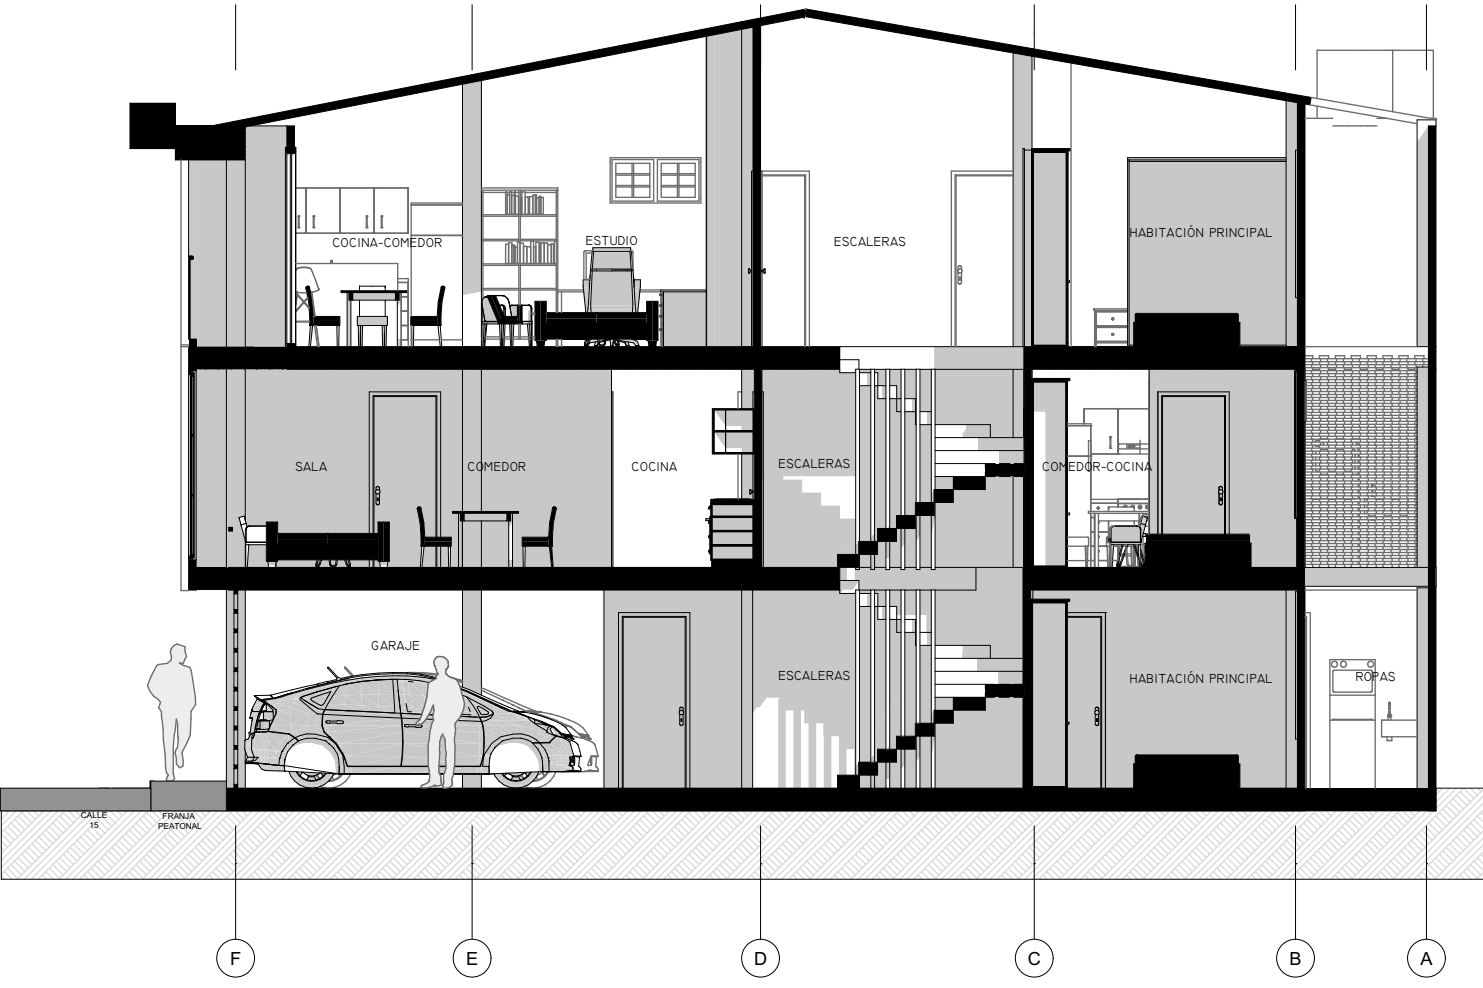

CORTE B-B'

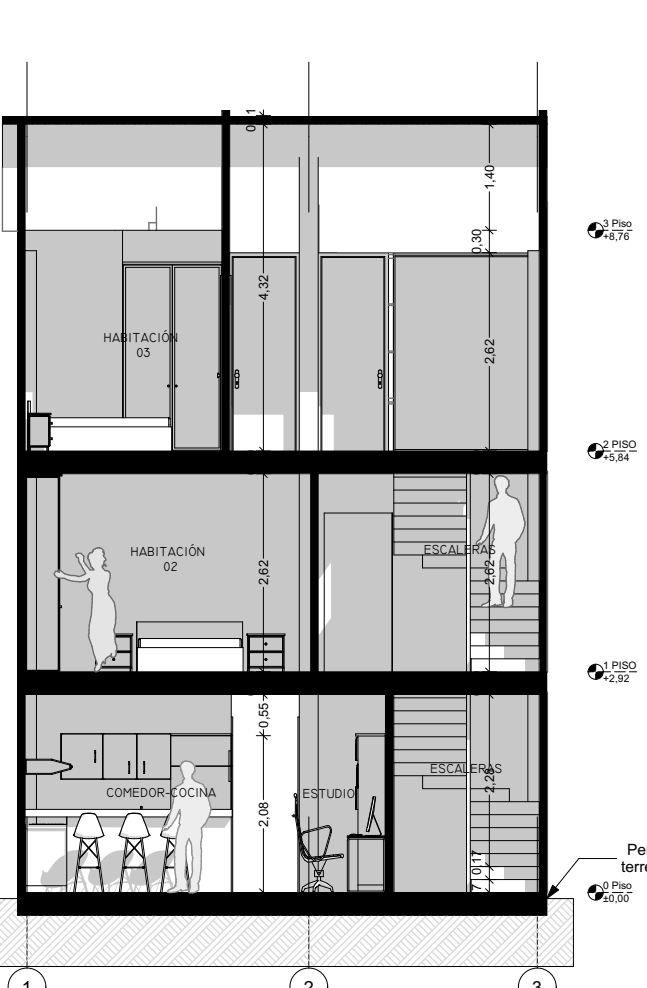

FACHADA PRINCIPAL



PROPIETARIOS:

JESSICA VIVIANA RANGEL

DIRECCIÓN:

CALLE 15 N° 4 - 35, BARRIO VILLAMIRA
OIBA, SANTANDER

APROBÓ:

CONTIENE:

PLANTAS ARQUITECTONICAS, CORTES, FACHADA,
CUADRO DE ÁREAS Y LOCALIZACIÓN

TRAMITE:

LICENCIA DE CONTRUCCIÓN NUEVA

FECHA

OCTUBRE 2025

ESCALA

1:75

PLANO

I DE I

TRAMITA:

ARQ. JESSICA VIVIANA RANGEL ESPINOSA
M. A30632018-109873588