


FACHADA PRINCIPAL

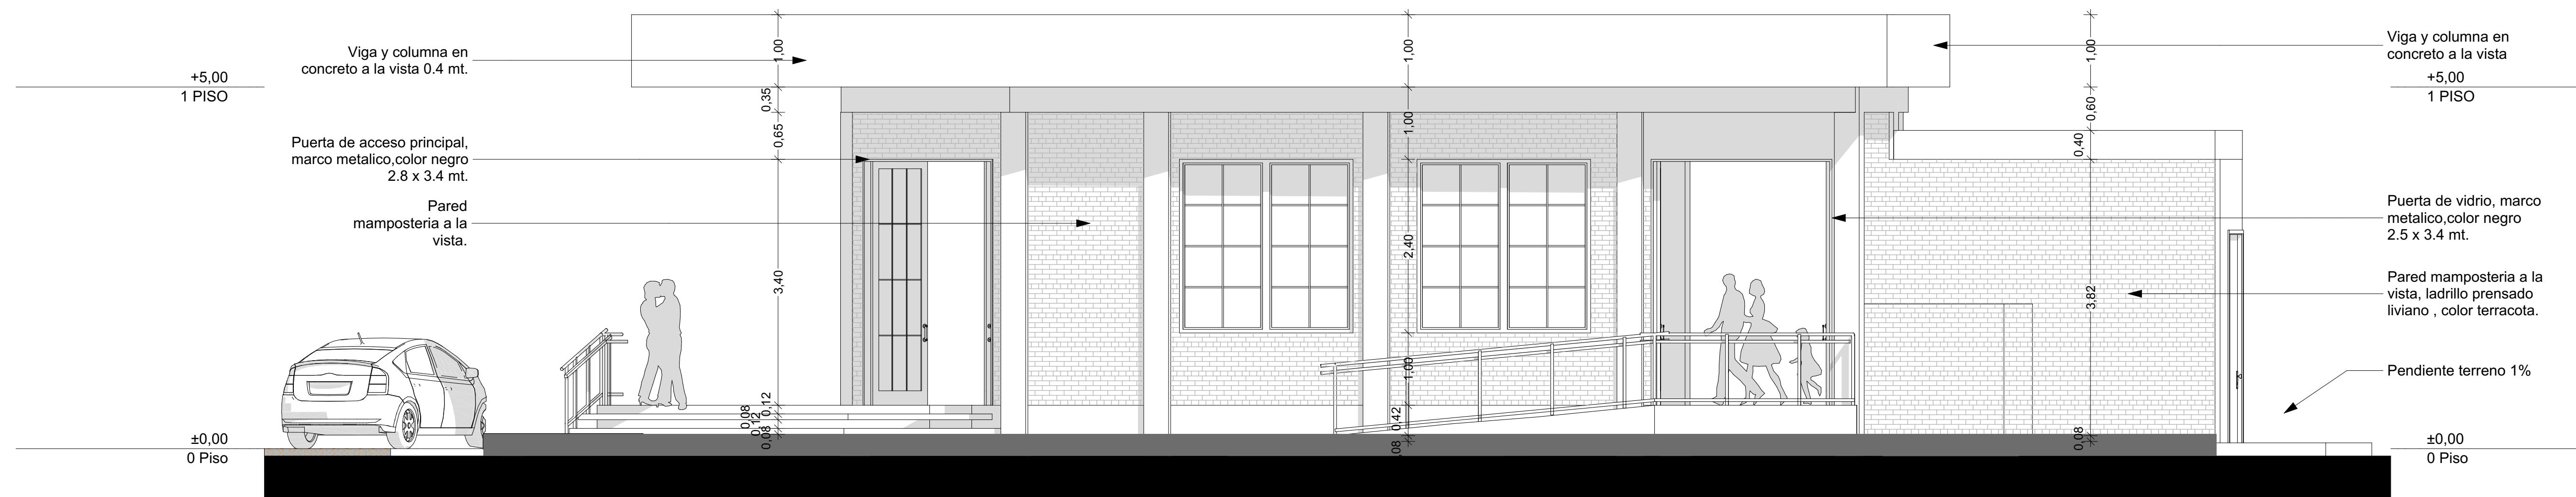



FACHADA LATERAL IZQUIERDA



CORTE LONGITUDINAL



CORTE TRANSVERSAL

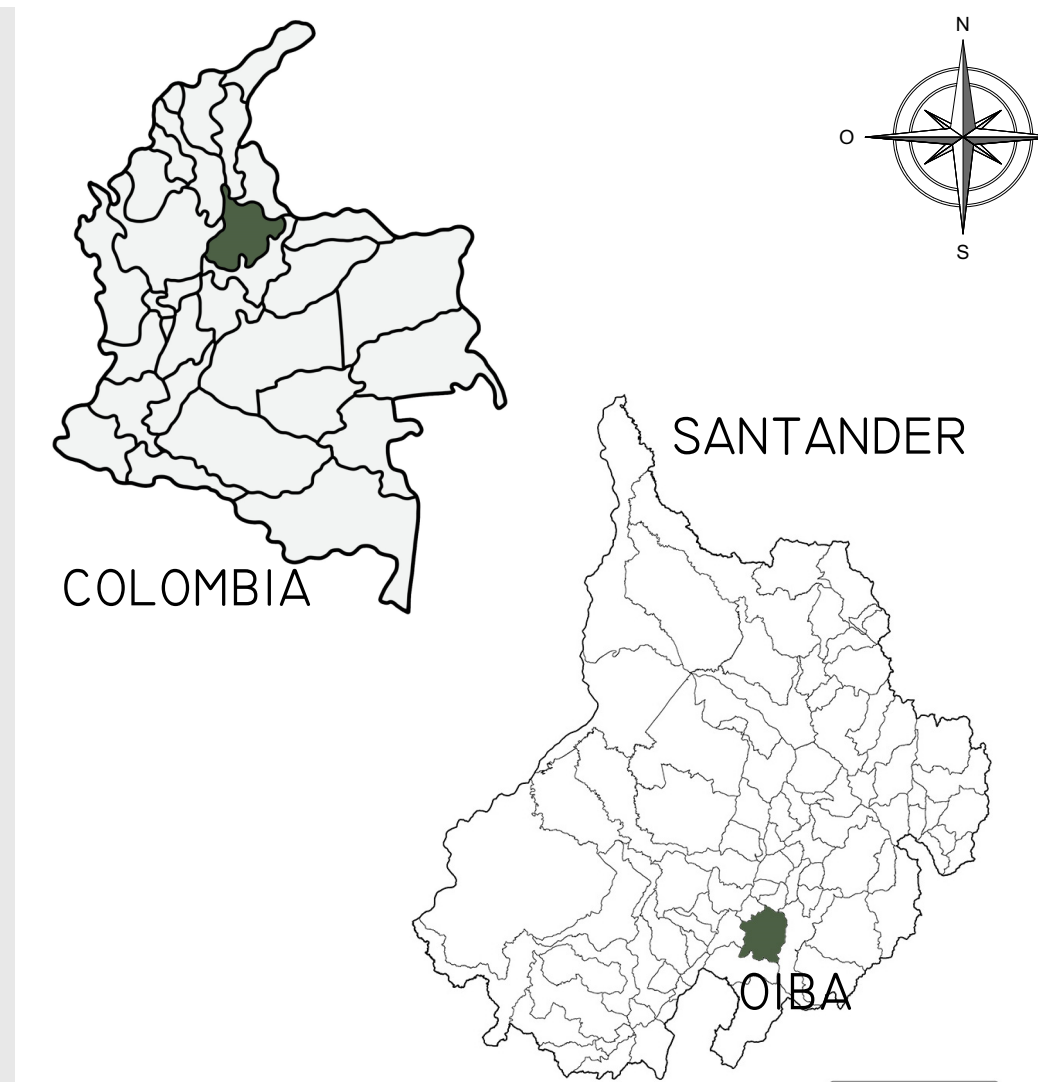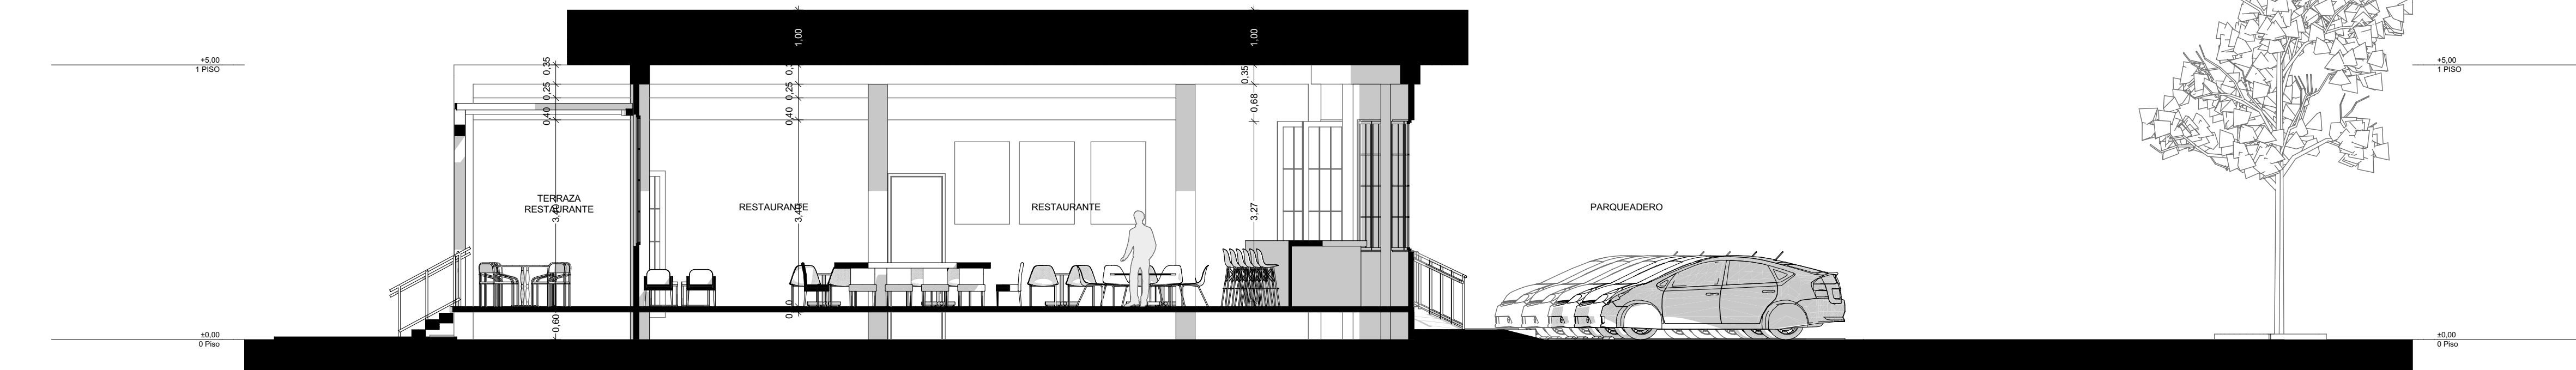

LOCALIZACIÓN

CUADRO DE AREAS	
AREA TOTAL DEL LOTE	7930 M2
AREA CONSTRUIDA ESTRUCTURA 1	110.4 M2
AREA CONSTRUIDA ESTRUCTURA 2 Y 3	312.3 M2
AREA CONSTRUIDA MODULO BAÑOS	67.9 M2
AREA TOTAL CONSTRUIDA	409.6 M2

PROPIETARIOS:		APROBÓ:	OBSERVACIONES	FECHA	CONTIENE
PACHSAN OIBA LIMITADA				ENERO 2025	FACHADAS, CORTES, ESTRUCTURA 2 Y 3
DIRECCIÓN:	DISEÑO:			ESCALA	PLANO
PREDIO URBANO LOTE AI OIBA, SANTANDER	ARQ. JESSICA VIVIANA RANGEL ESPINOSA M. A30632018-109873588			1:50	4 DE 4
					CONSTRUCCION OBRA NUEVA