




PLANTA PRIMER PISO

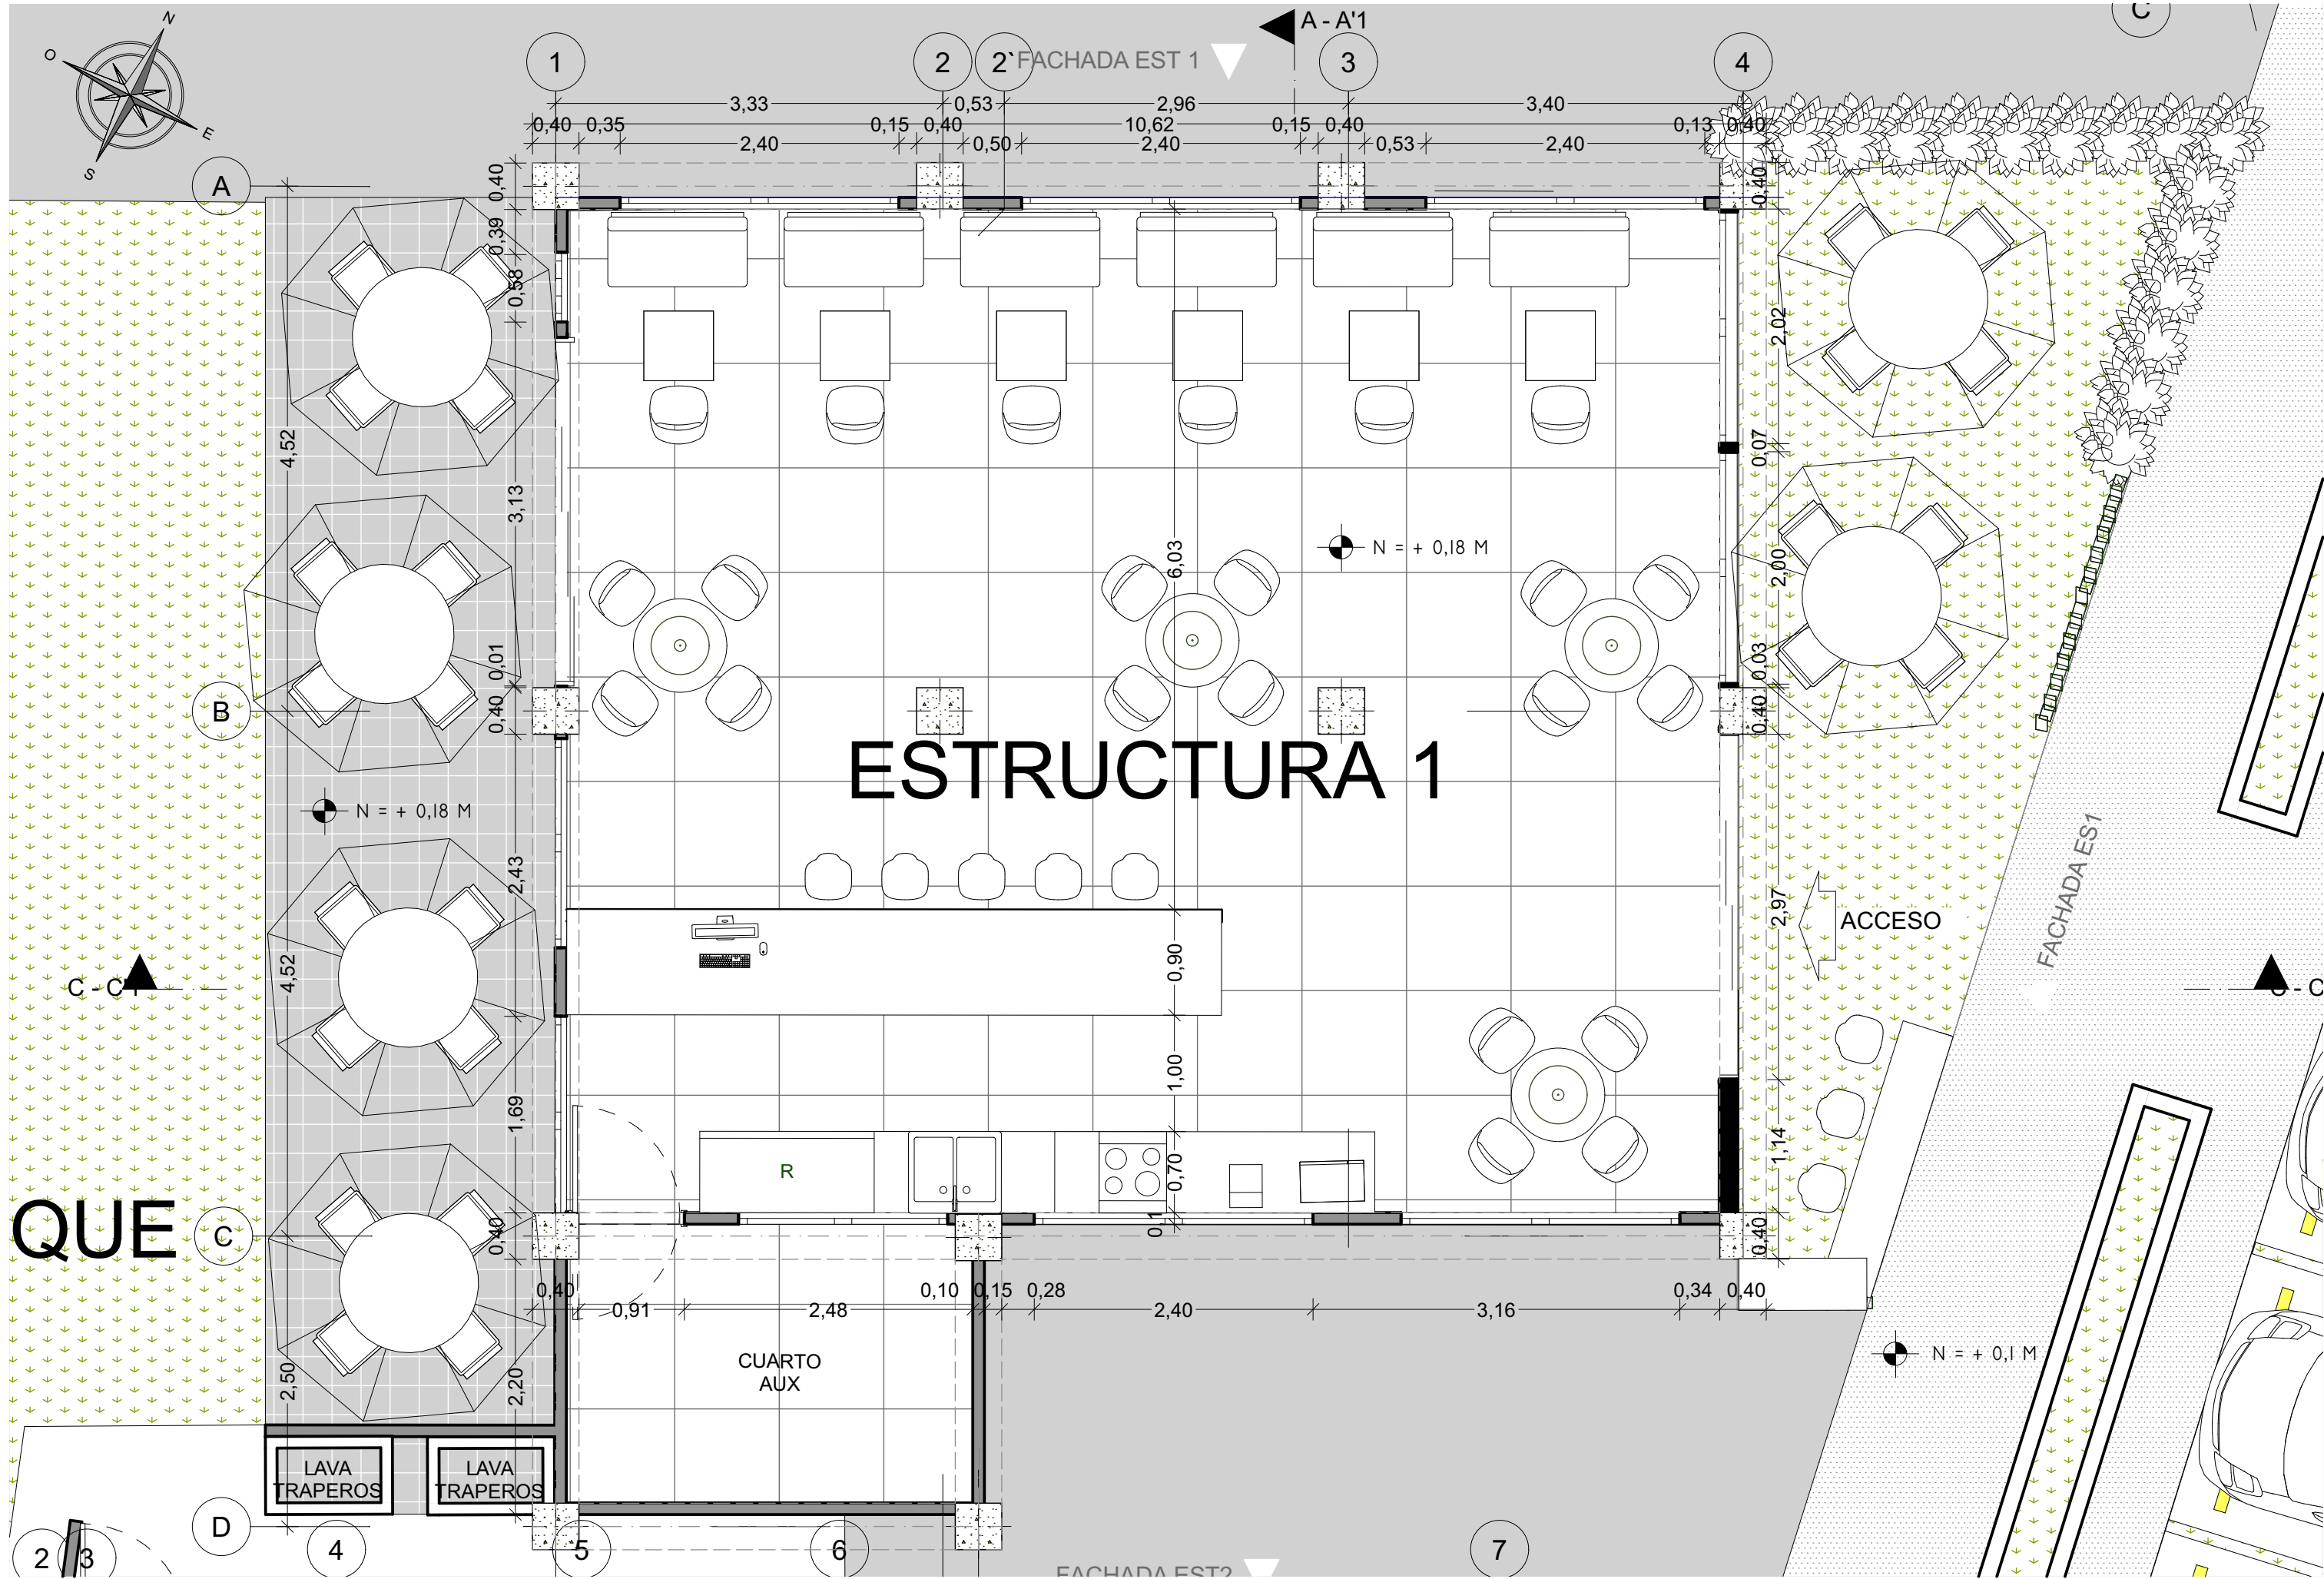


PLANTA DE CUBIERTA

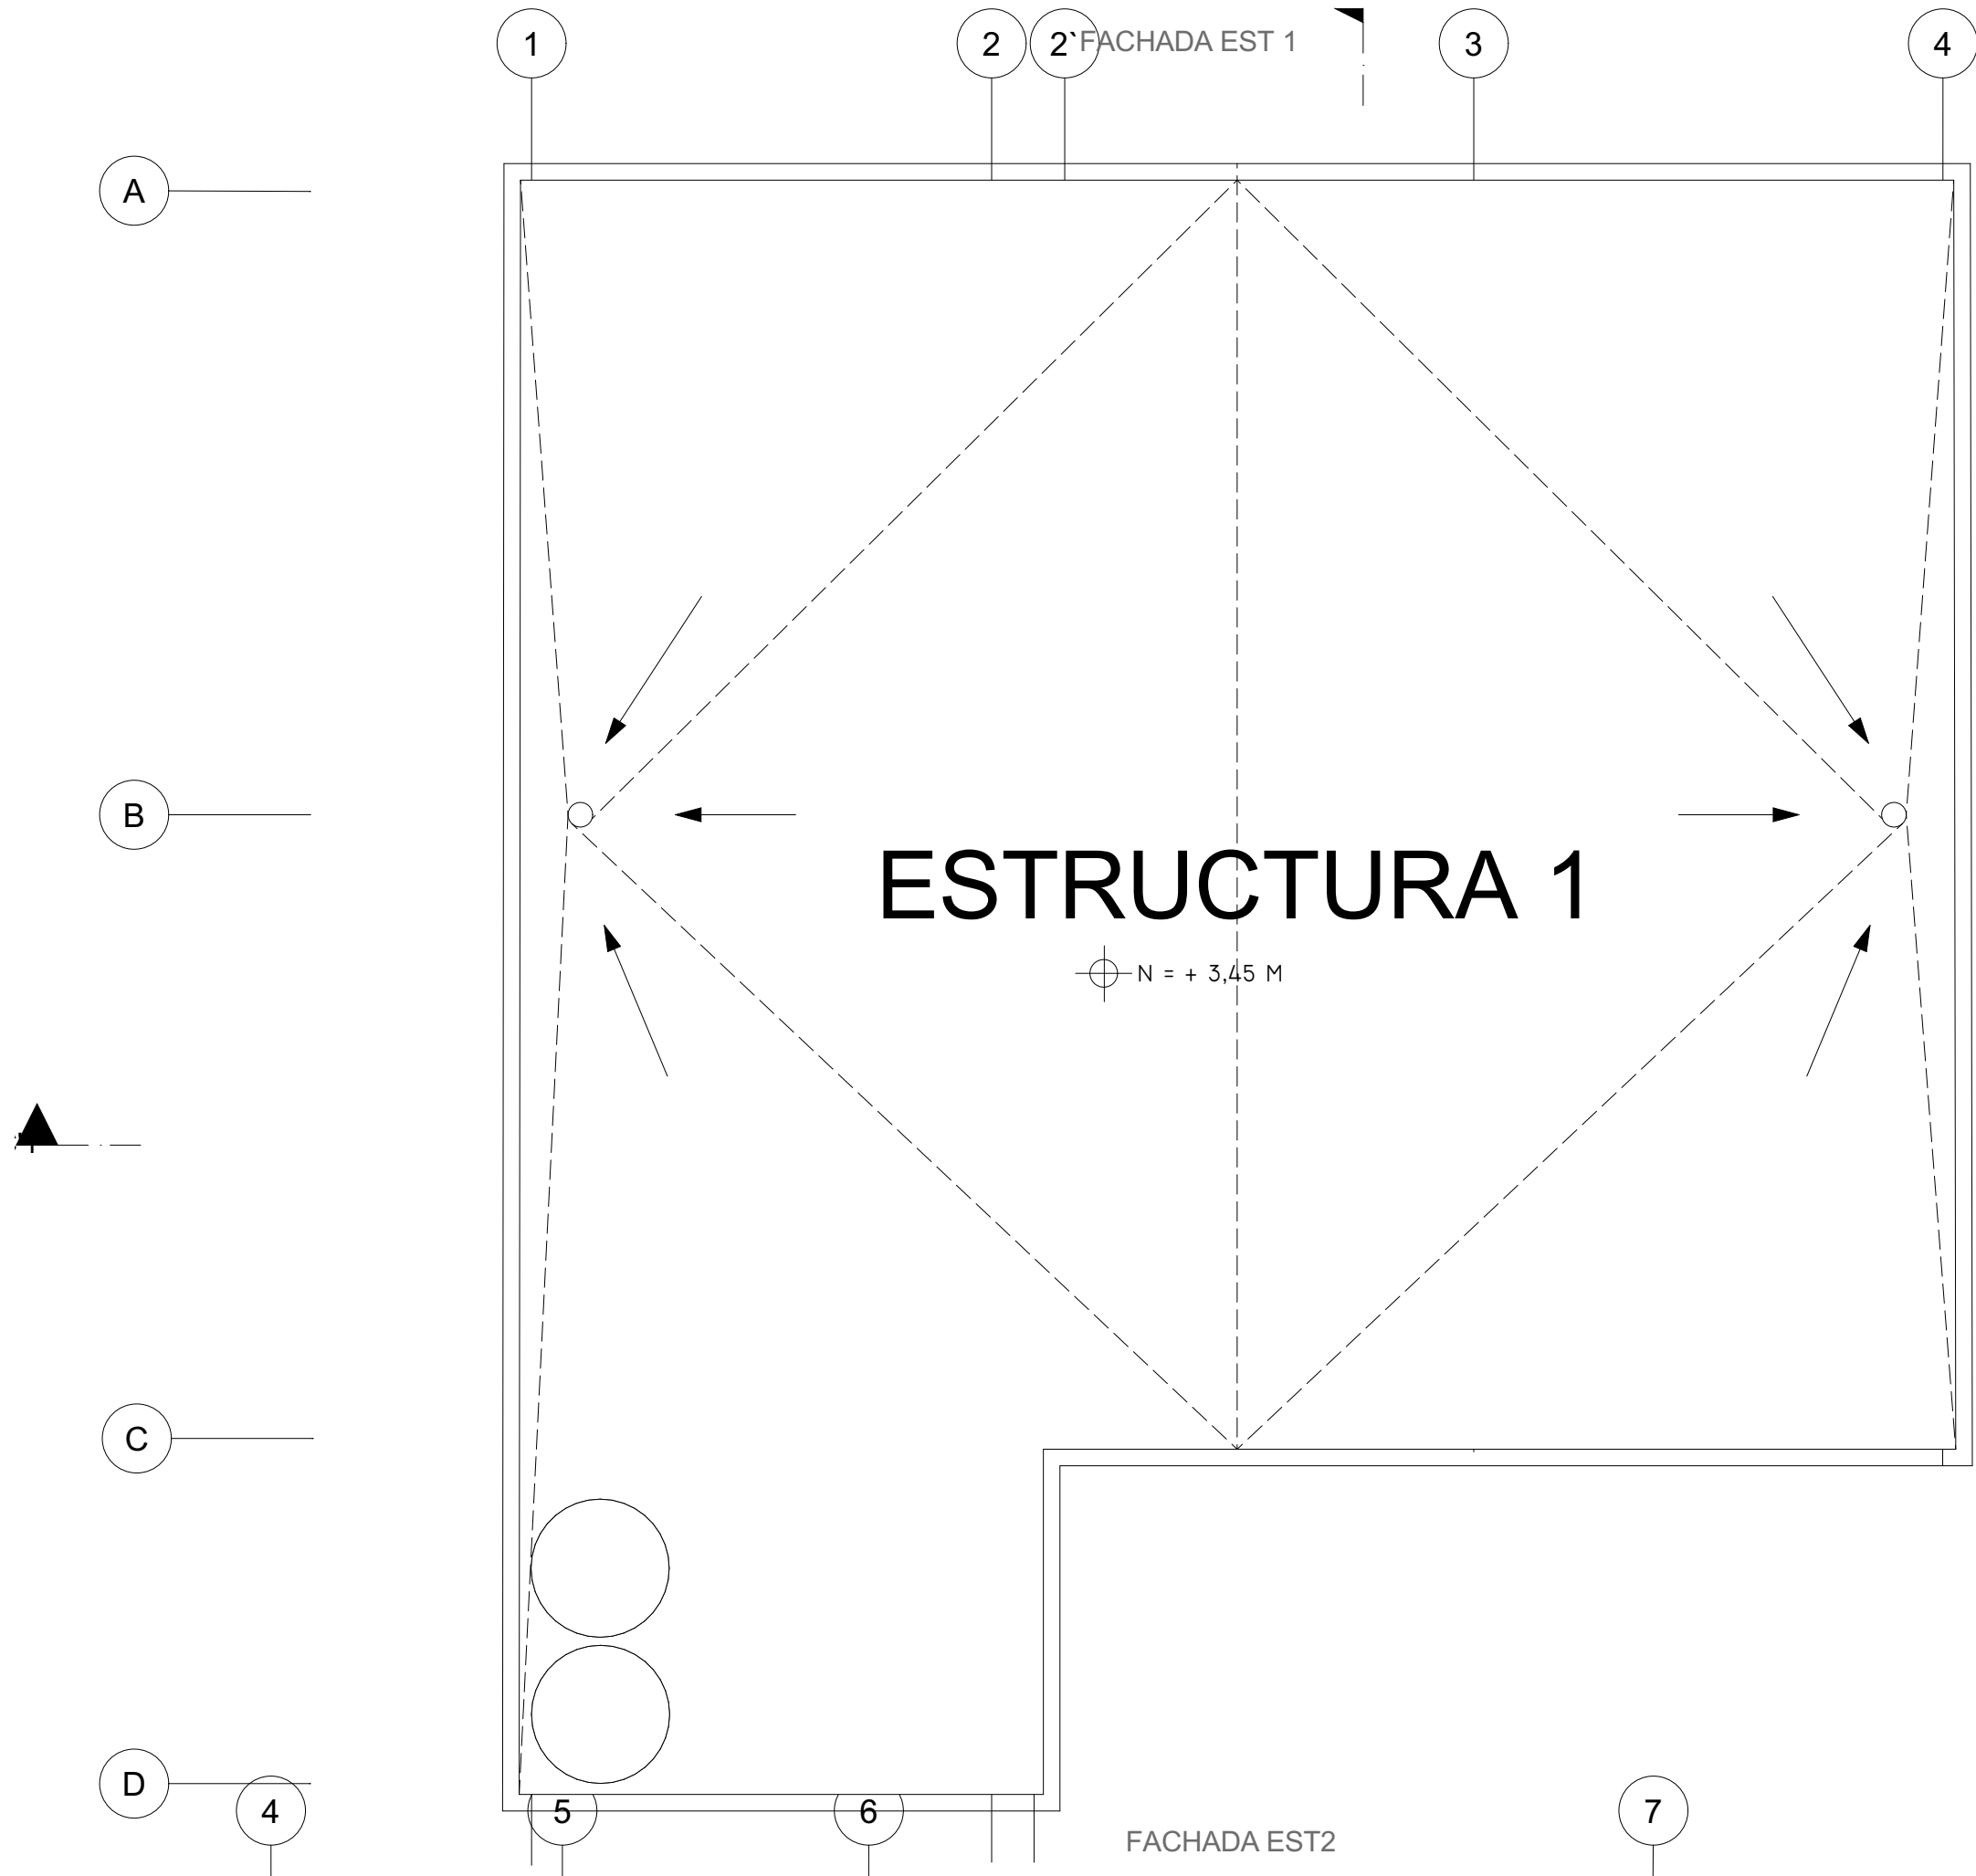


FACHADA PRINCIPAL

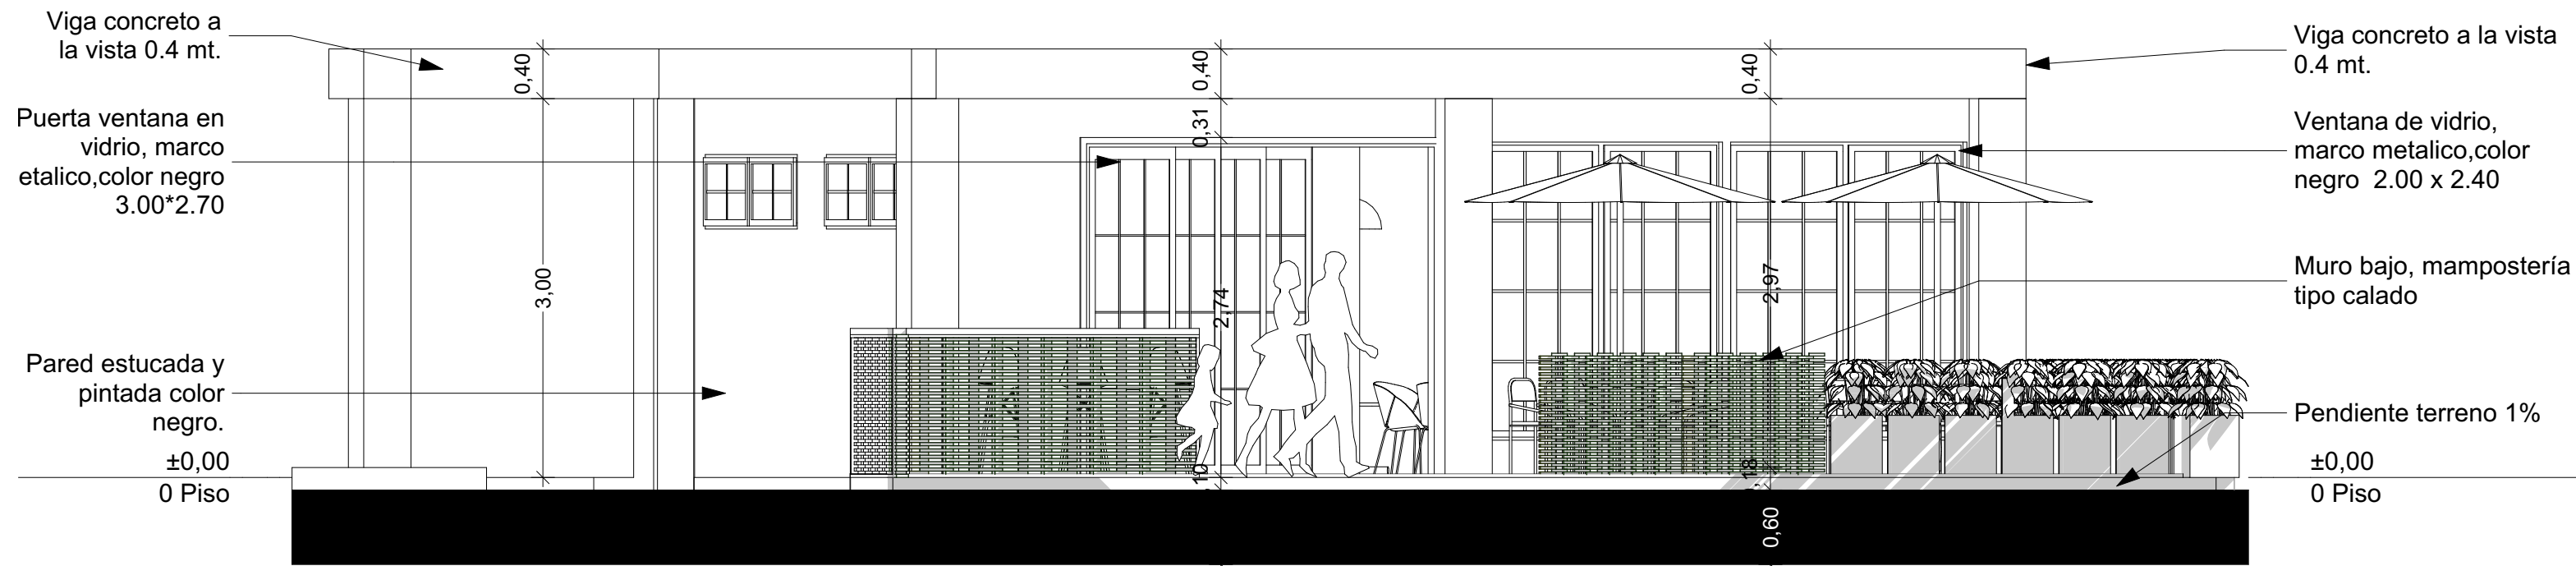


CORTE LONGITUDINAL

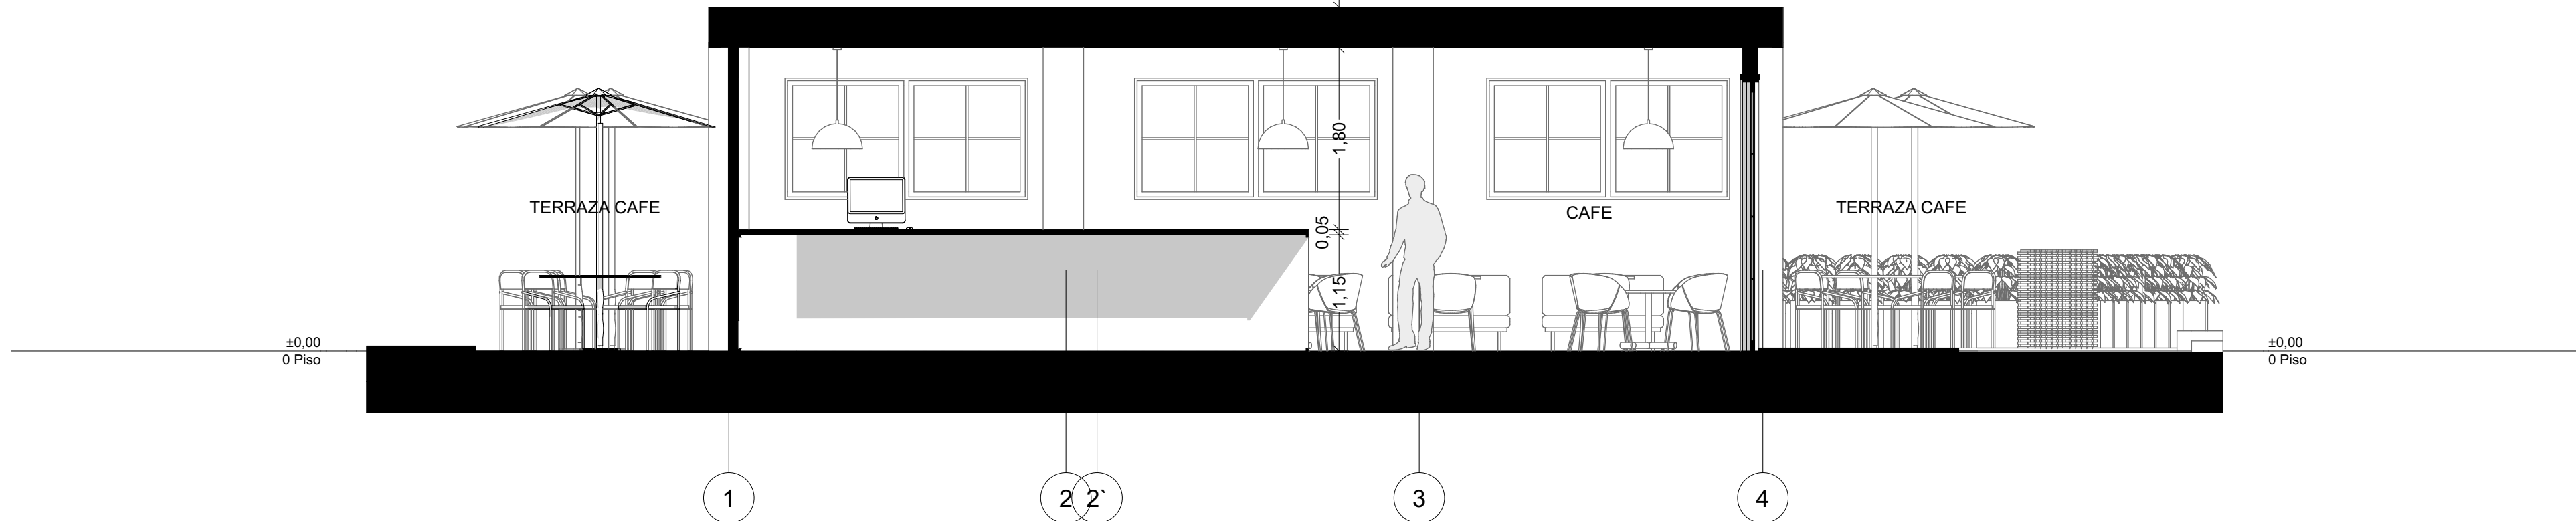

FACHADA LATERAL DERECHA

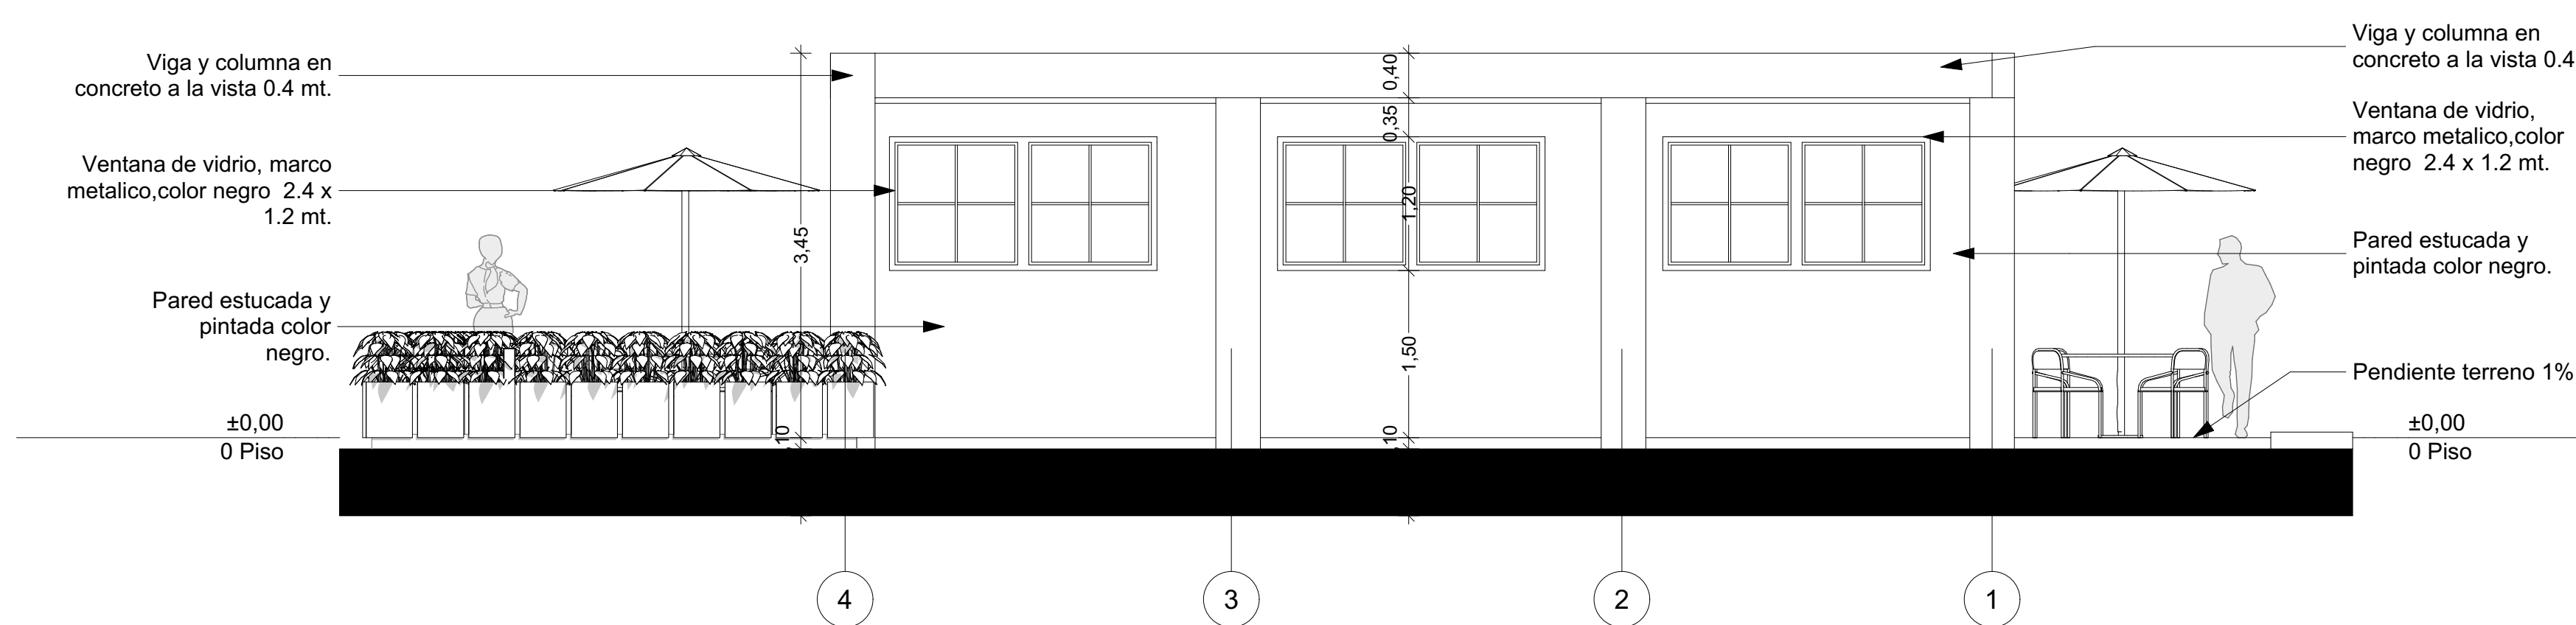

CORTE TRANSVERSAL

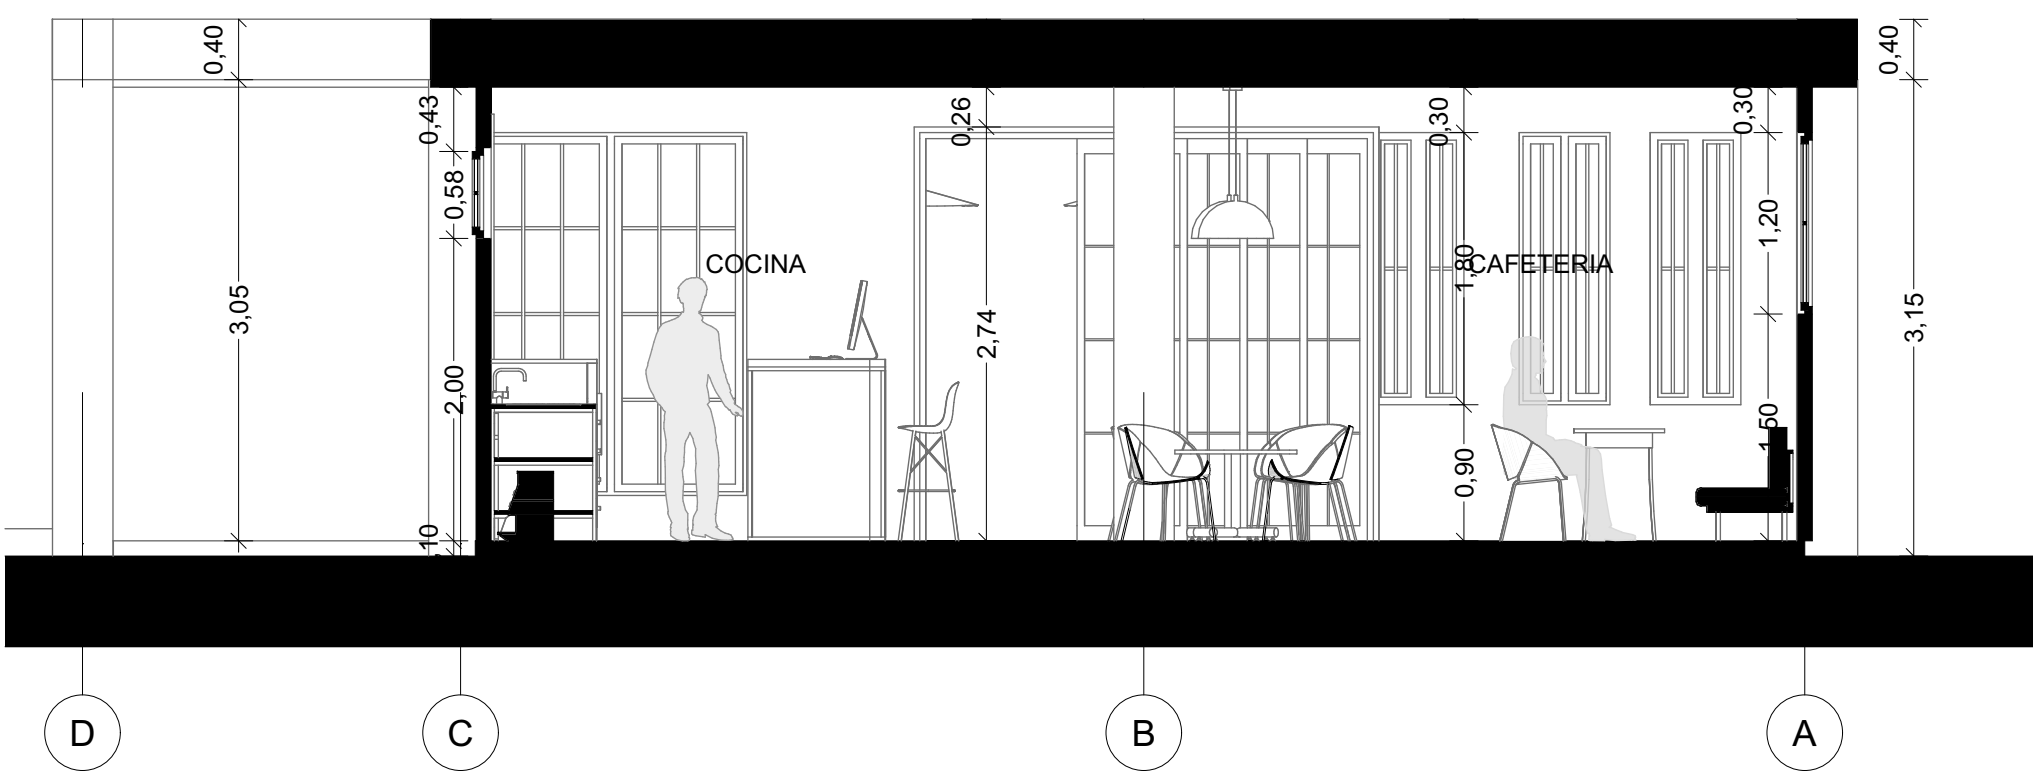

PROPIETARIOS: PACHSAN OIBA LIMITADA	APROBÓ: 	OBSERVACIONES 	FECHA ENERO 2025	CONTIENE ESTRUCTURA I PLANTA ARQUITECTONICA Y CUBIERTA
DIRECCIÓN: PREDIO URBANO LOTE AI OIBA, SANTANDER	DISEÑO: ARQ. JESSICA VIVIANA RANGEL ESPINOSA M. A30632018-I09873588		ESCALA 1:50	TRAMITE CONSTRUCCION OBRA NUEVA
			PLANO 2 DE 4	