


PLANTA PRIMER PISO




FACHADA PRINCIPAL

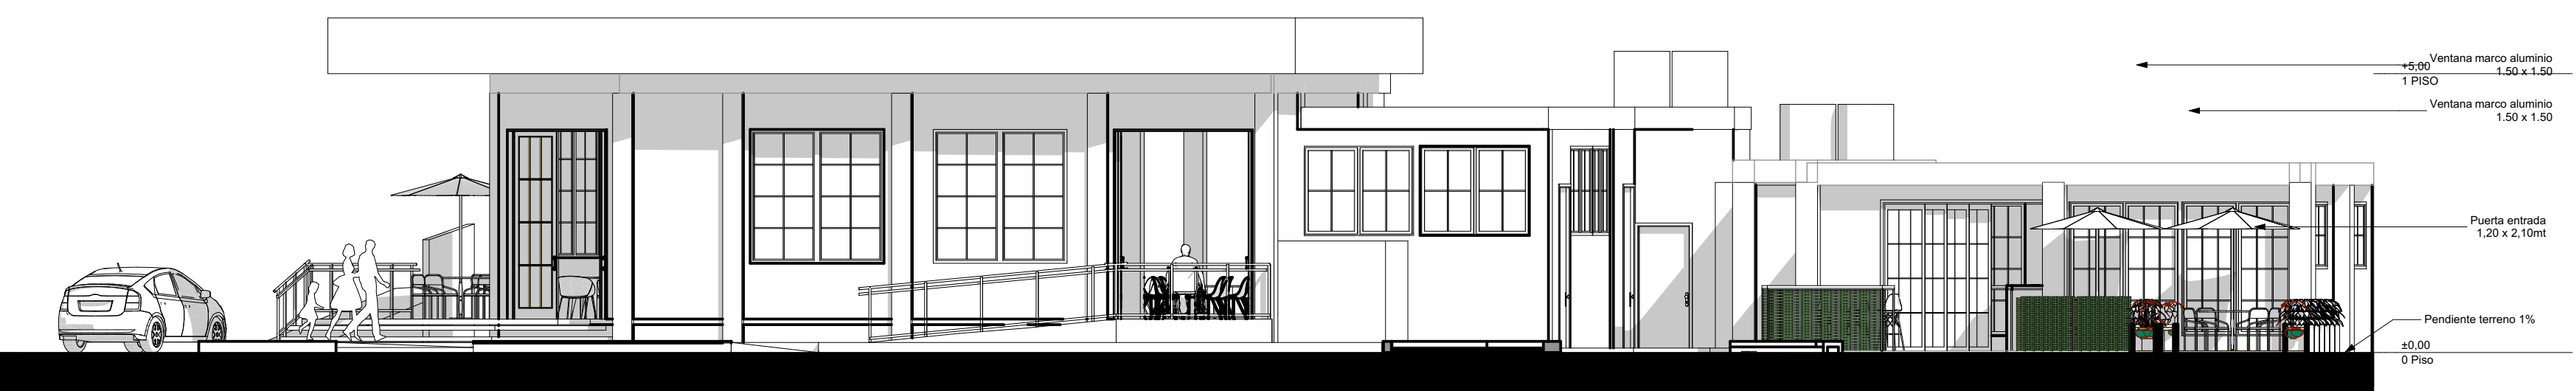


FACHADA LATERAL IZQUIERDA



CORTE LONGITUDINAL

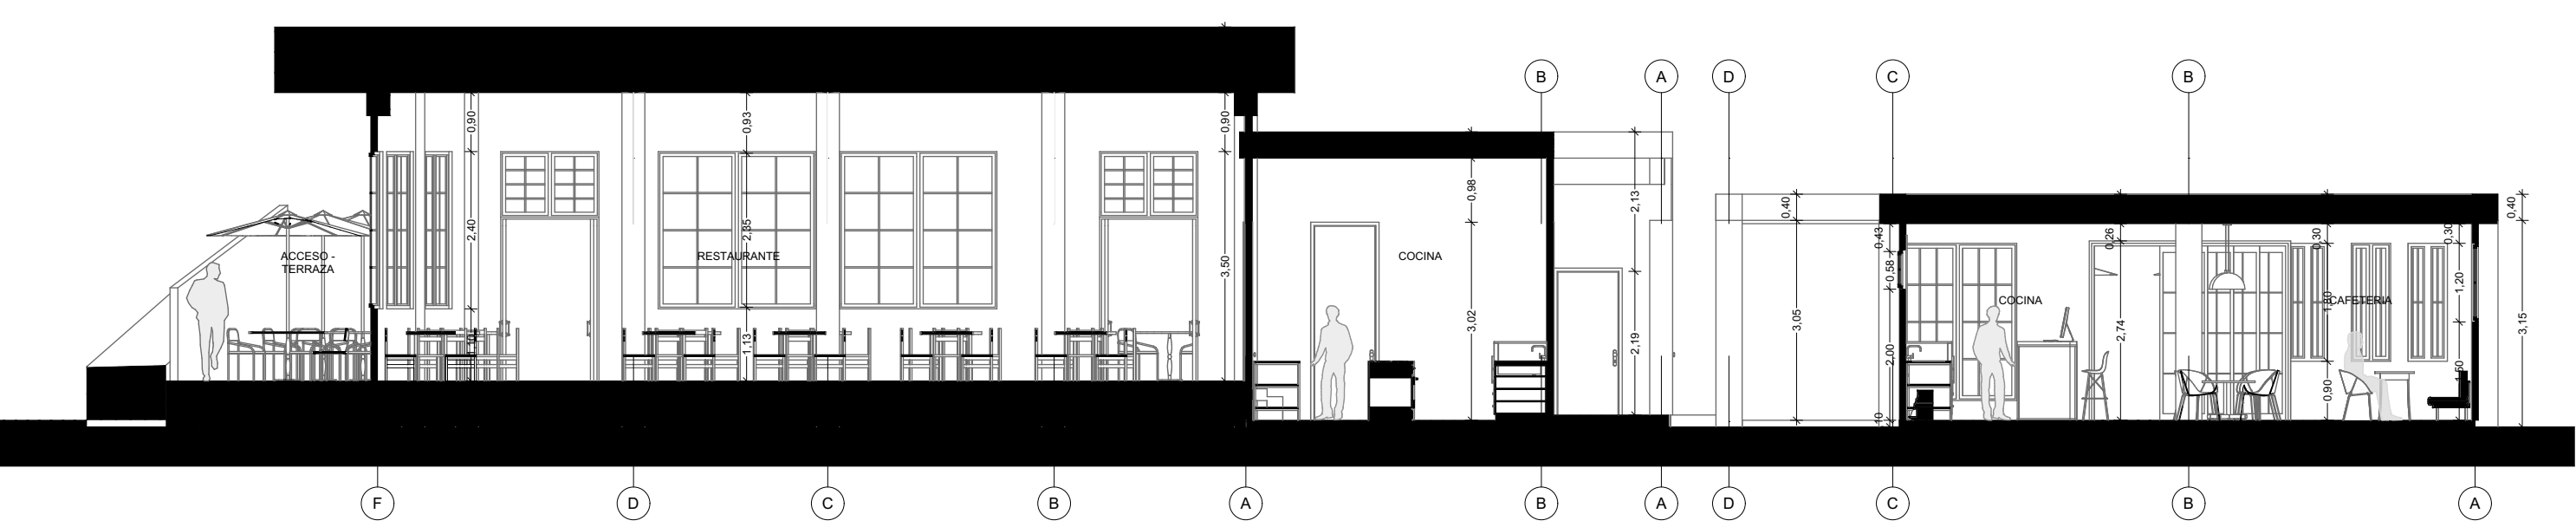

CORTE TRANSVERSAL

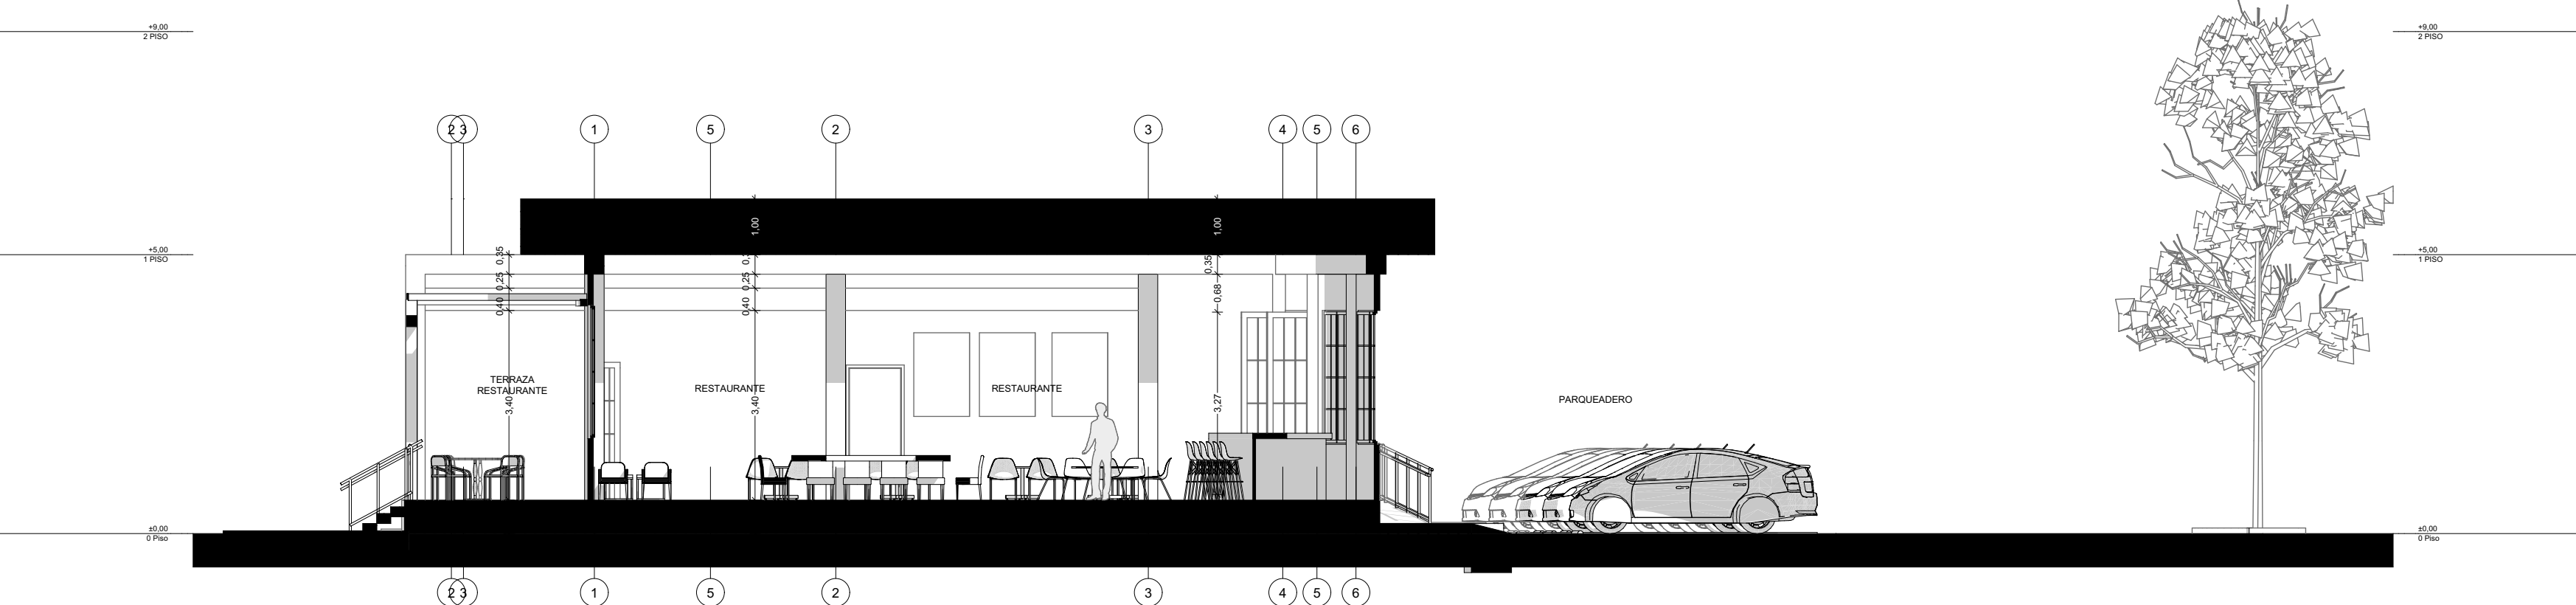

PROPIETARIOS:				APROBÓ:		OBSERVACIONES		FECHA		CONTIENE	
PACHSAN OIBA LIMITADA								ENERO 2025		PLANTA GENERAL, CORTES Y FACHADAS	
DIRECCIÓN:		DISEÑO:						ESCALA		PLANO	
PREDIO URBANO LOTE AI OIBA, SANTANDER		ARQ. JESSICA VIVIANA RANGEL ESPINOSA M. A30632018-I09873588						1:100		I DE 4	
										CONSTRUCCION OBRA NUEVA	