




PLANTA PRIMER PISO

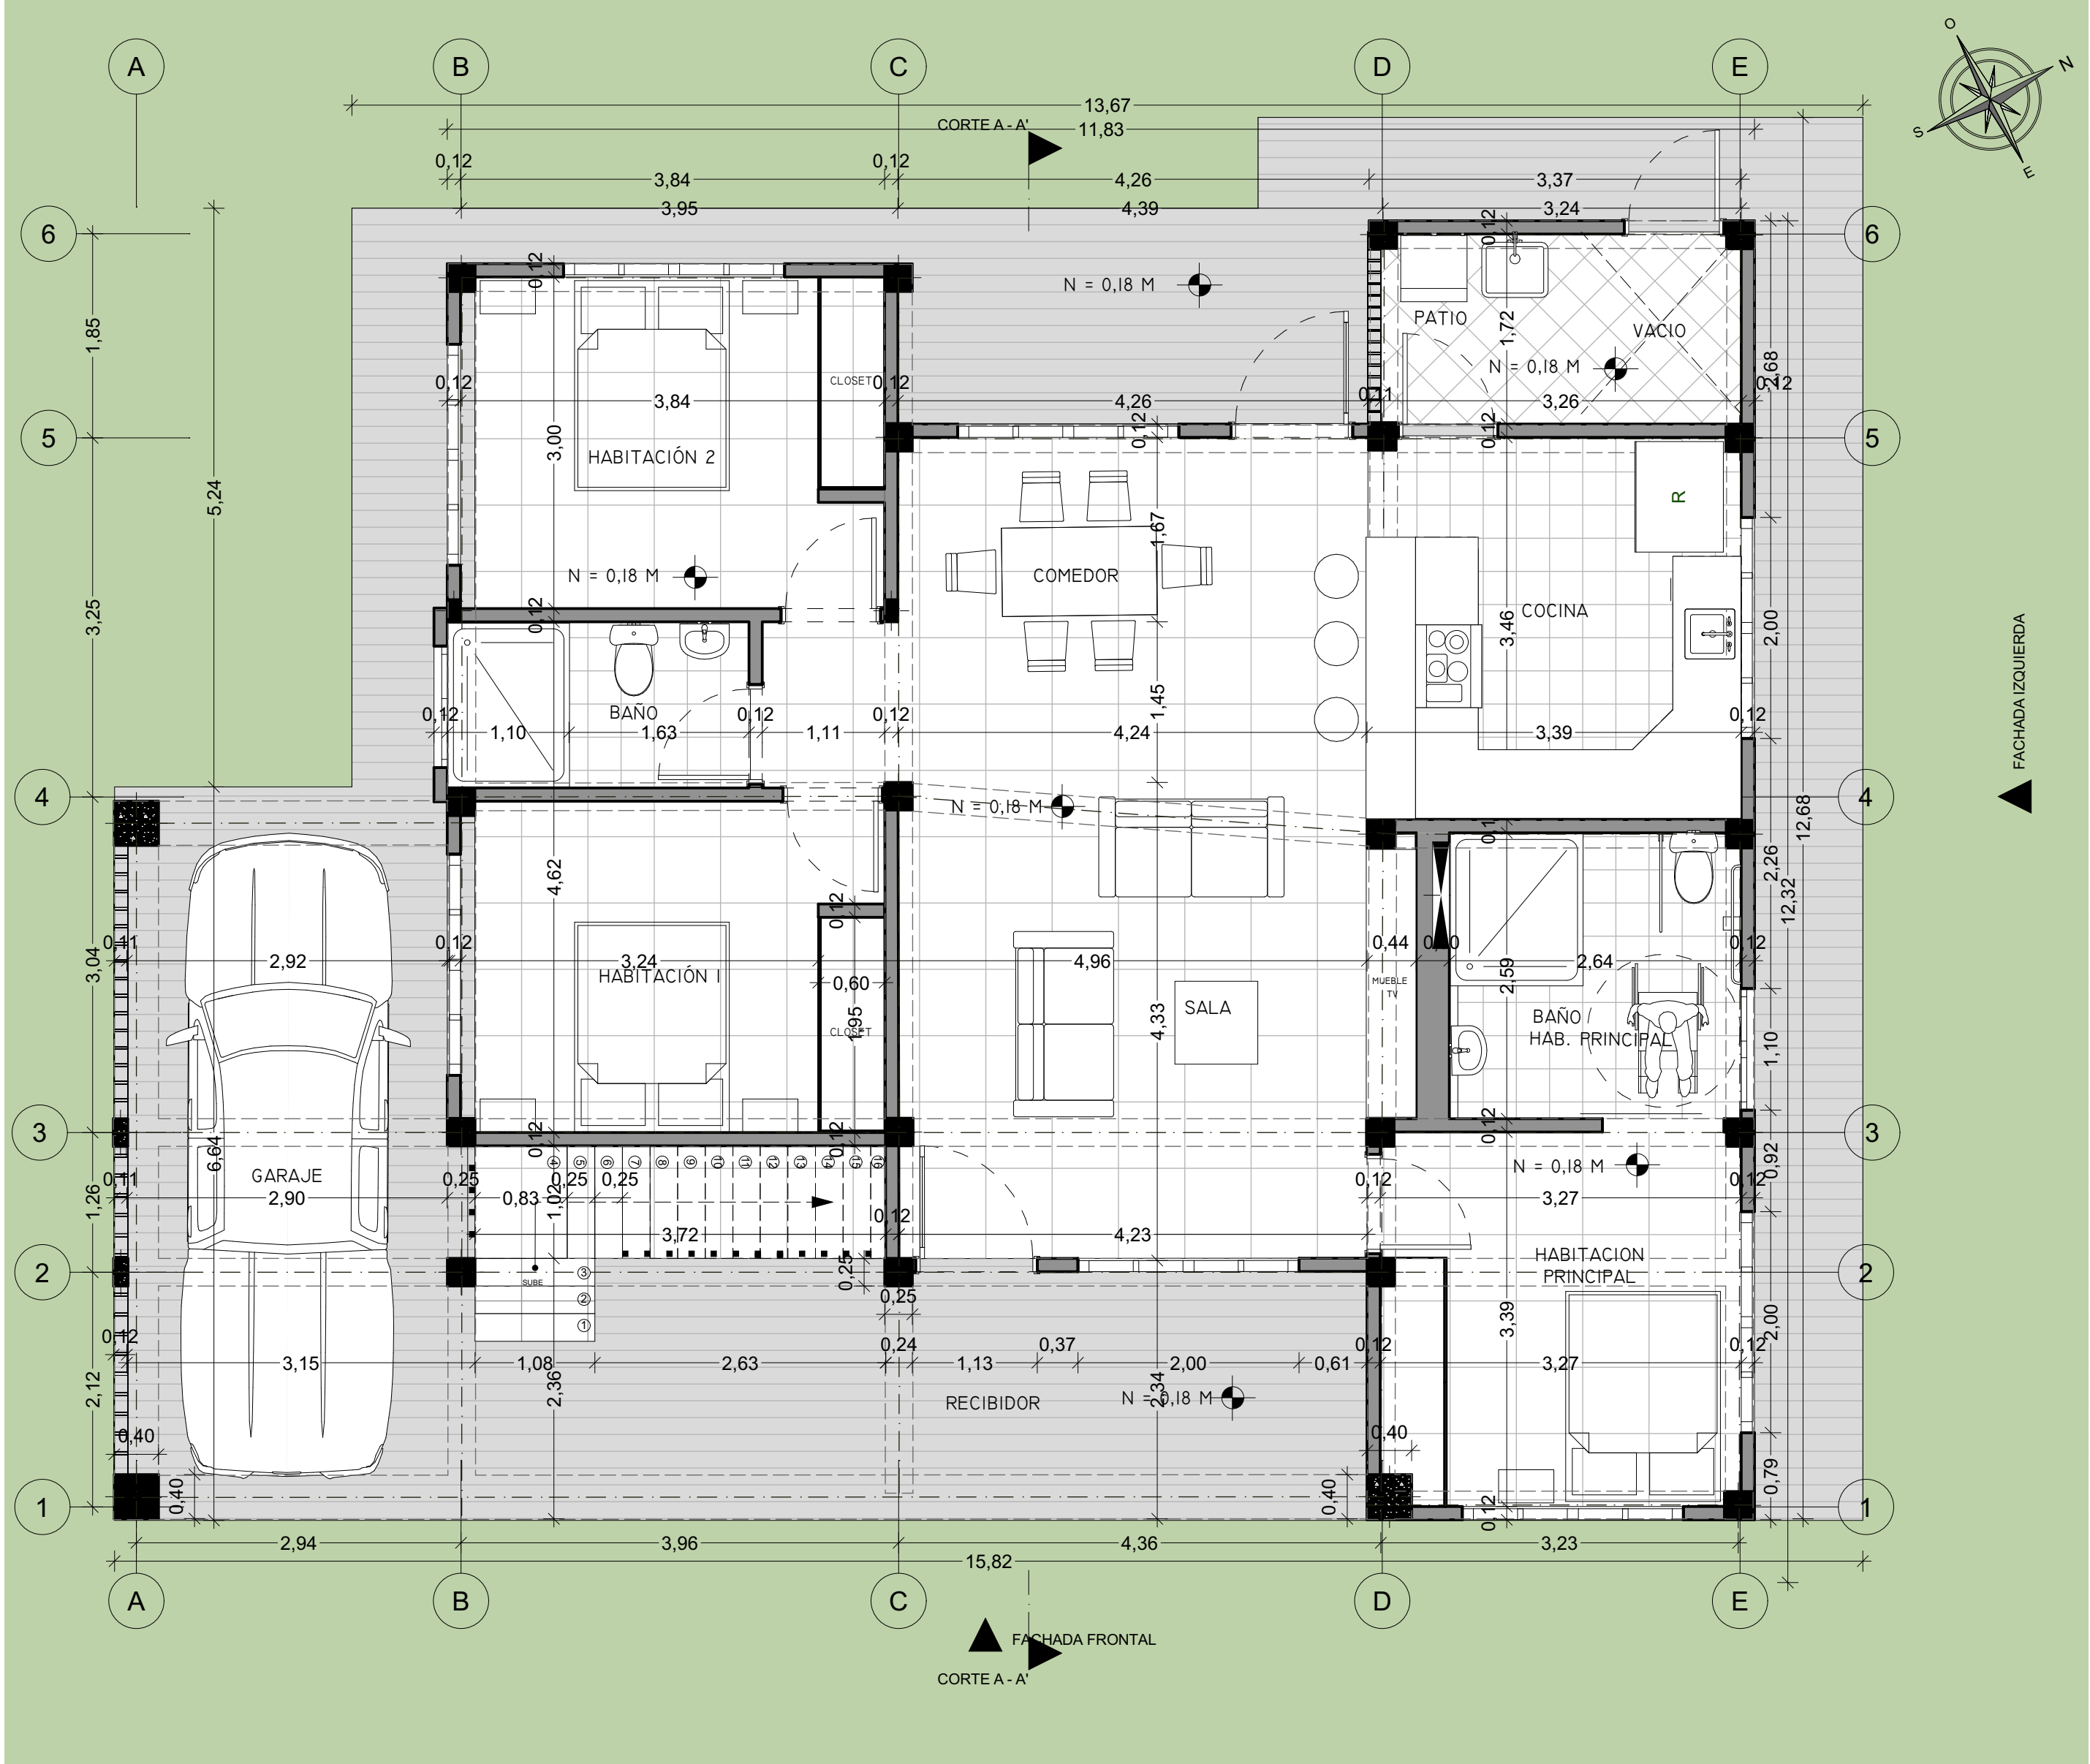

PLANTA DE CUBIERTA

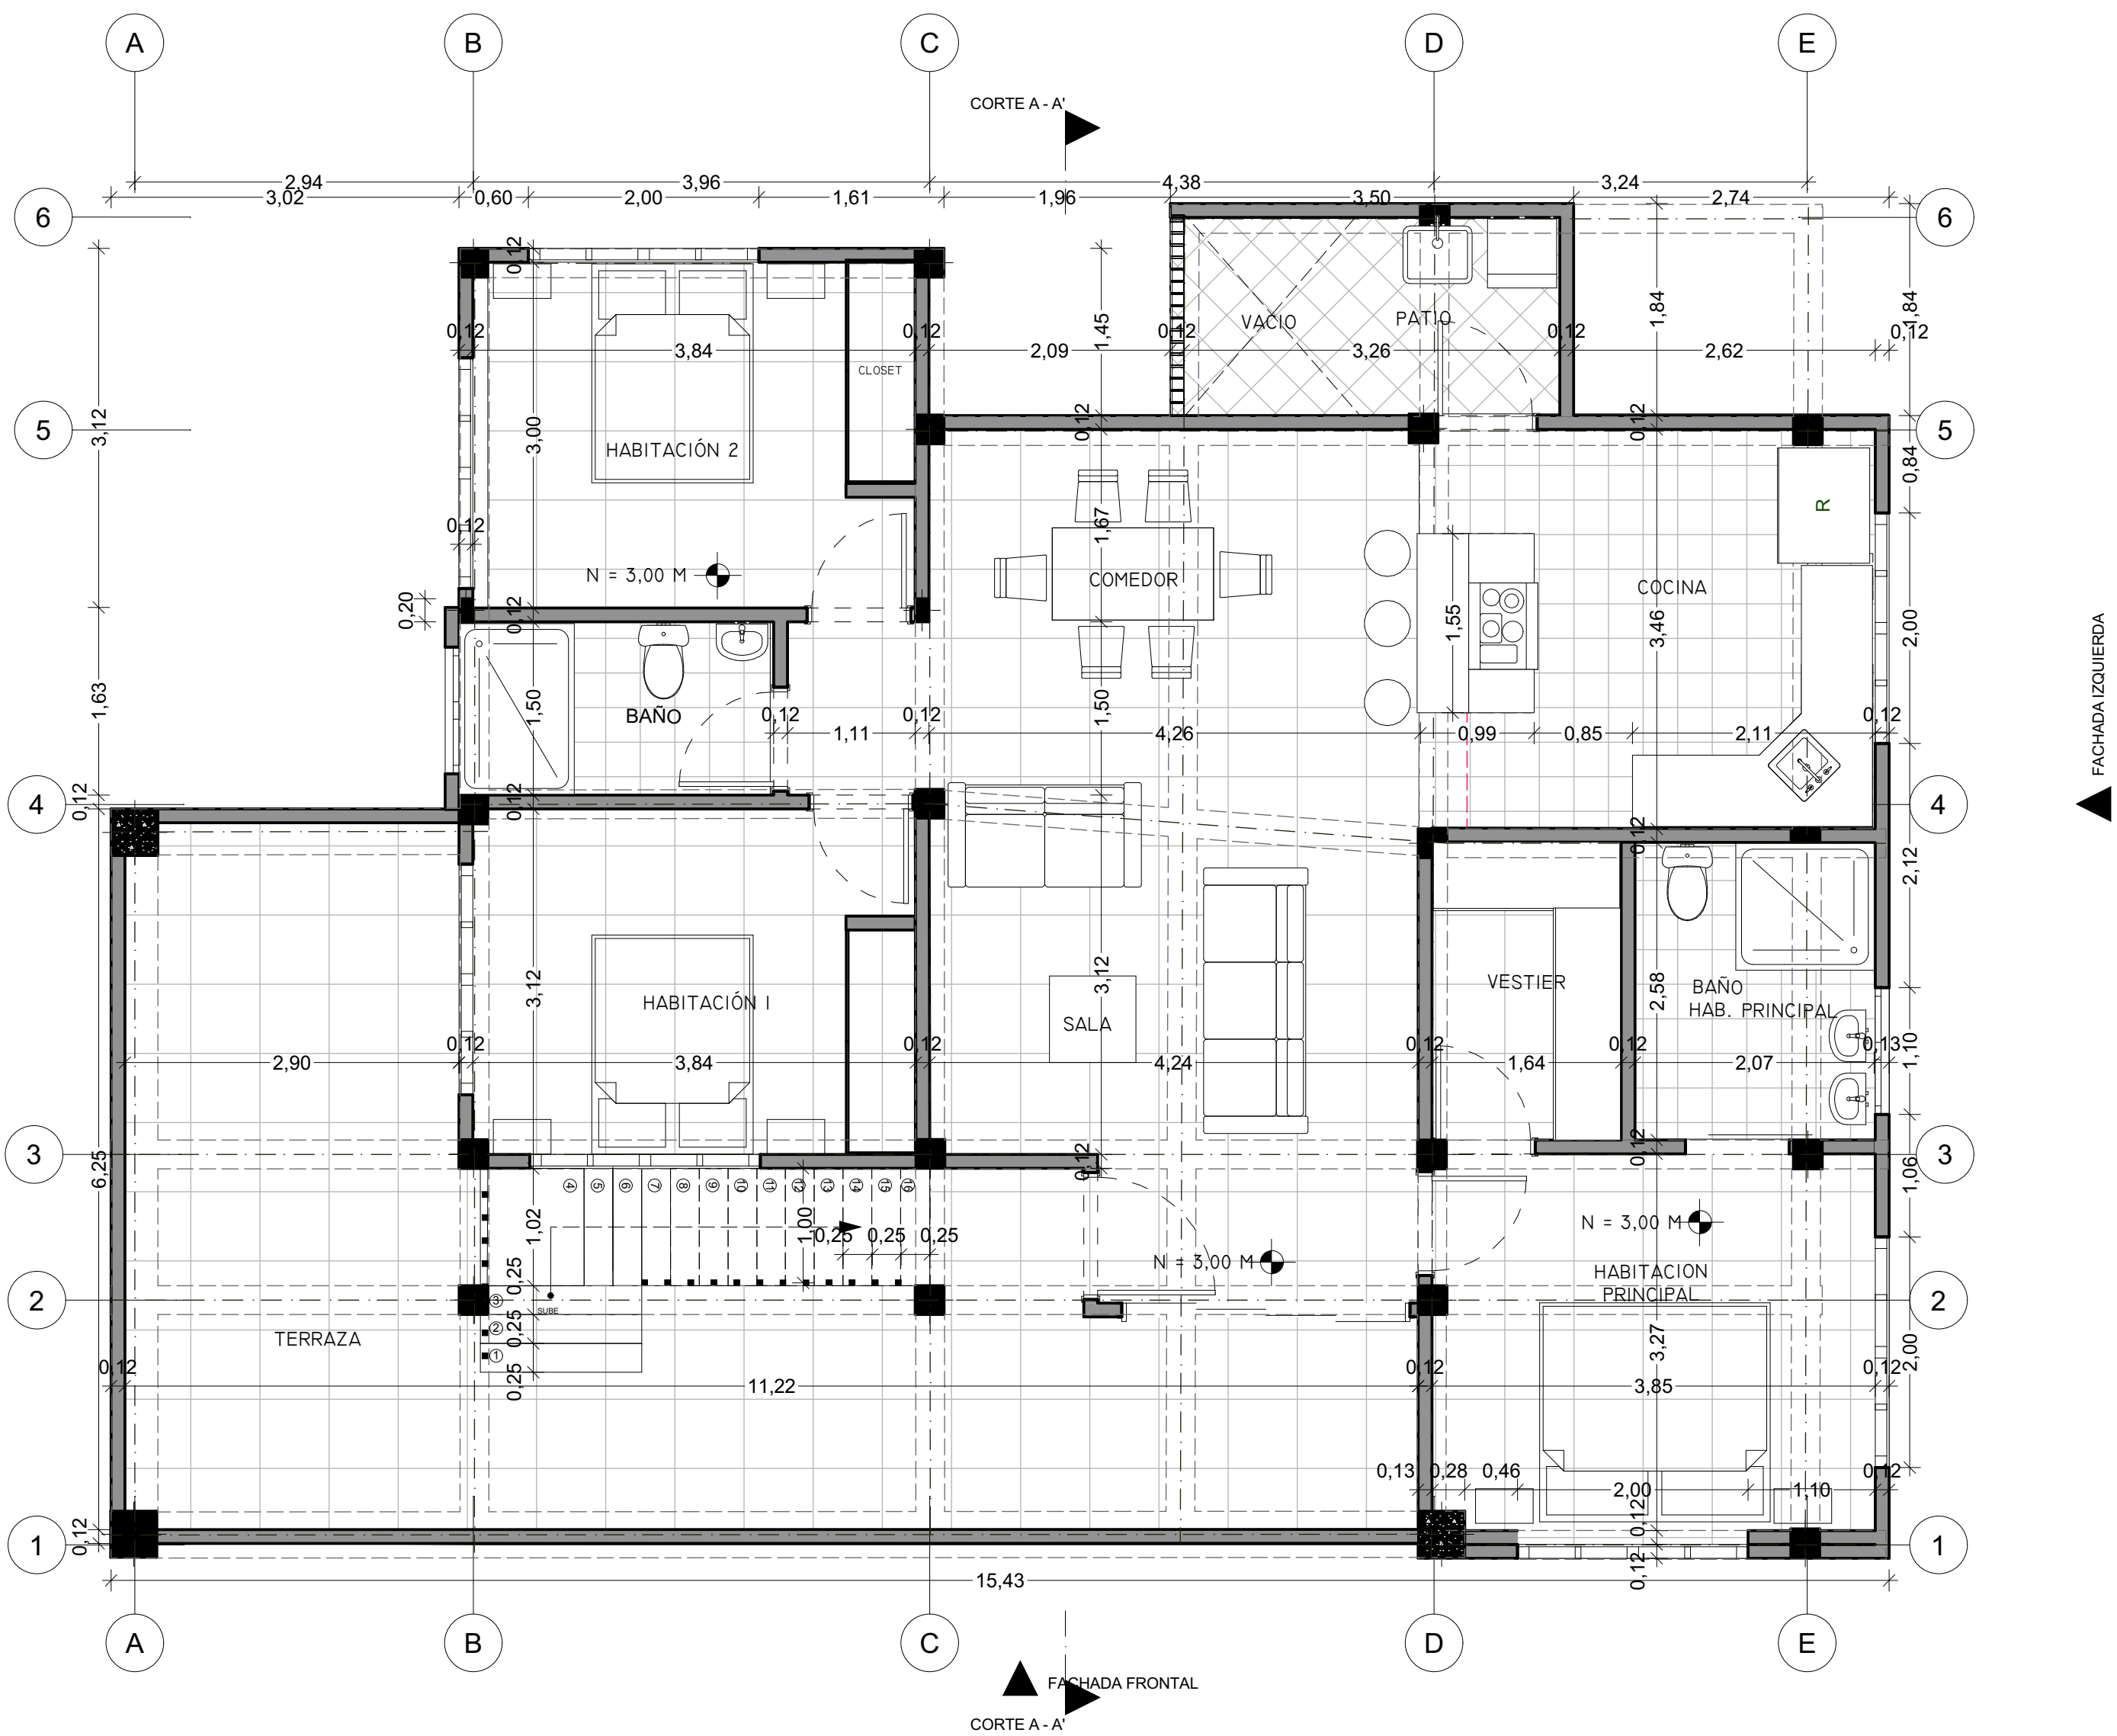


LOCALIZACIÓN

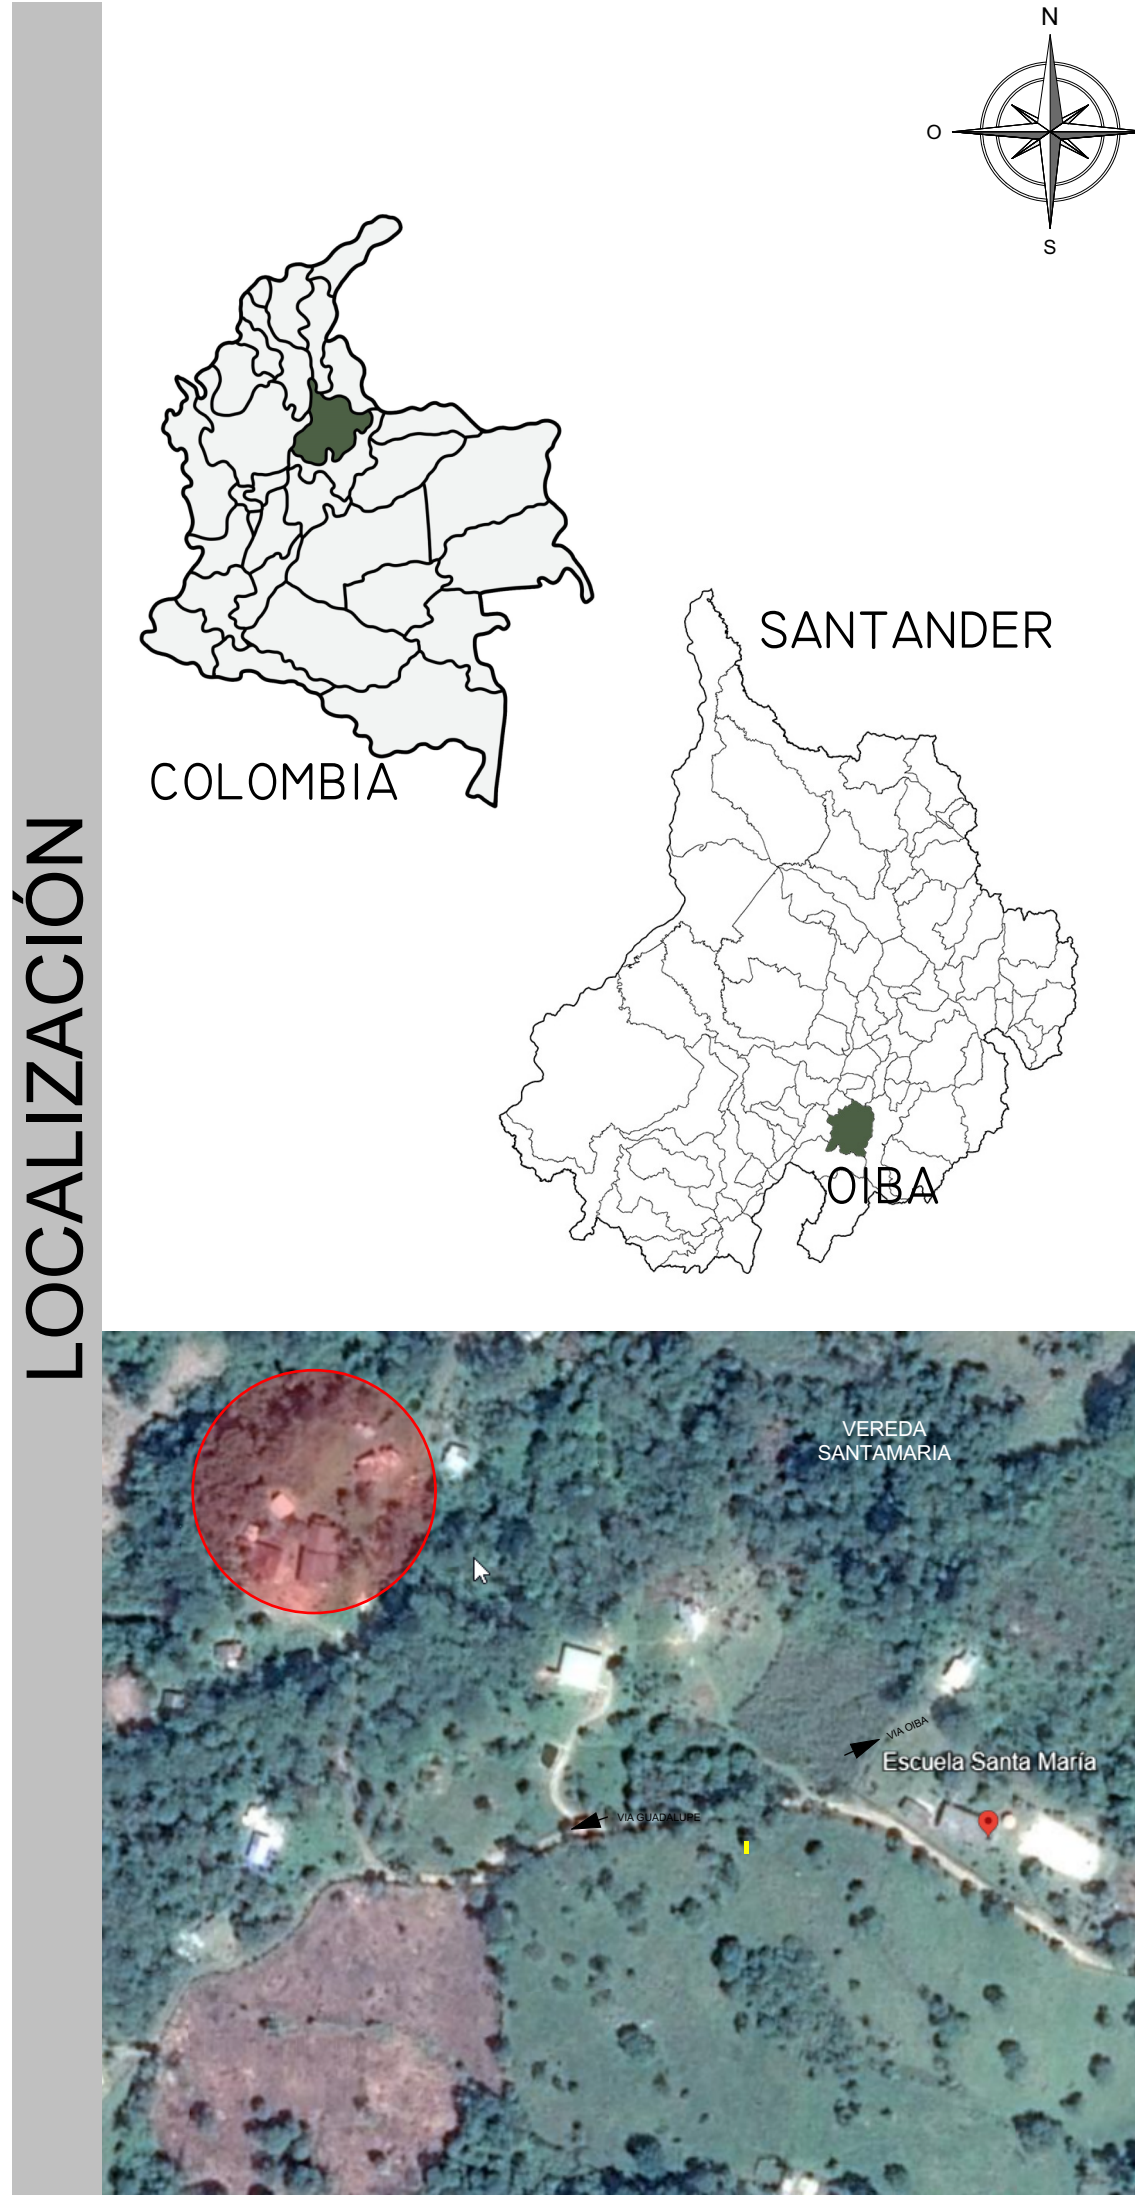


CUADRO DE AREAS


ÁREA CONSTRUIDA PISO 1	146 M2
ÁREA CONSTRUIDA PISO 2	112 M2

FACHADA PRINCIPAL

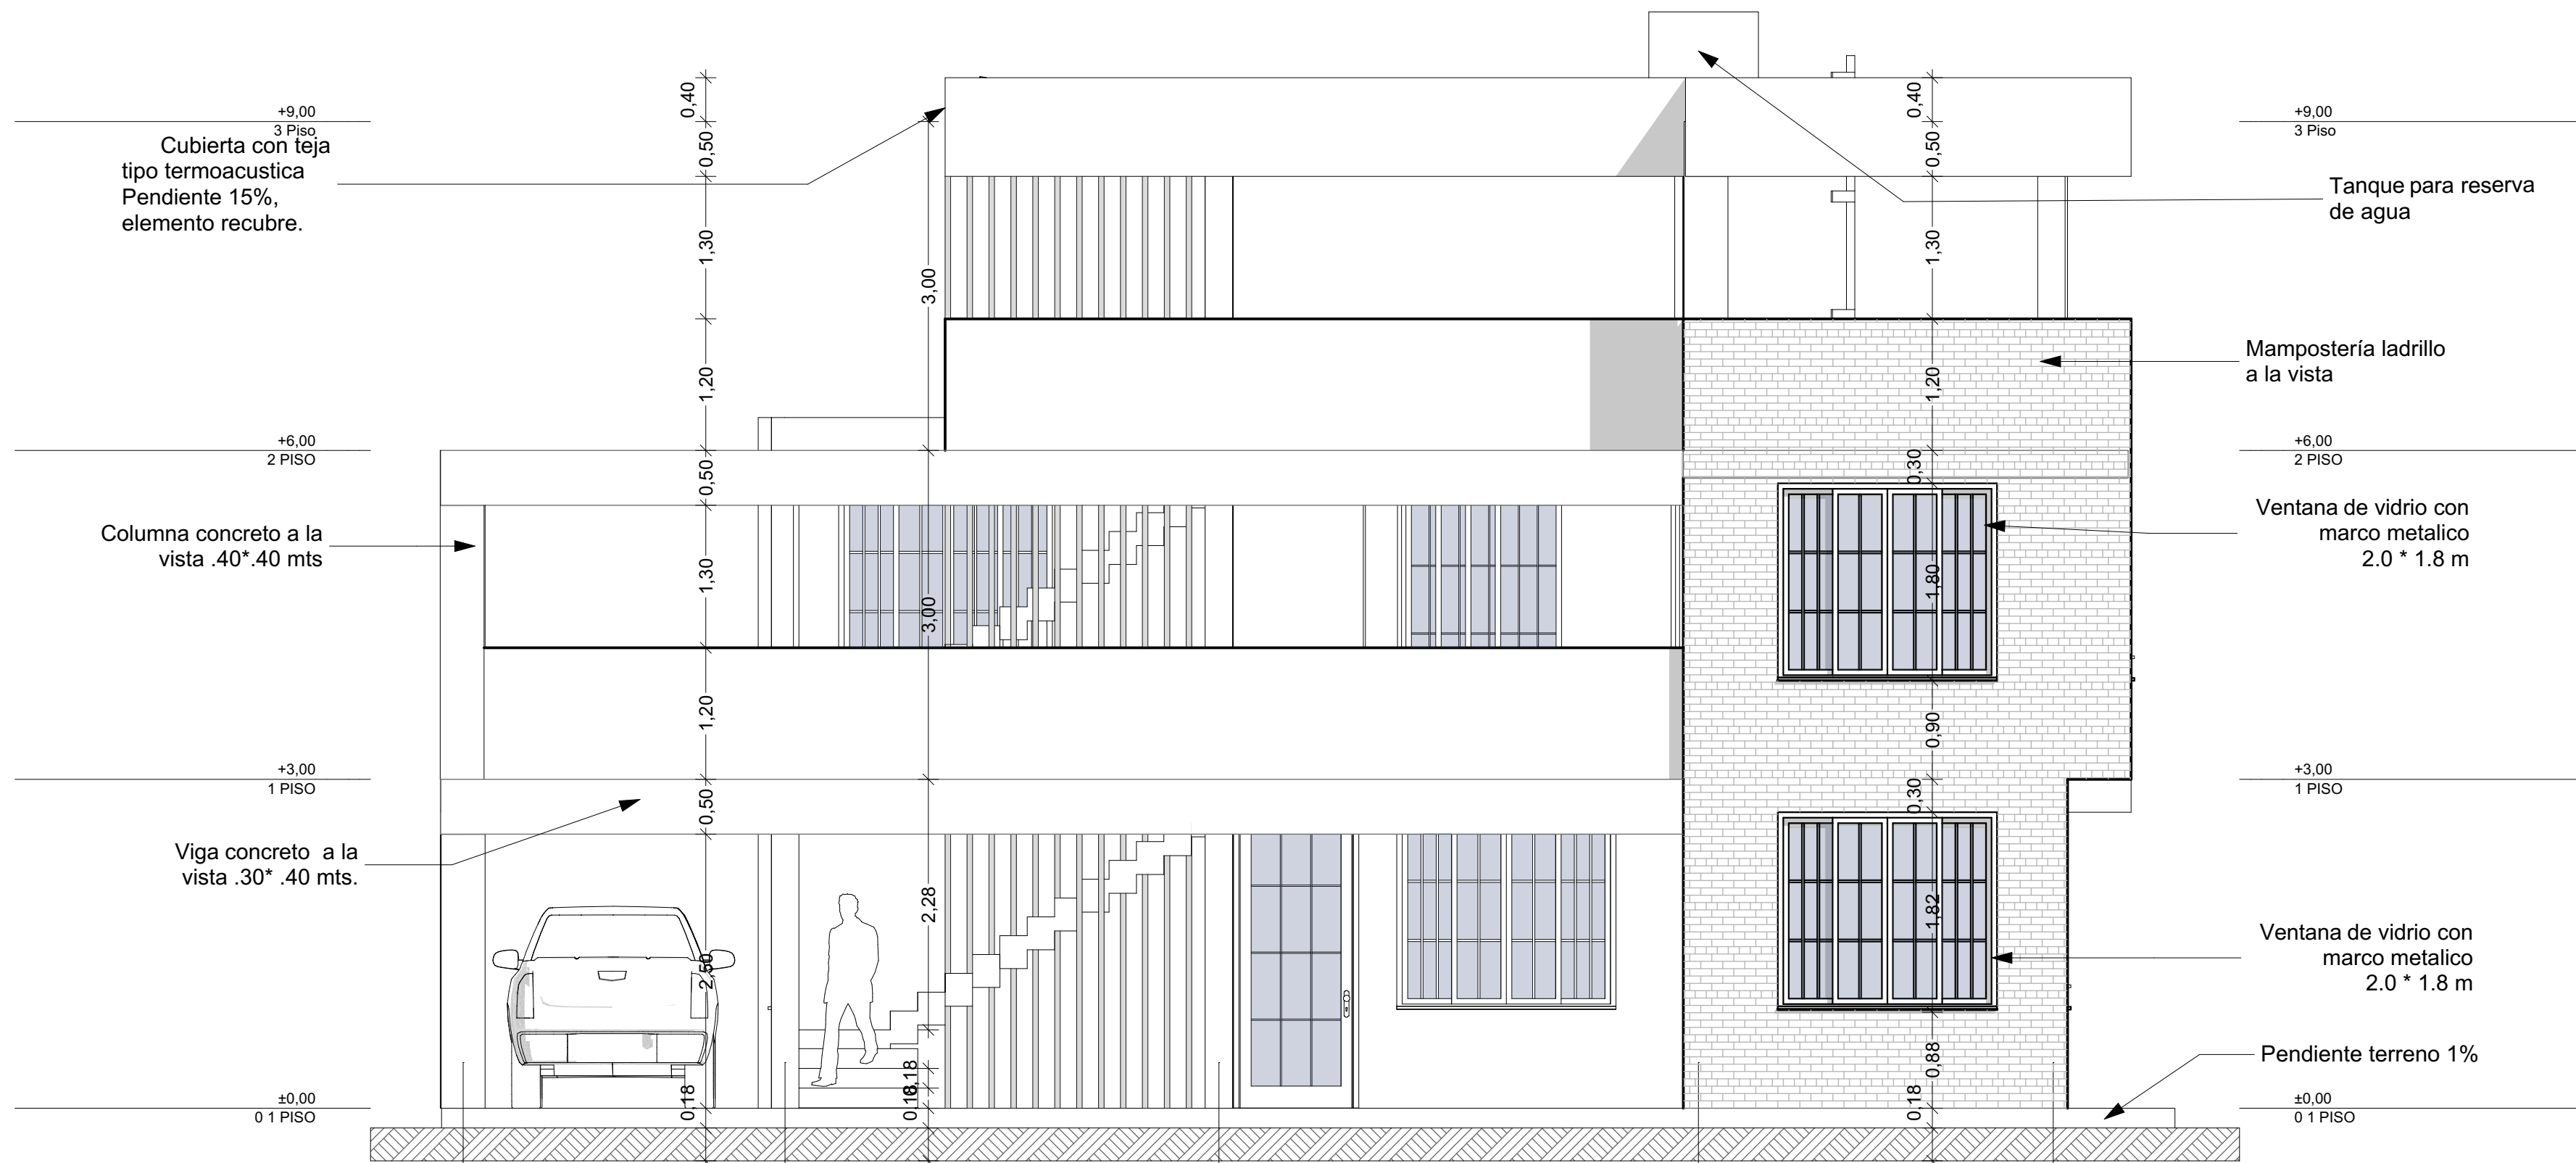

FACHADA LATERAL DERECHA

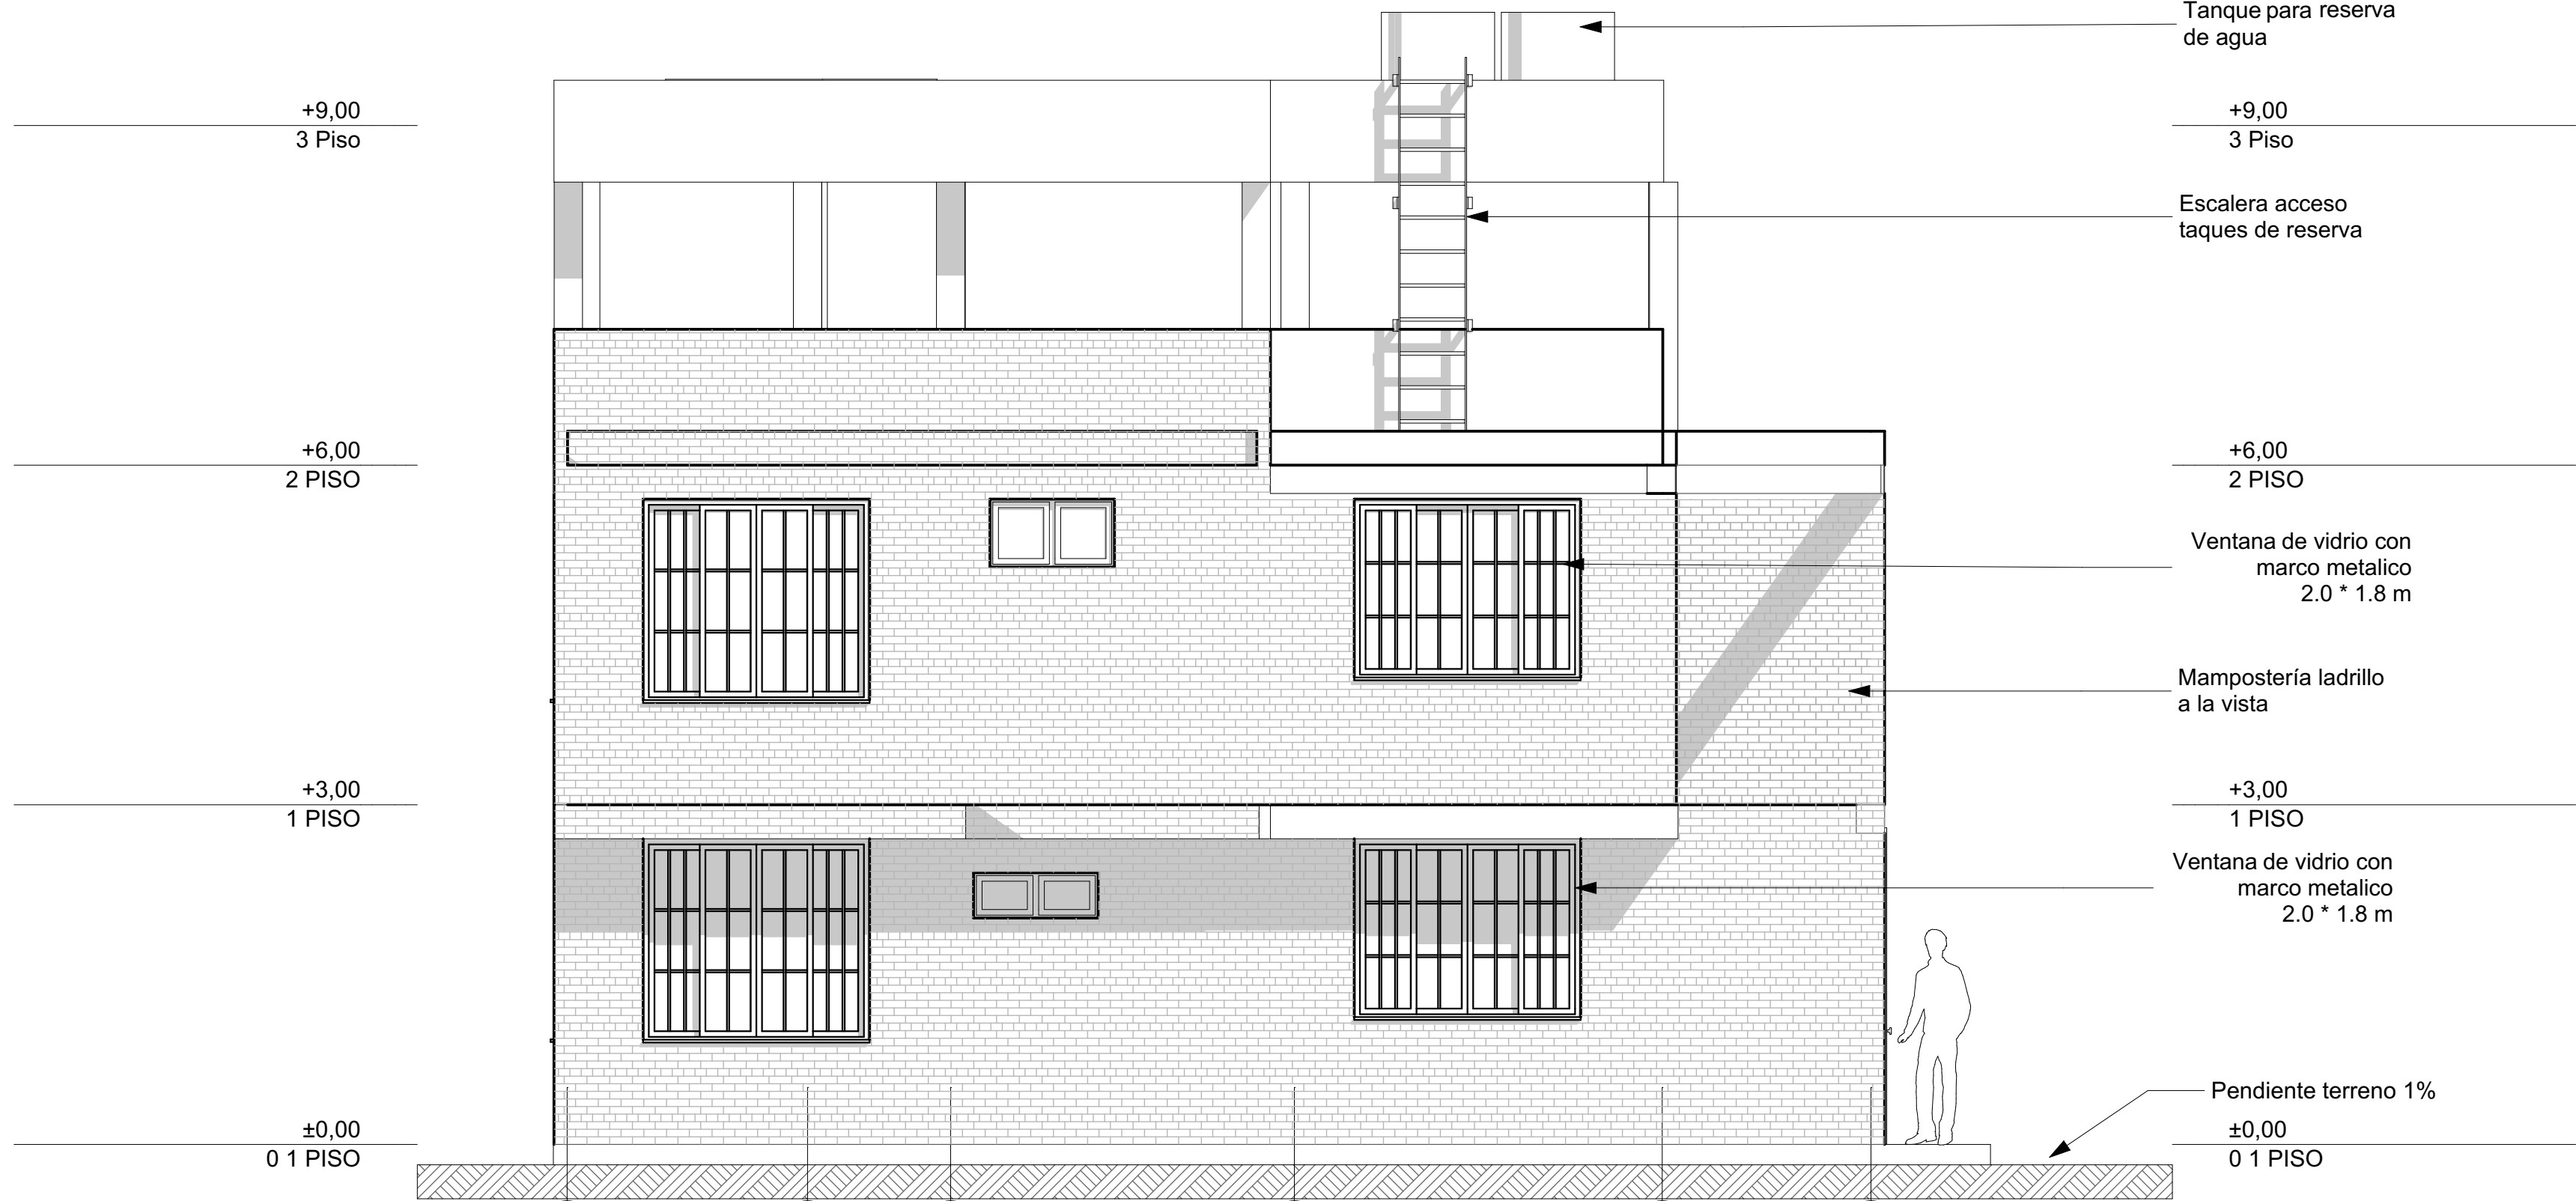

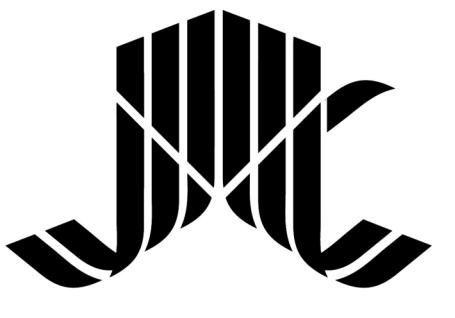PROPIETARIOS: JUAN RIVAS	DISEÑO:  JESSICA VIVIANA RANGEL E. ARQUITECTA - DISEÑADORA DE ESPACIOS INTERIORES TEL: 317 29 48 49 - E-MAIL: RANGELJESSICA@GMAIL.COM	APROBÓ: 	CONTIENE: PLANTAS ARQUITECTÓNICAS, FACHADA , CUADRO DE ÁREAS Y LOCALIZACIÓN	FECHA: DICIEMBRE 2024	OBSERVACIONES: RECOMENDACIONES ESTRUCTURALES -TODAS LAS COLUMNAS VAN DE 25X25 EXCEPTO LAS GRANDES ESAS VAN DE 40 X40 Y COLUMNETAS 0.20 *0.12 MS CON 4 VARILLAS DE 3/8 -FLEJES CON SEPARACION EN LOS EXTREMOS 0.10 MT LO DEMAS CADA 0.20MT, SEGUN LO INDICA LA TABLA. -EL REFUERZO DE LAS COLUMNAS DE 25 SON 8 VARILLAS 1/2 Y LAS DE 40 SON 12 DE 1/2 O 8 DE 5/8 -LAS VIGAS SON DE 0.25*0.30 CON REFUERZO DE 6 VARILLAS DE 1/2 -LAS VIGAS DE AMARRE 0.40*0.50 CON 10 VARILLAS DE 3/4 O DE 8 DE PULG ADA DE PARA LAS COLUMNAS DE .40 *0.40 -ZAPATAS CENTRALES DE 1.20 *1.20 LAS DEMAS DE 1.0 * 1.0, CON VARILLAS D E MEDIA CADA 15 CM Y EL RECUBRIMIENTO DEBE SER DE 8CM MINIMO.
DIRECCIÓN: VEREDA SANTAMARIA OIBA, SANTANDER			TRAMITE: LICENCIA DE CONSTRUCCIÓN NUEVA	ESCALA: 1:50	PLANO: I DE I