



PLANTA TERCER PISO

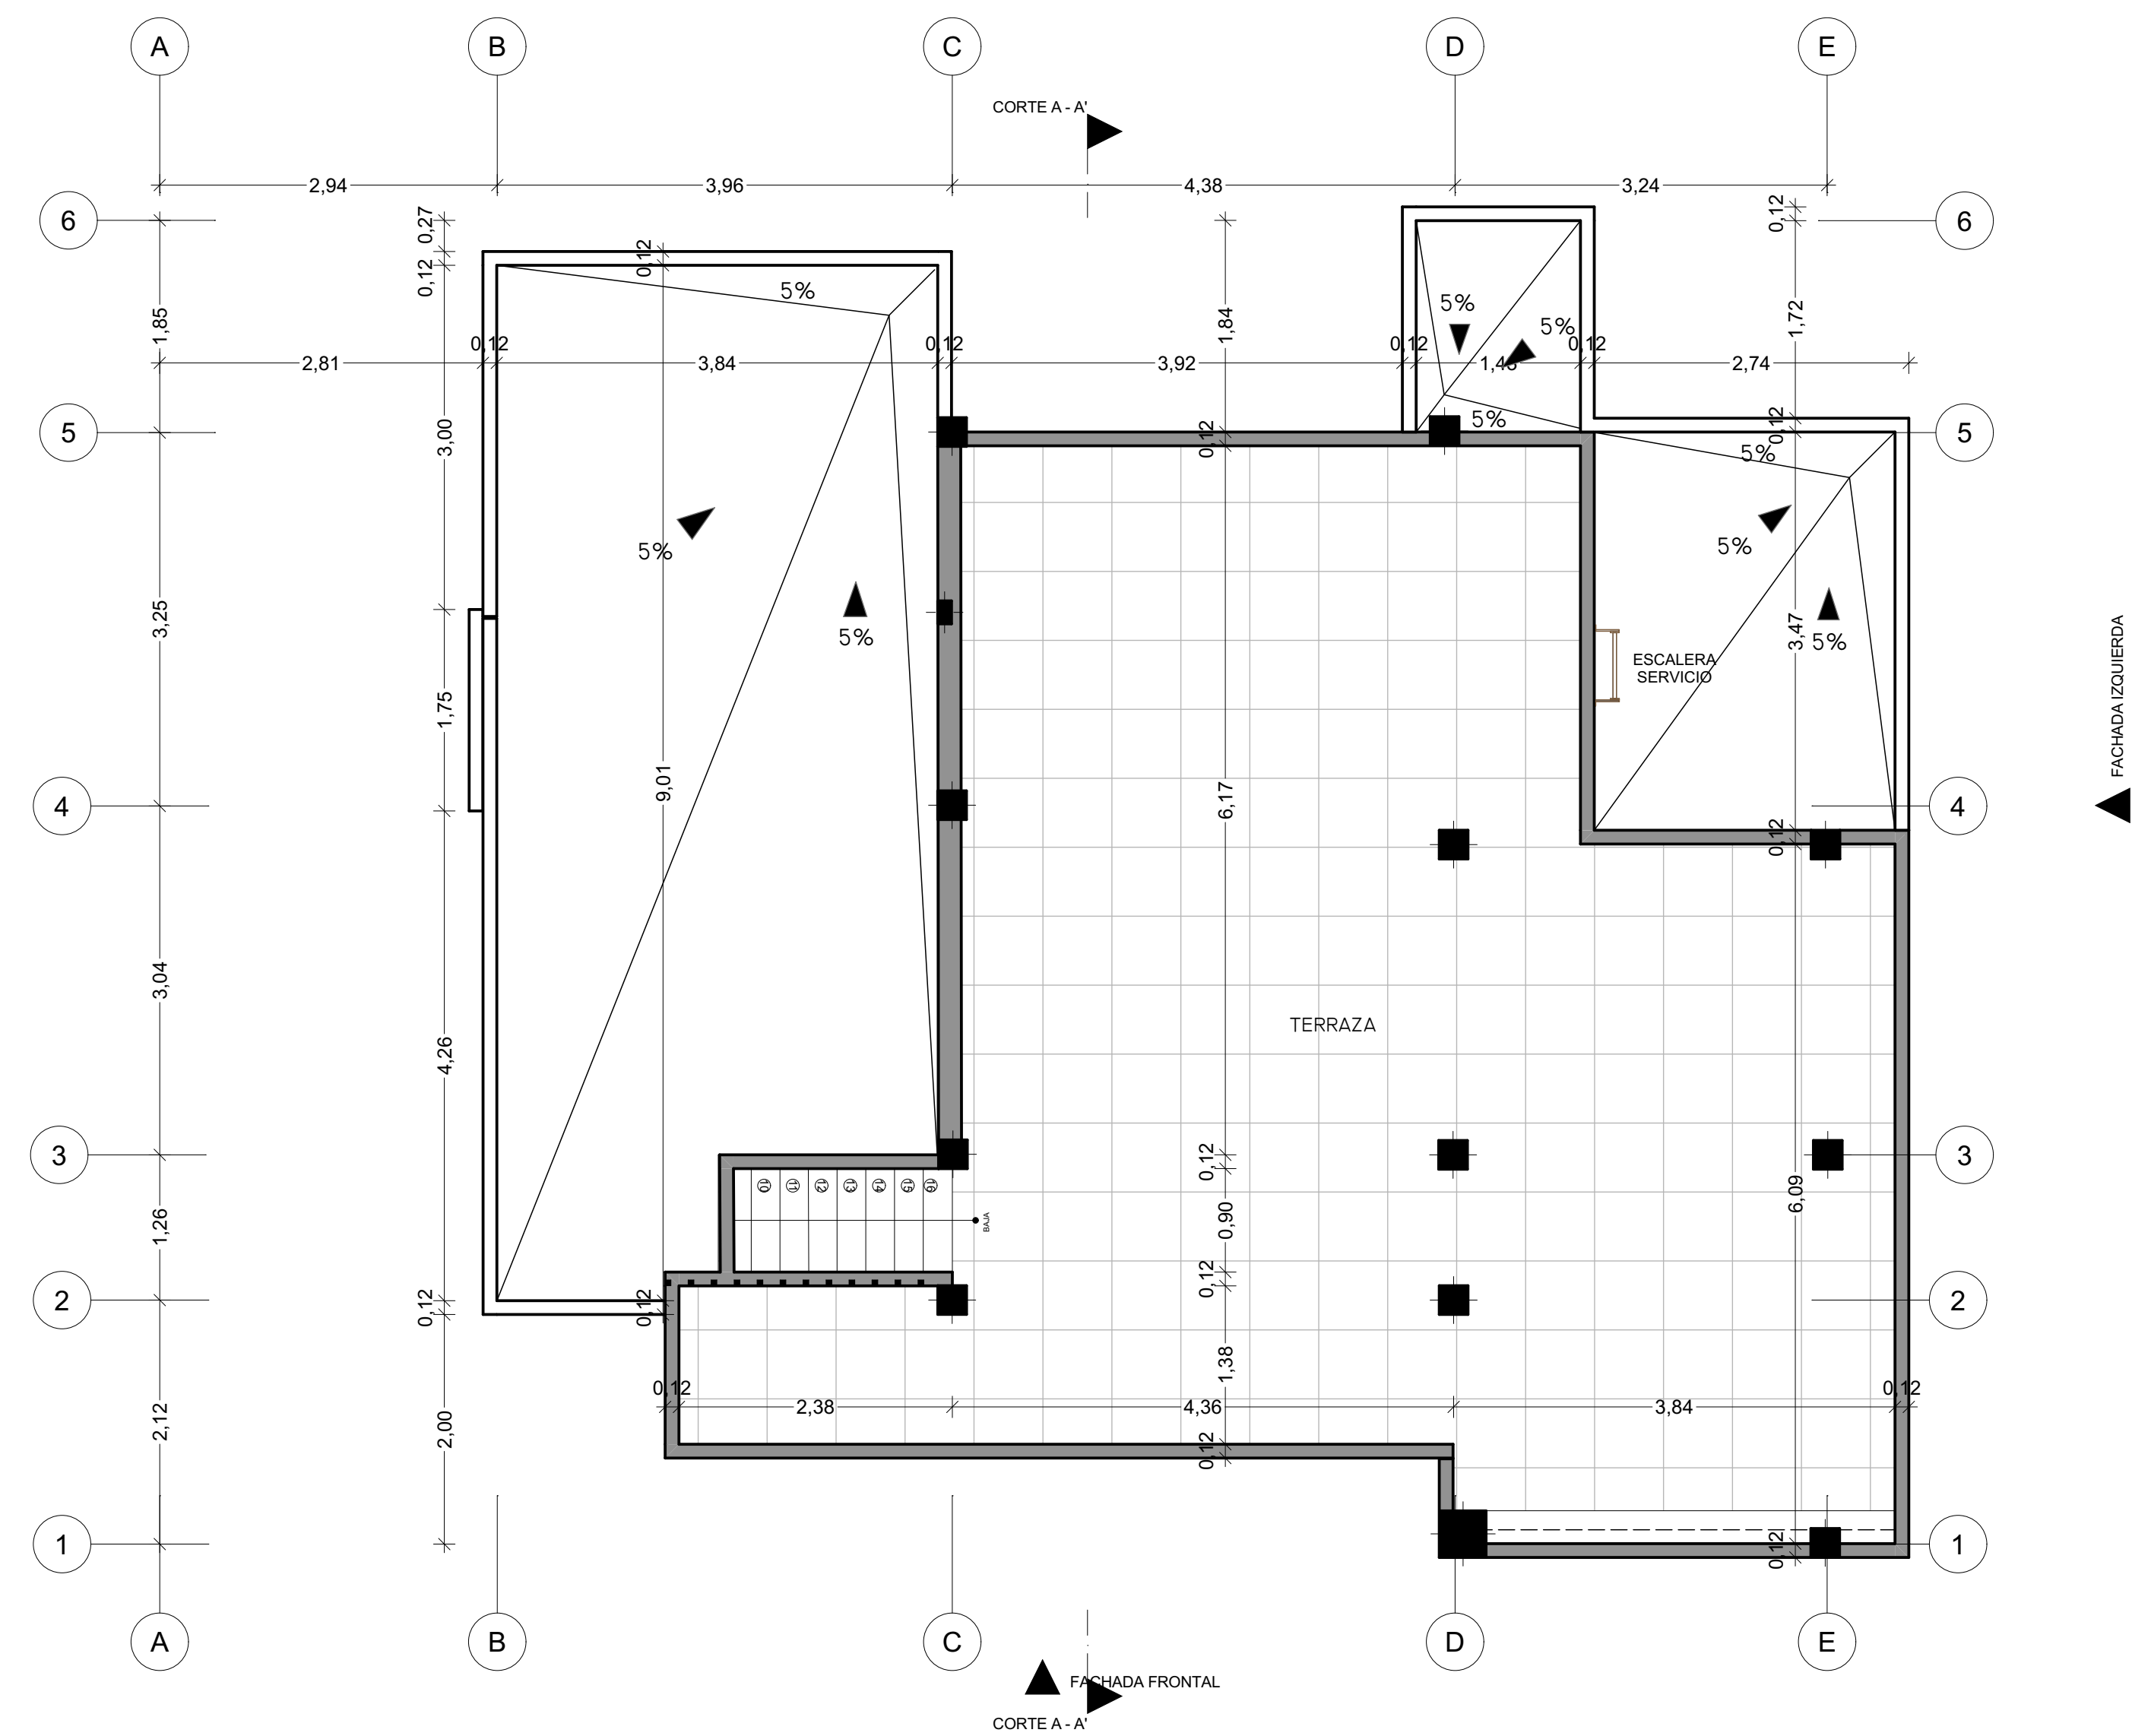


PLANTA DE CUBIERTA

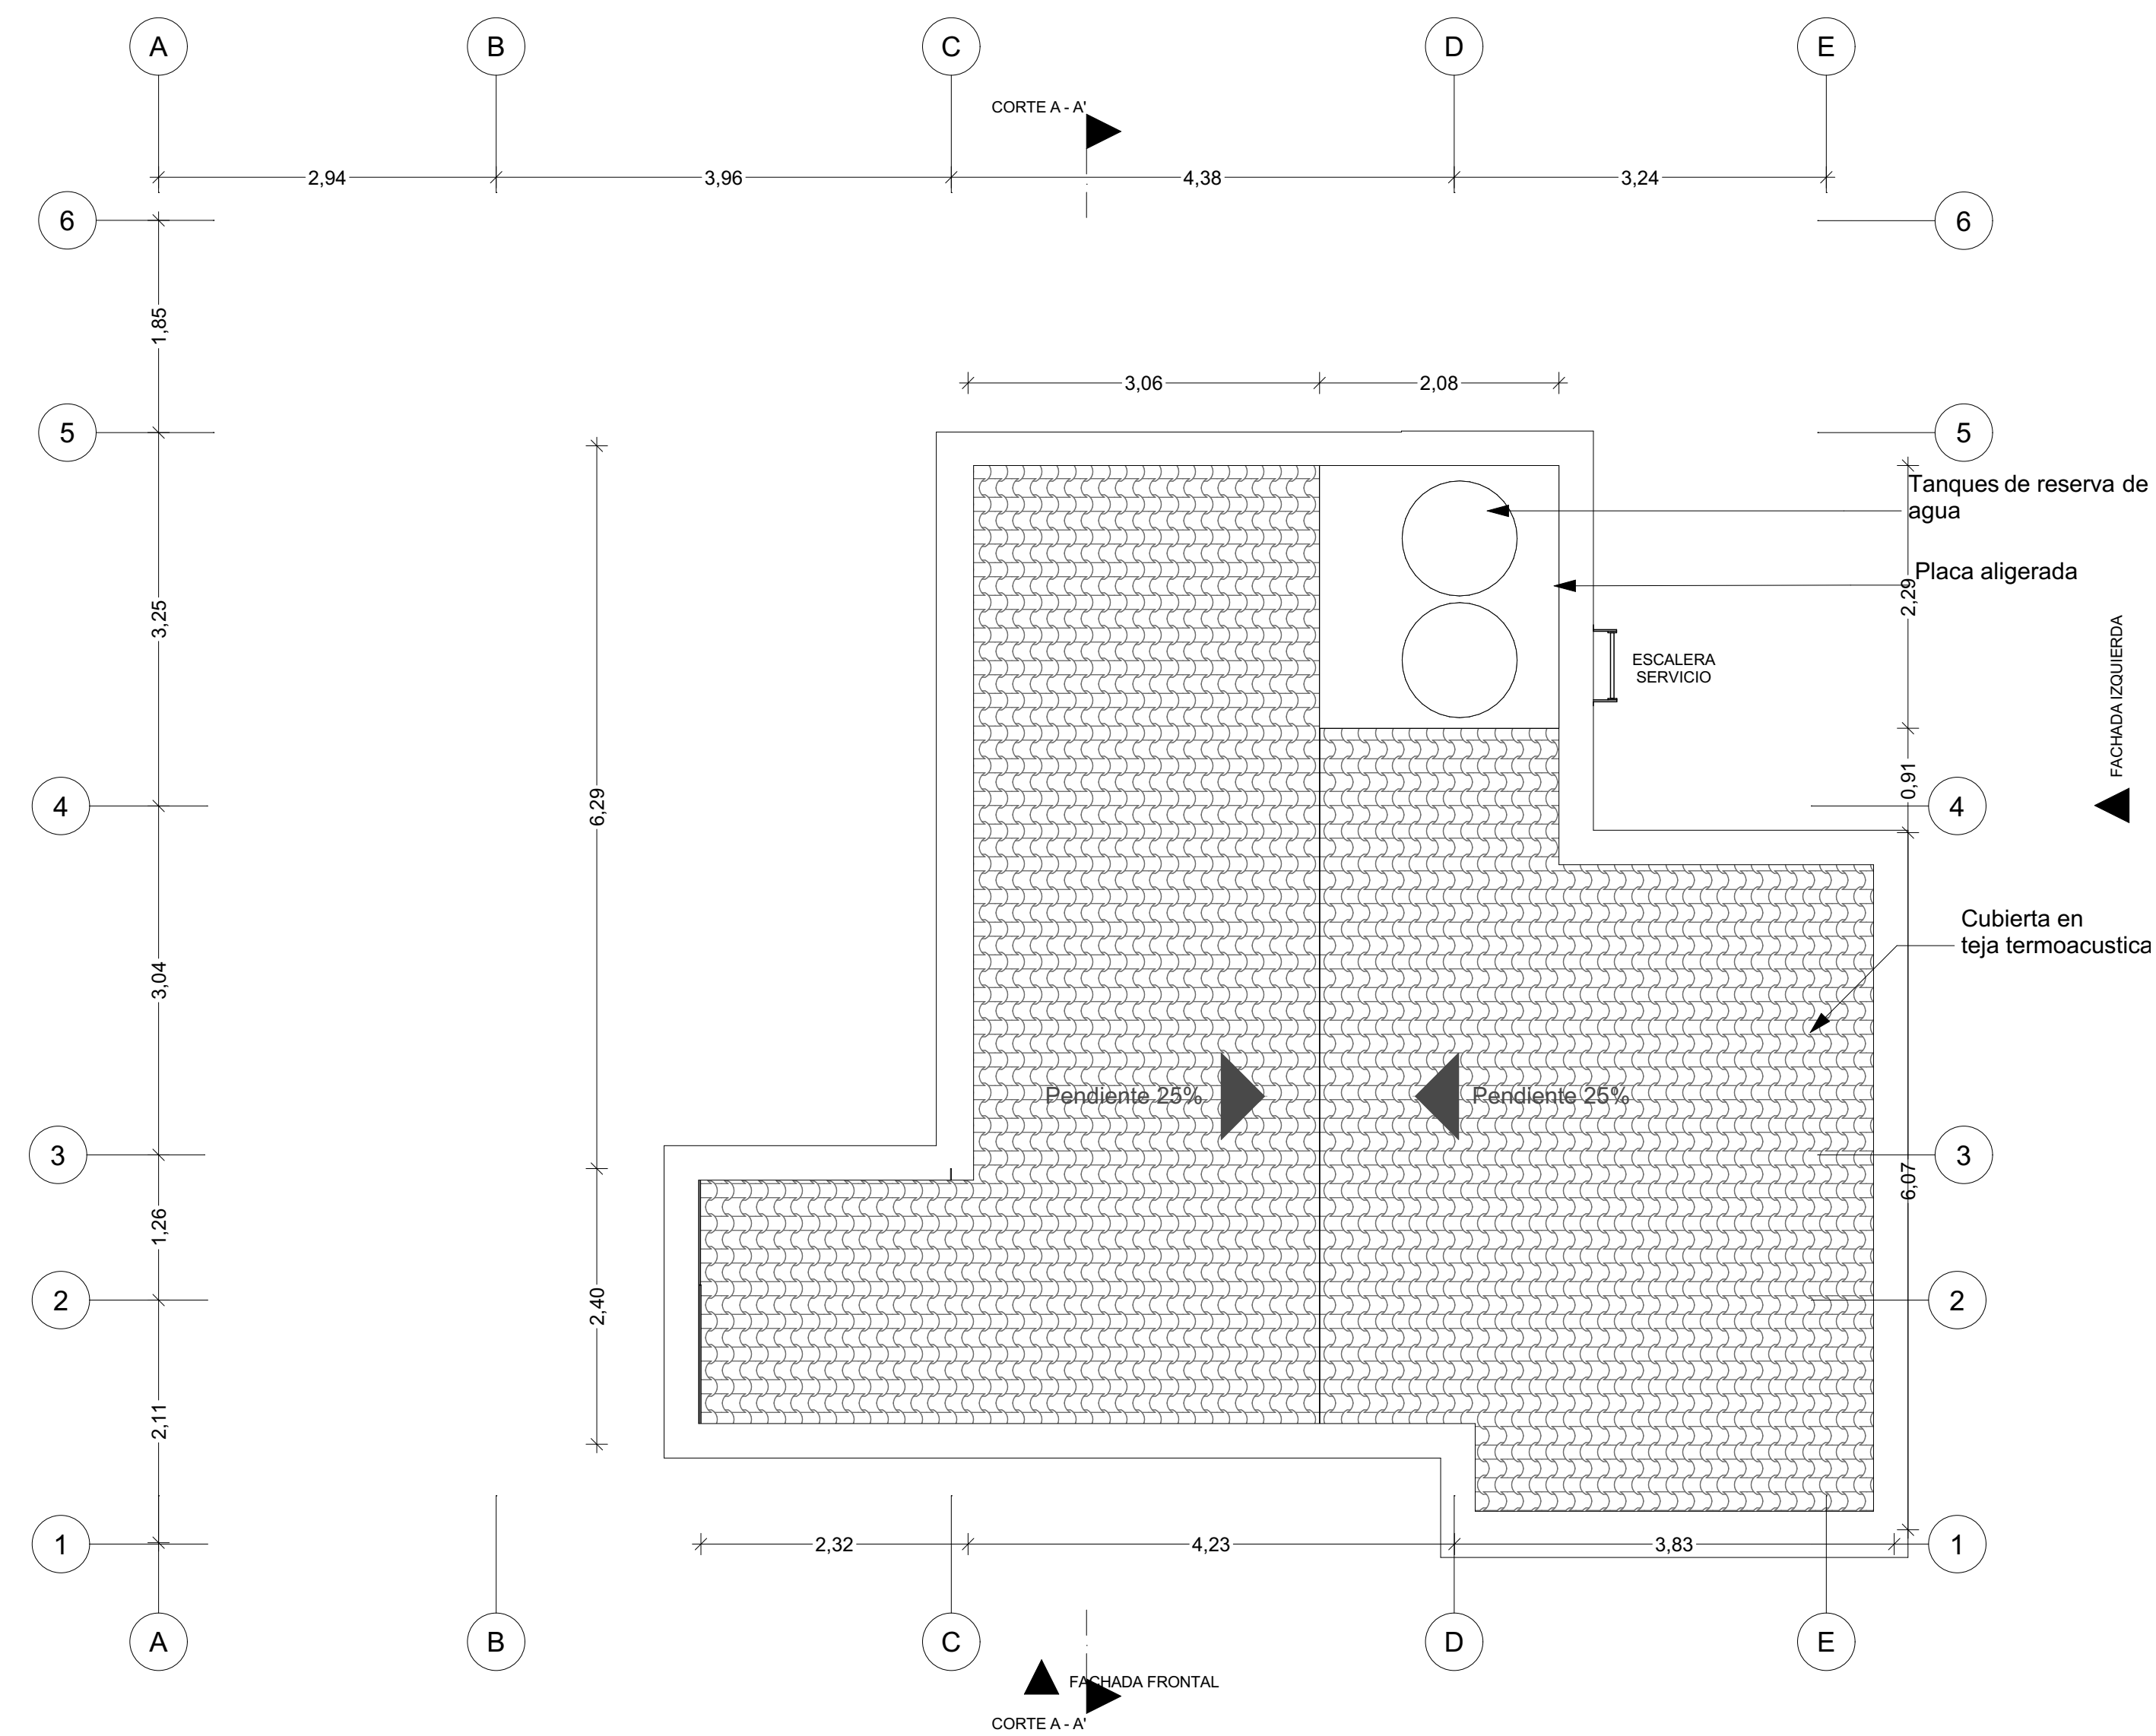


PROPIEDADES DE LAS BARRAS DE ACERO						
BARRA No	DIAMETRO	DIAMETRO EN mm	AREA c2	PERIMETRO EN mm	PESO KG/ml	TRASLAPE EN cm
2	1/4"	6.4 mm	0.32	19.8 mm	0.25	30 cm
3	3/8"	9.5 mm	0.71	29.8 mm	0.56	50 cm
4	1/2"	12.7 mm	1.19	39.9 mm	0.99	70 cm
5	5/8"	15.9 mm	2	49.9 mm	1.55	80 cm
6	3/4"	19.1 mm	2.84	59.8 mm	2.24	85 cm
7	7/8"	22.2 mm	3.87	69.8 mm	3.04	100 cm
8	1"	25.4	5.1	79.8 mm	3.97	110 cm

FACHADA POSTERIOR

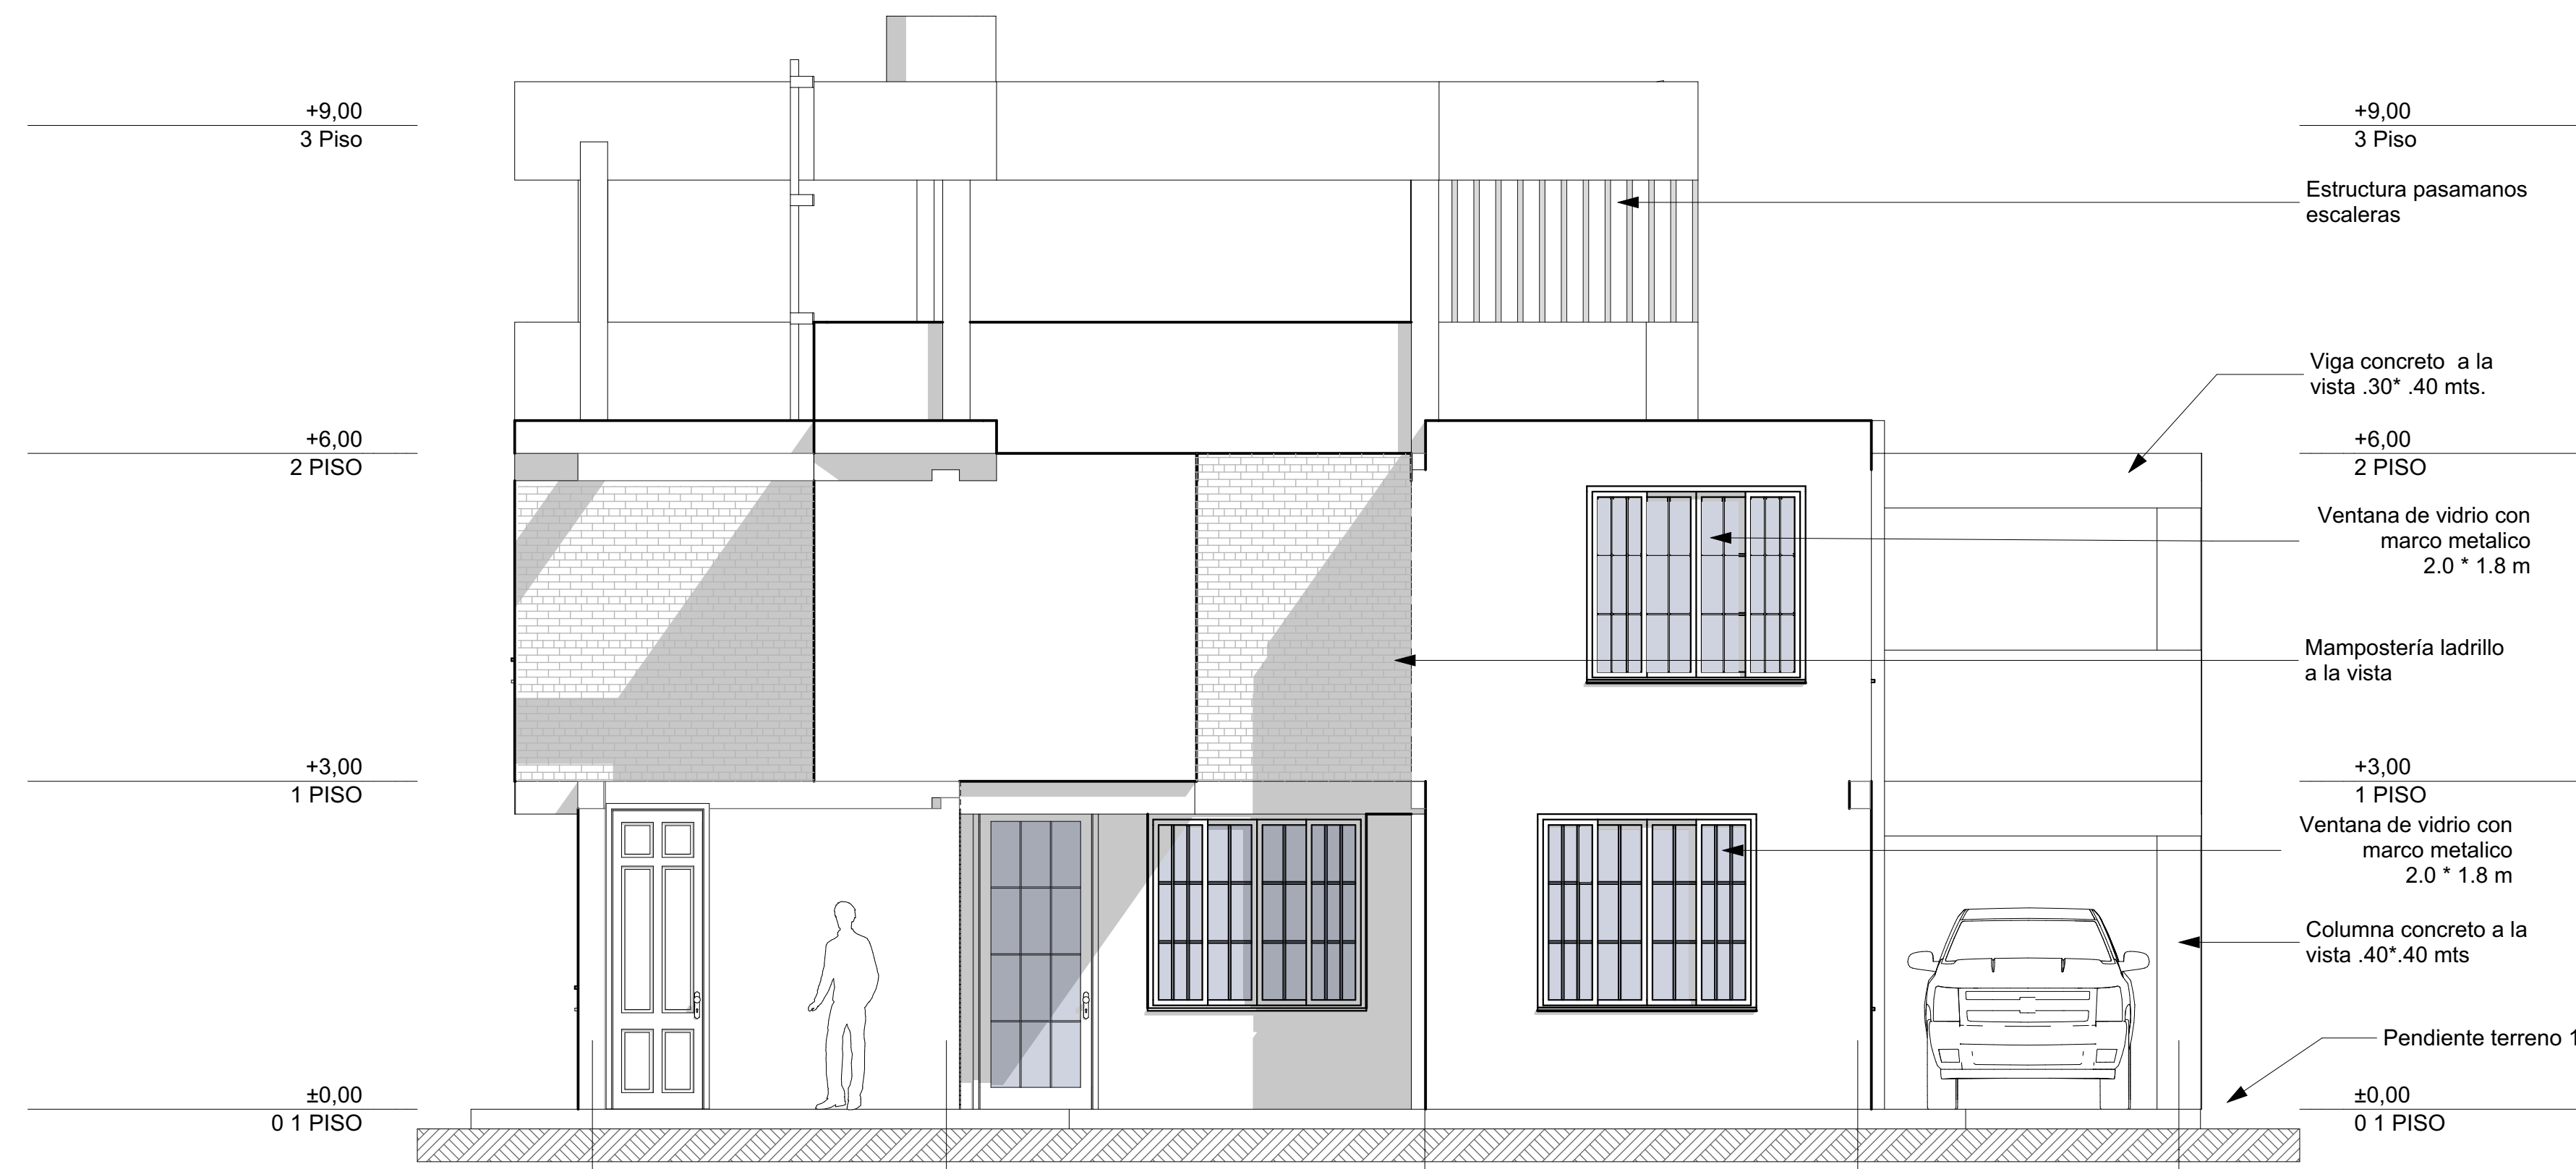

FACHADA LATERAL DERECHA

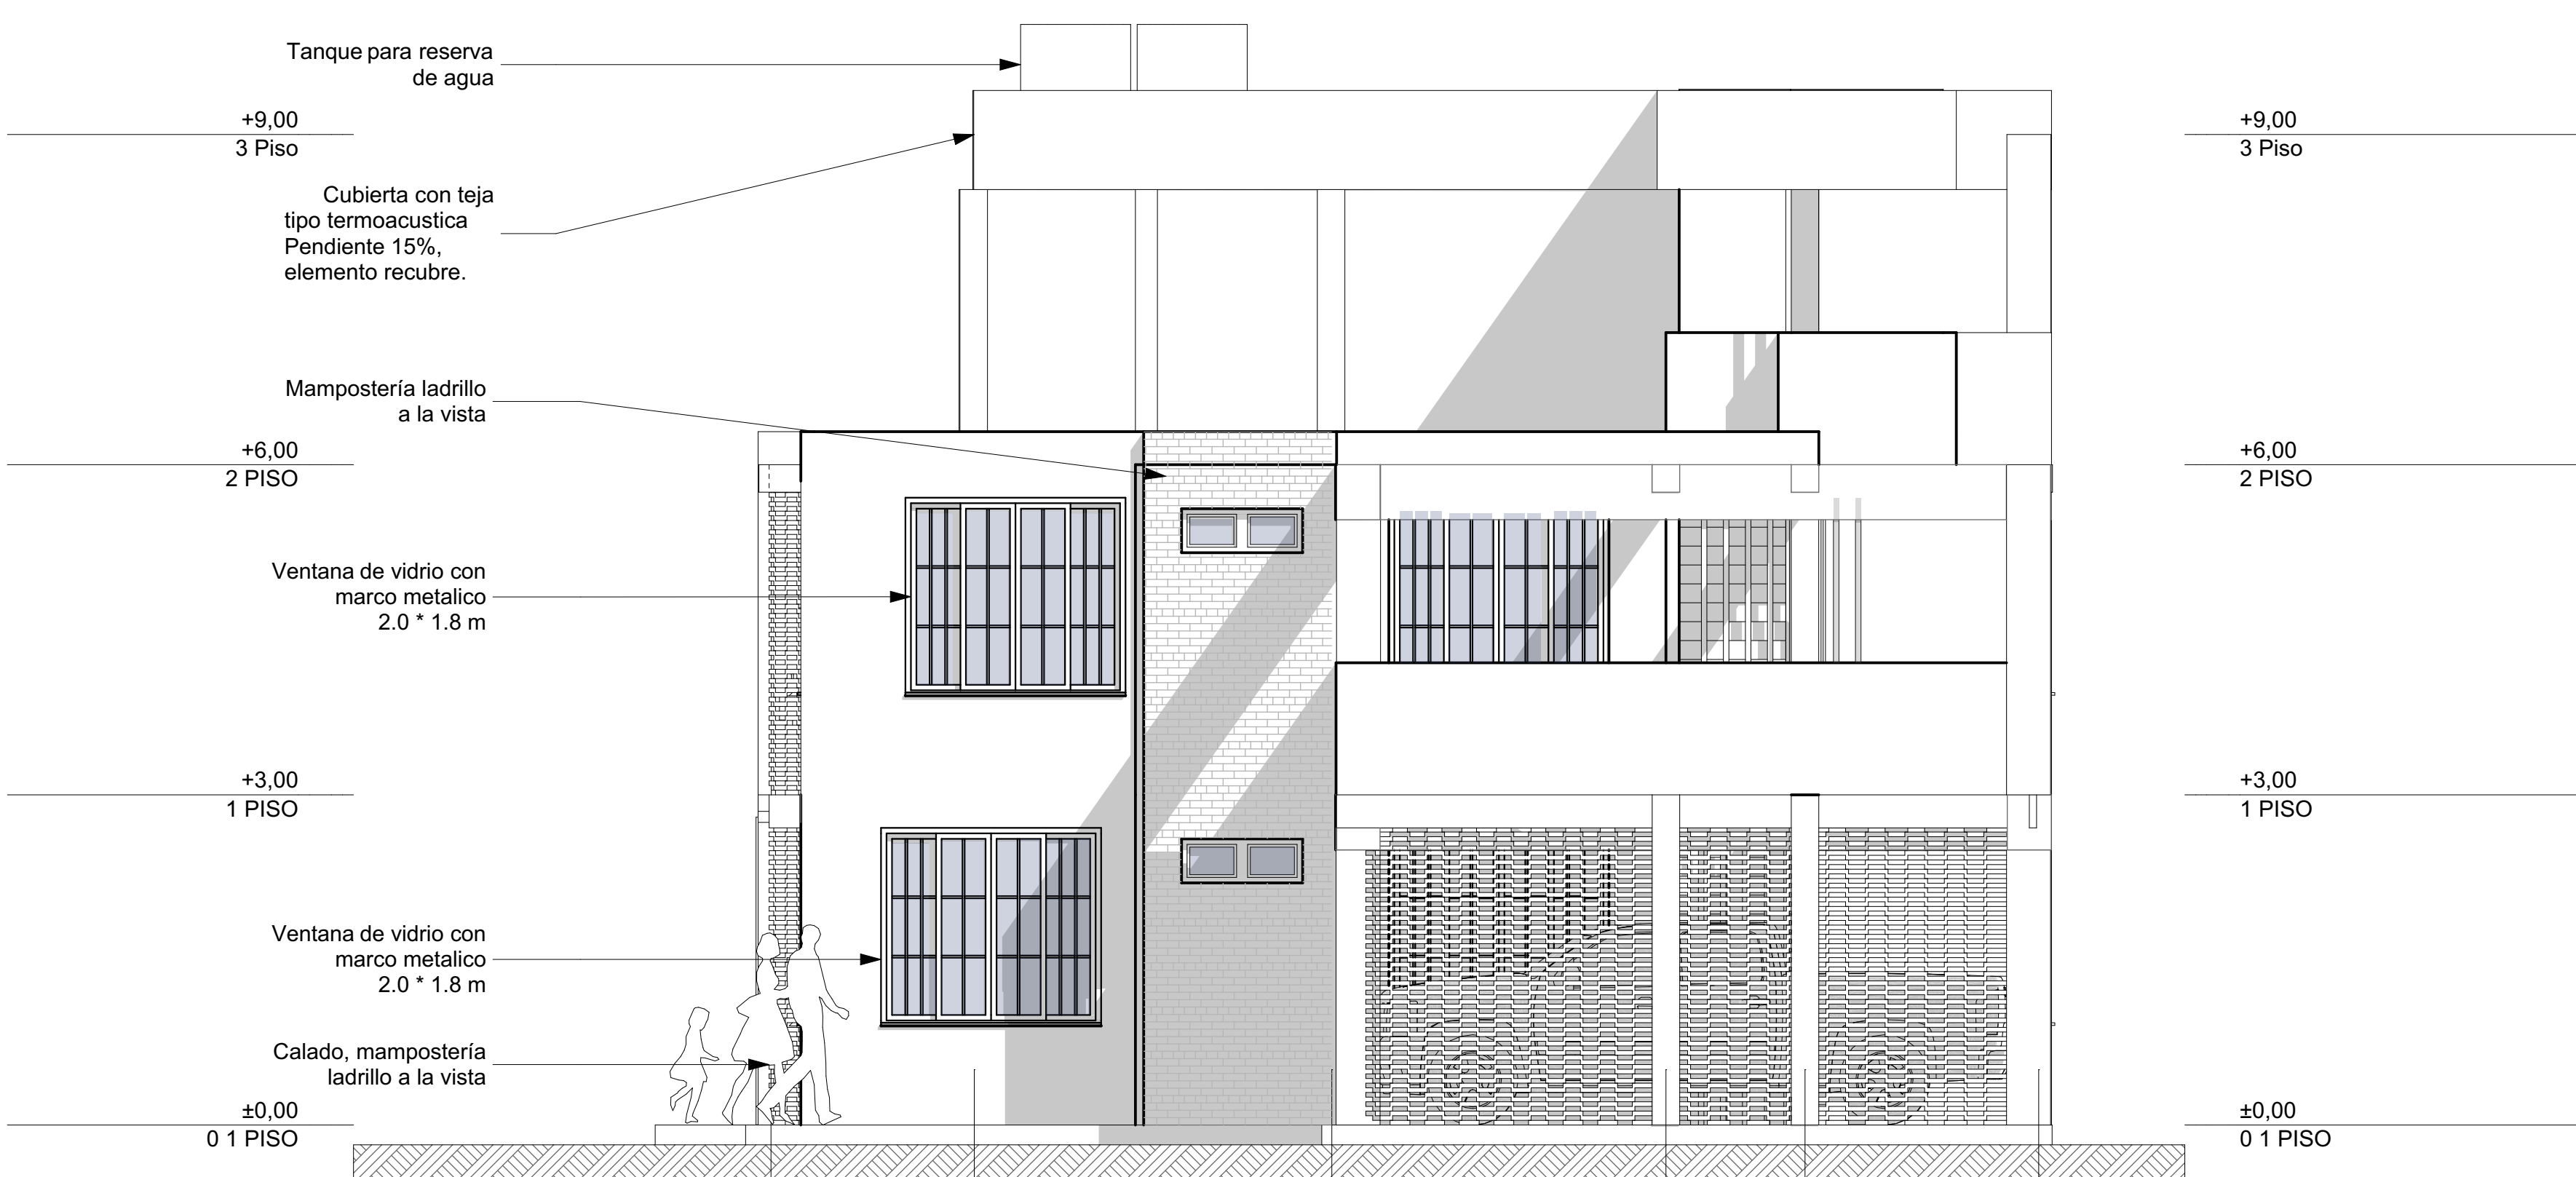

PROPIETARIOS: JUAN RIVAS	DISEÑO:  JESSICA VIVIANA RANGEL E. ARQUITECTA - DISEÑADORA DE ESPACIOS INTERIORES TEL: 317 210 43 49 - E-MAIL: RANGELJESSICA@GMAIL.COM	APROBÓ: 	CONTIENE: PLANTAS ARQUITECTÓNICAS, FACHADA , CUADRO DE ÁREAS Y LOCALIZACIÓN	FECHA: DICIEMBRE 2024	OBSERVACIONES:
DIRECCIÓN: VEREDA SANTAMARIA OIBA, SANTANDER			TRAMITE: LICENCIA DE CONSTRUCCIÓN NUEVA	ESCALA: 1:50	PLANO: I DE I