




PLANTA PRIMER PISO

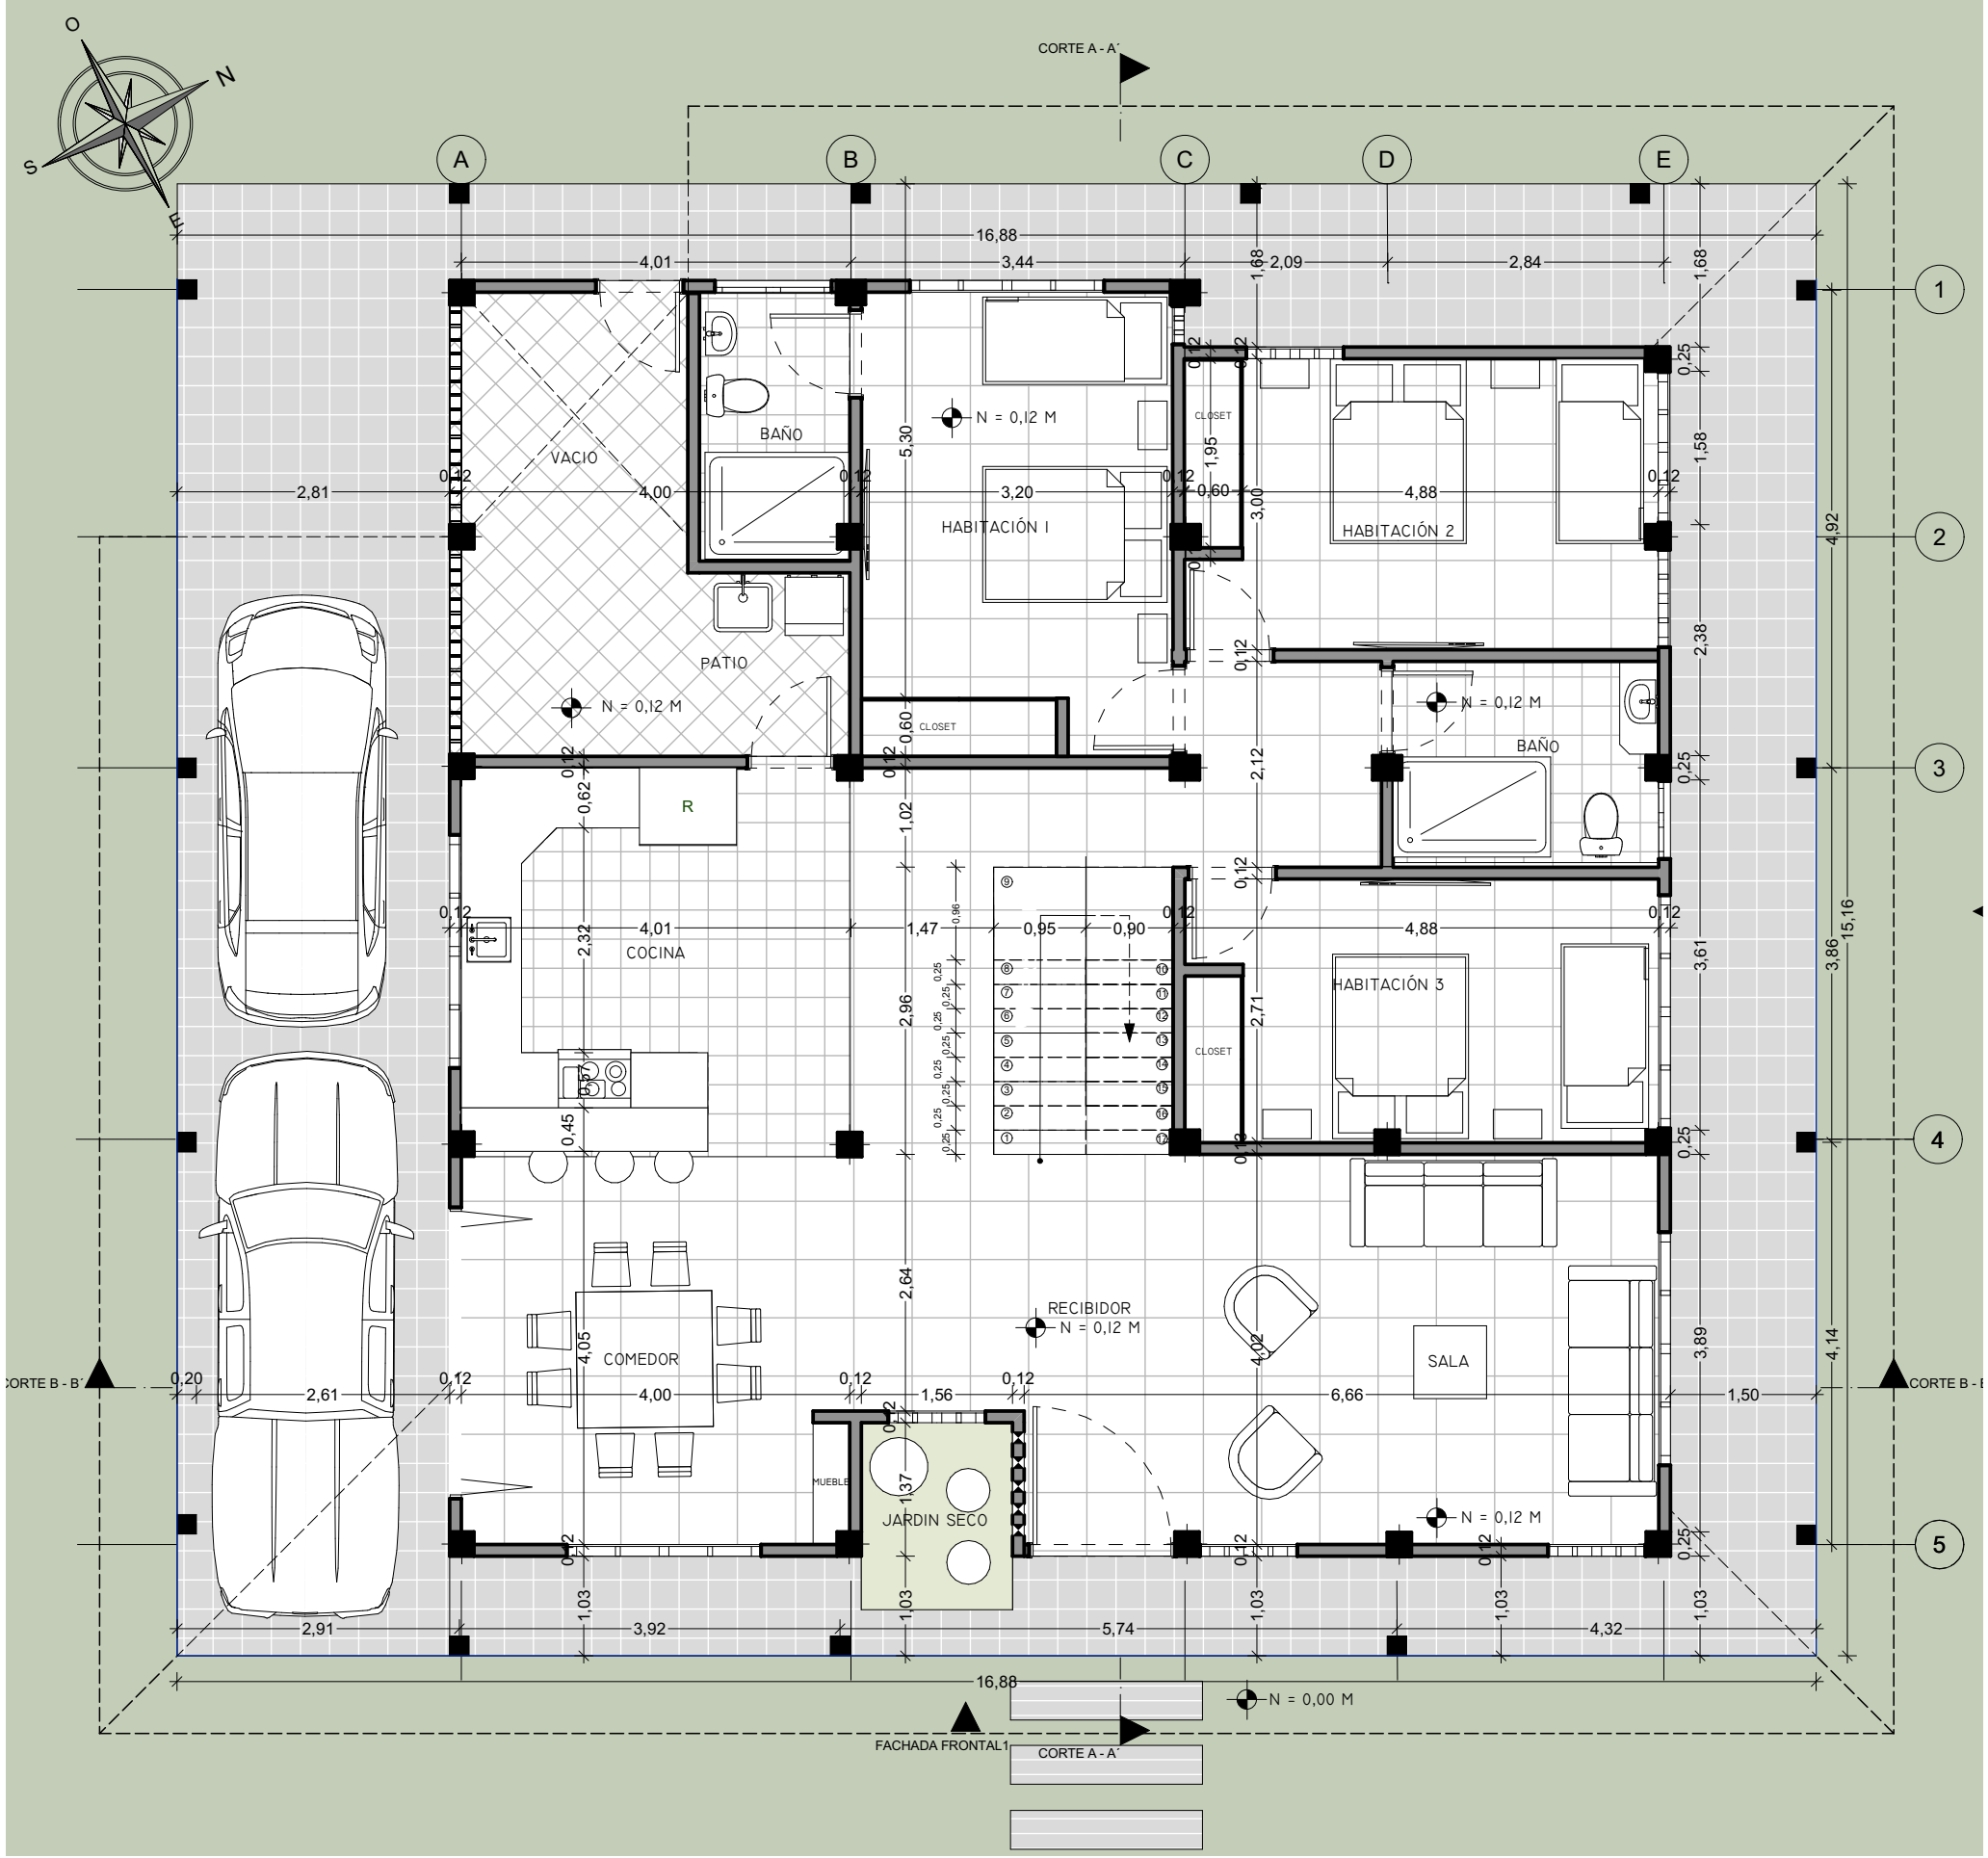


PLANTA SEGUNDO PISO

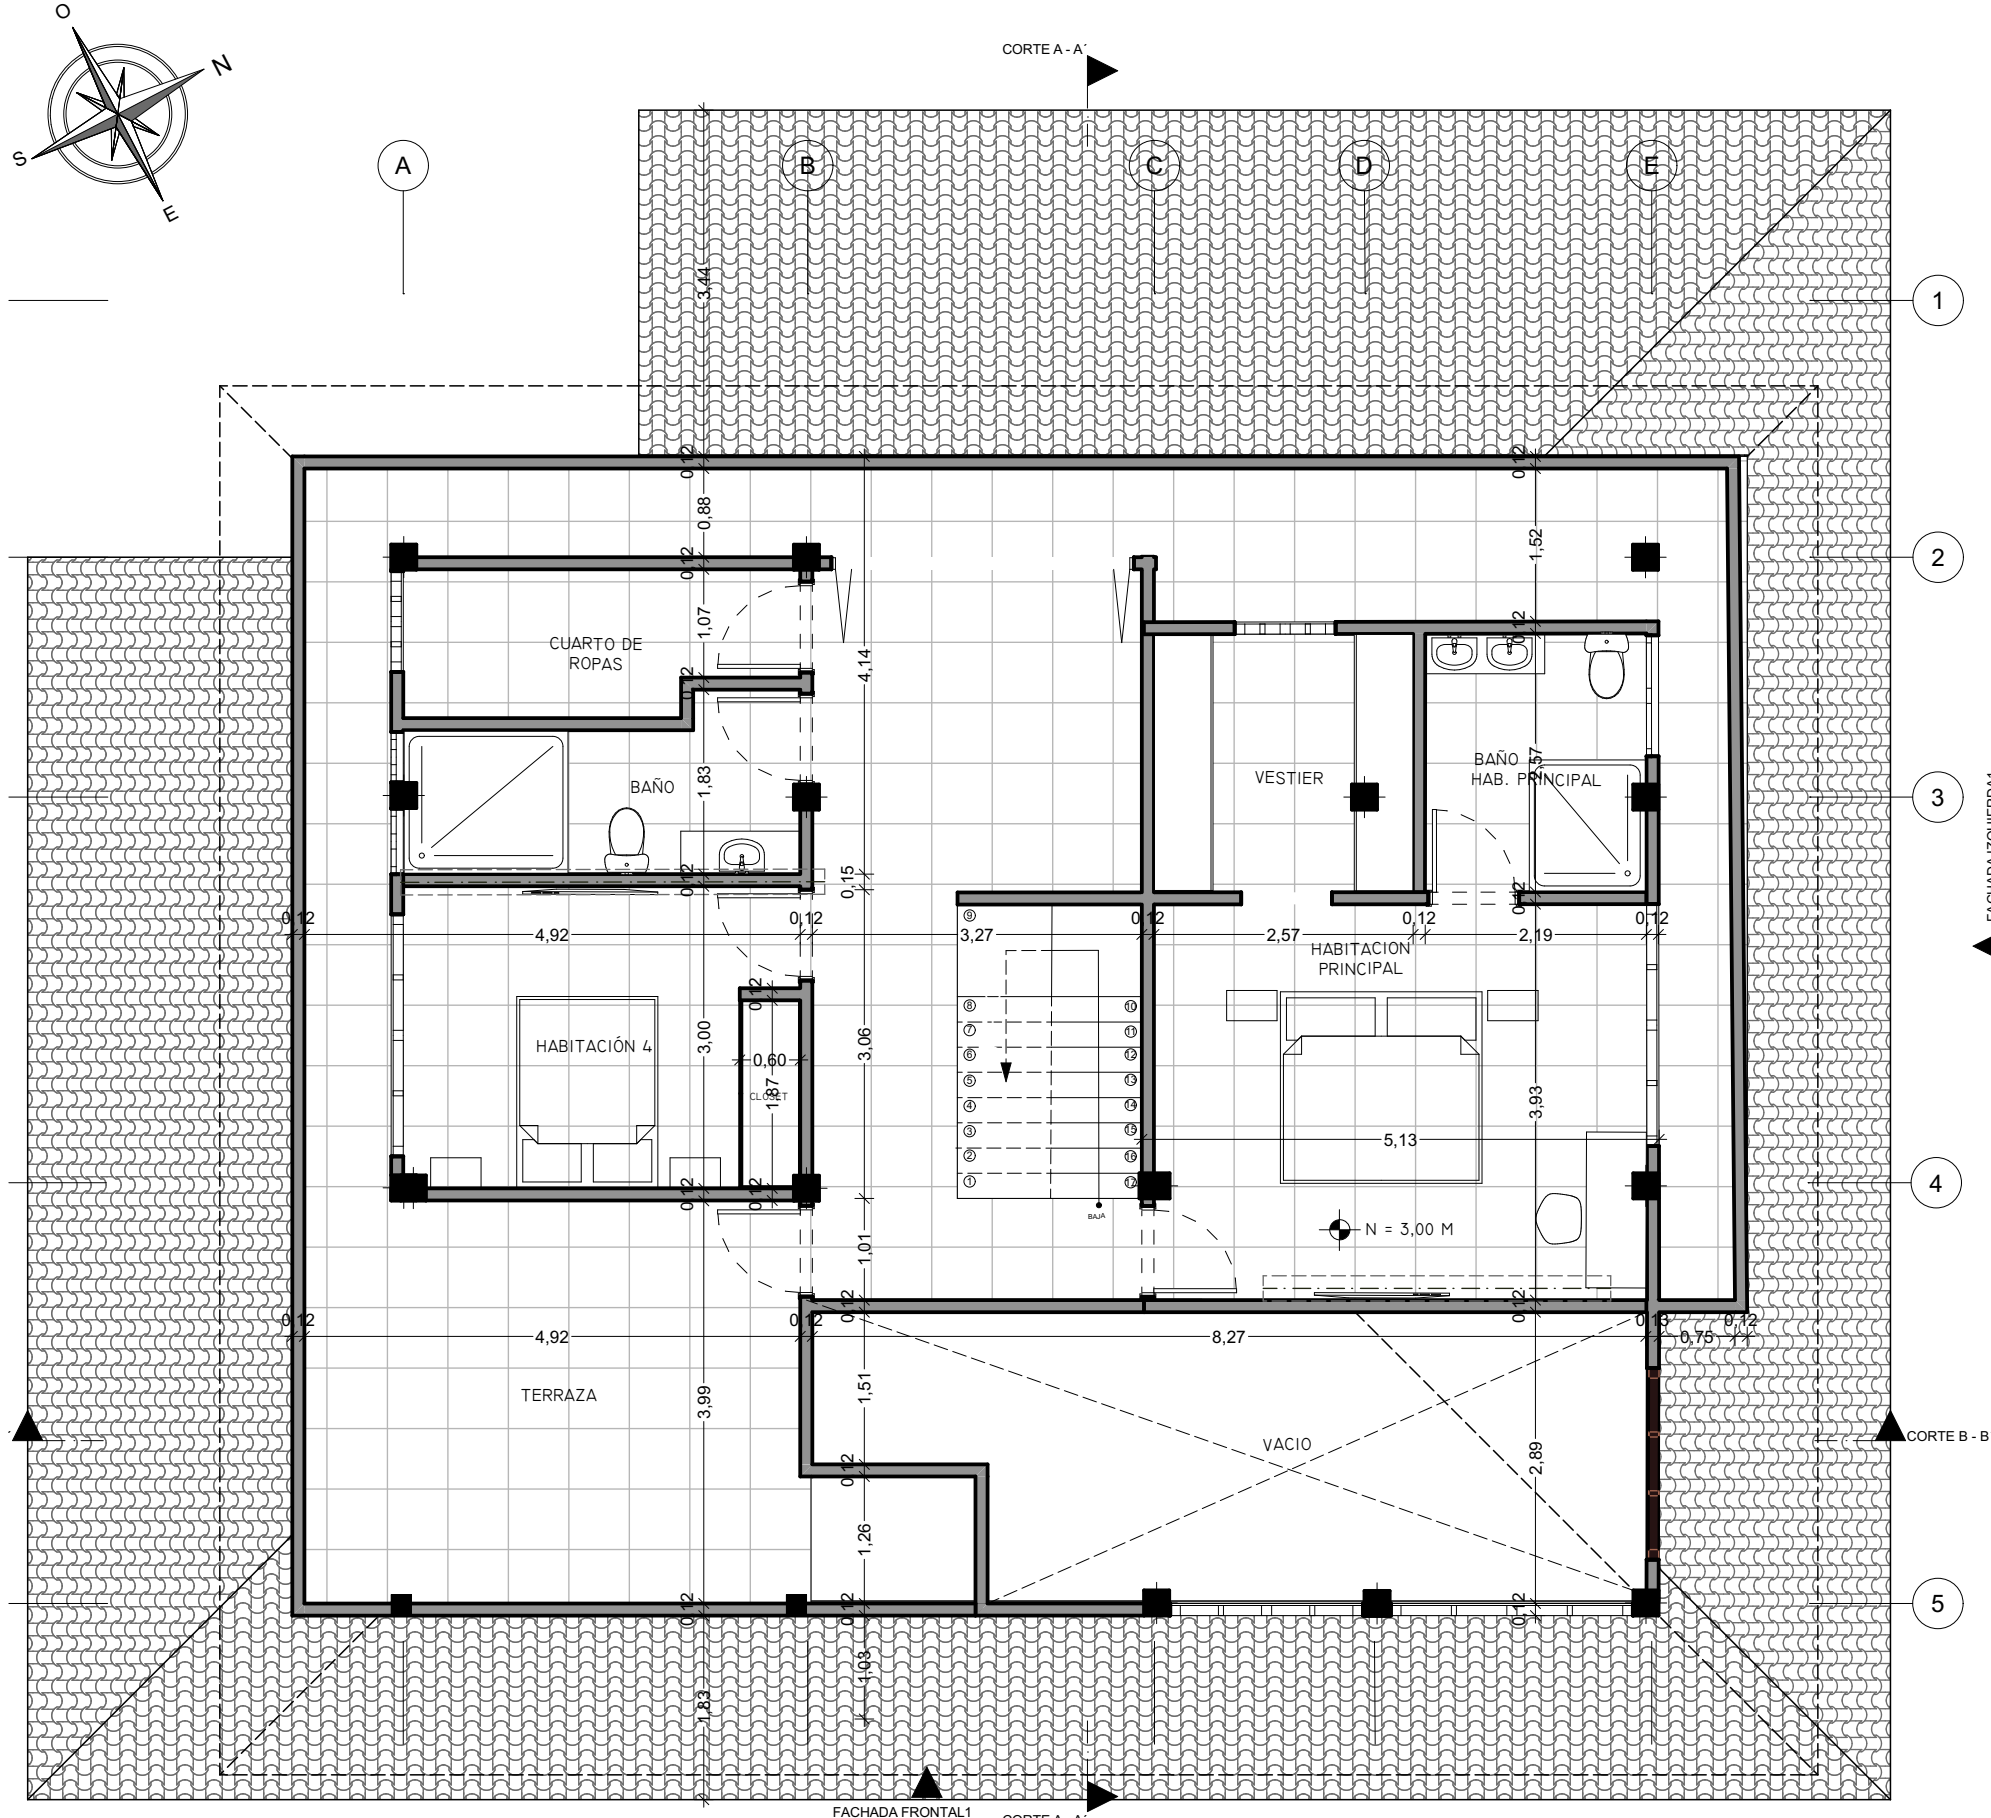

PLANTA DE CUBIERTA

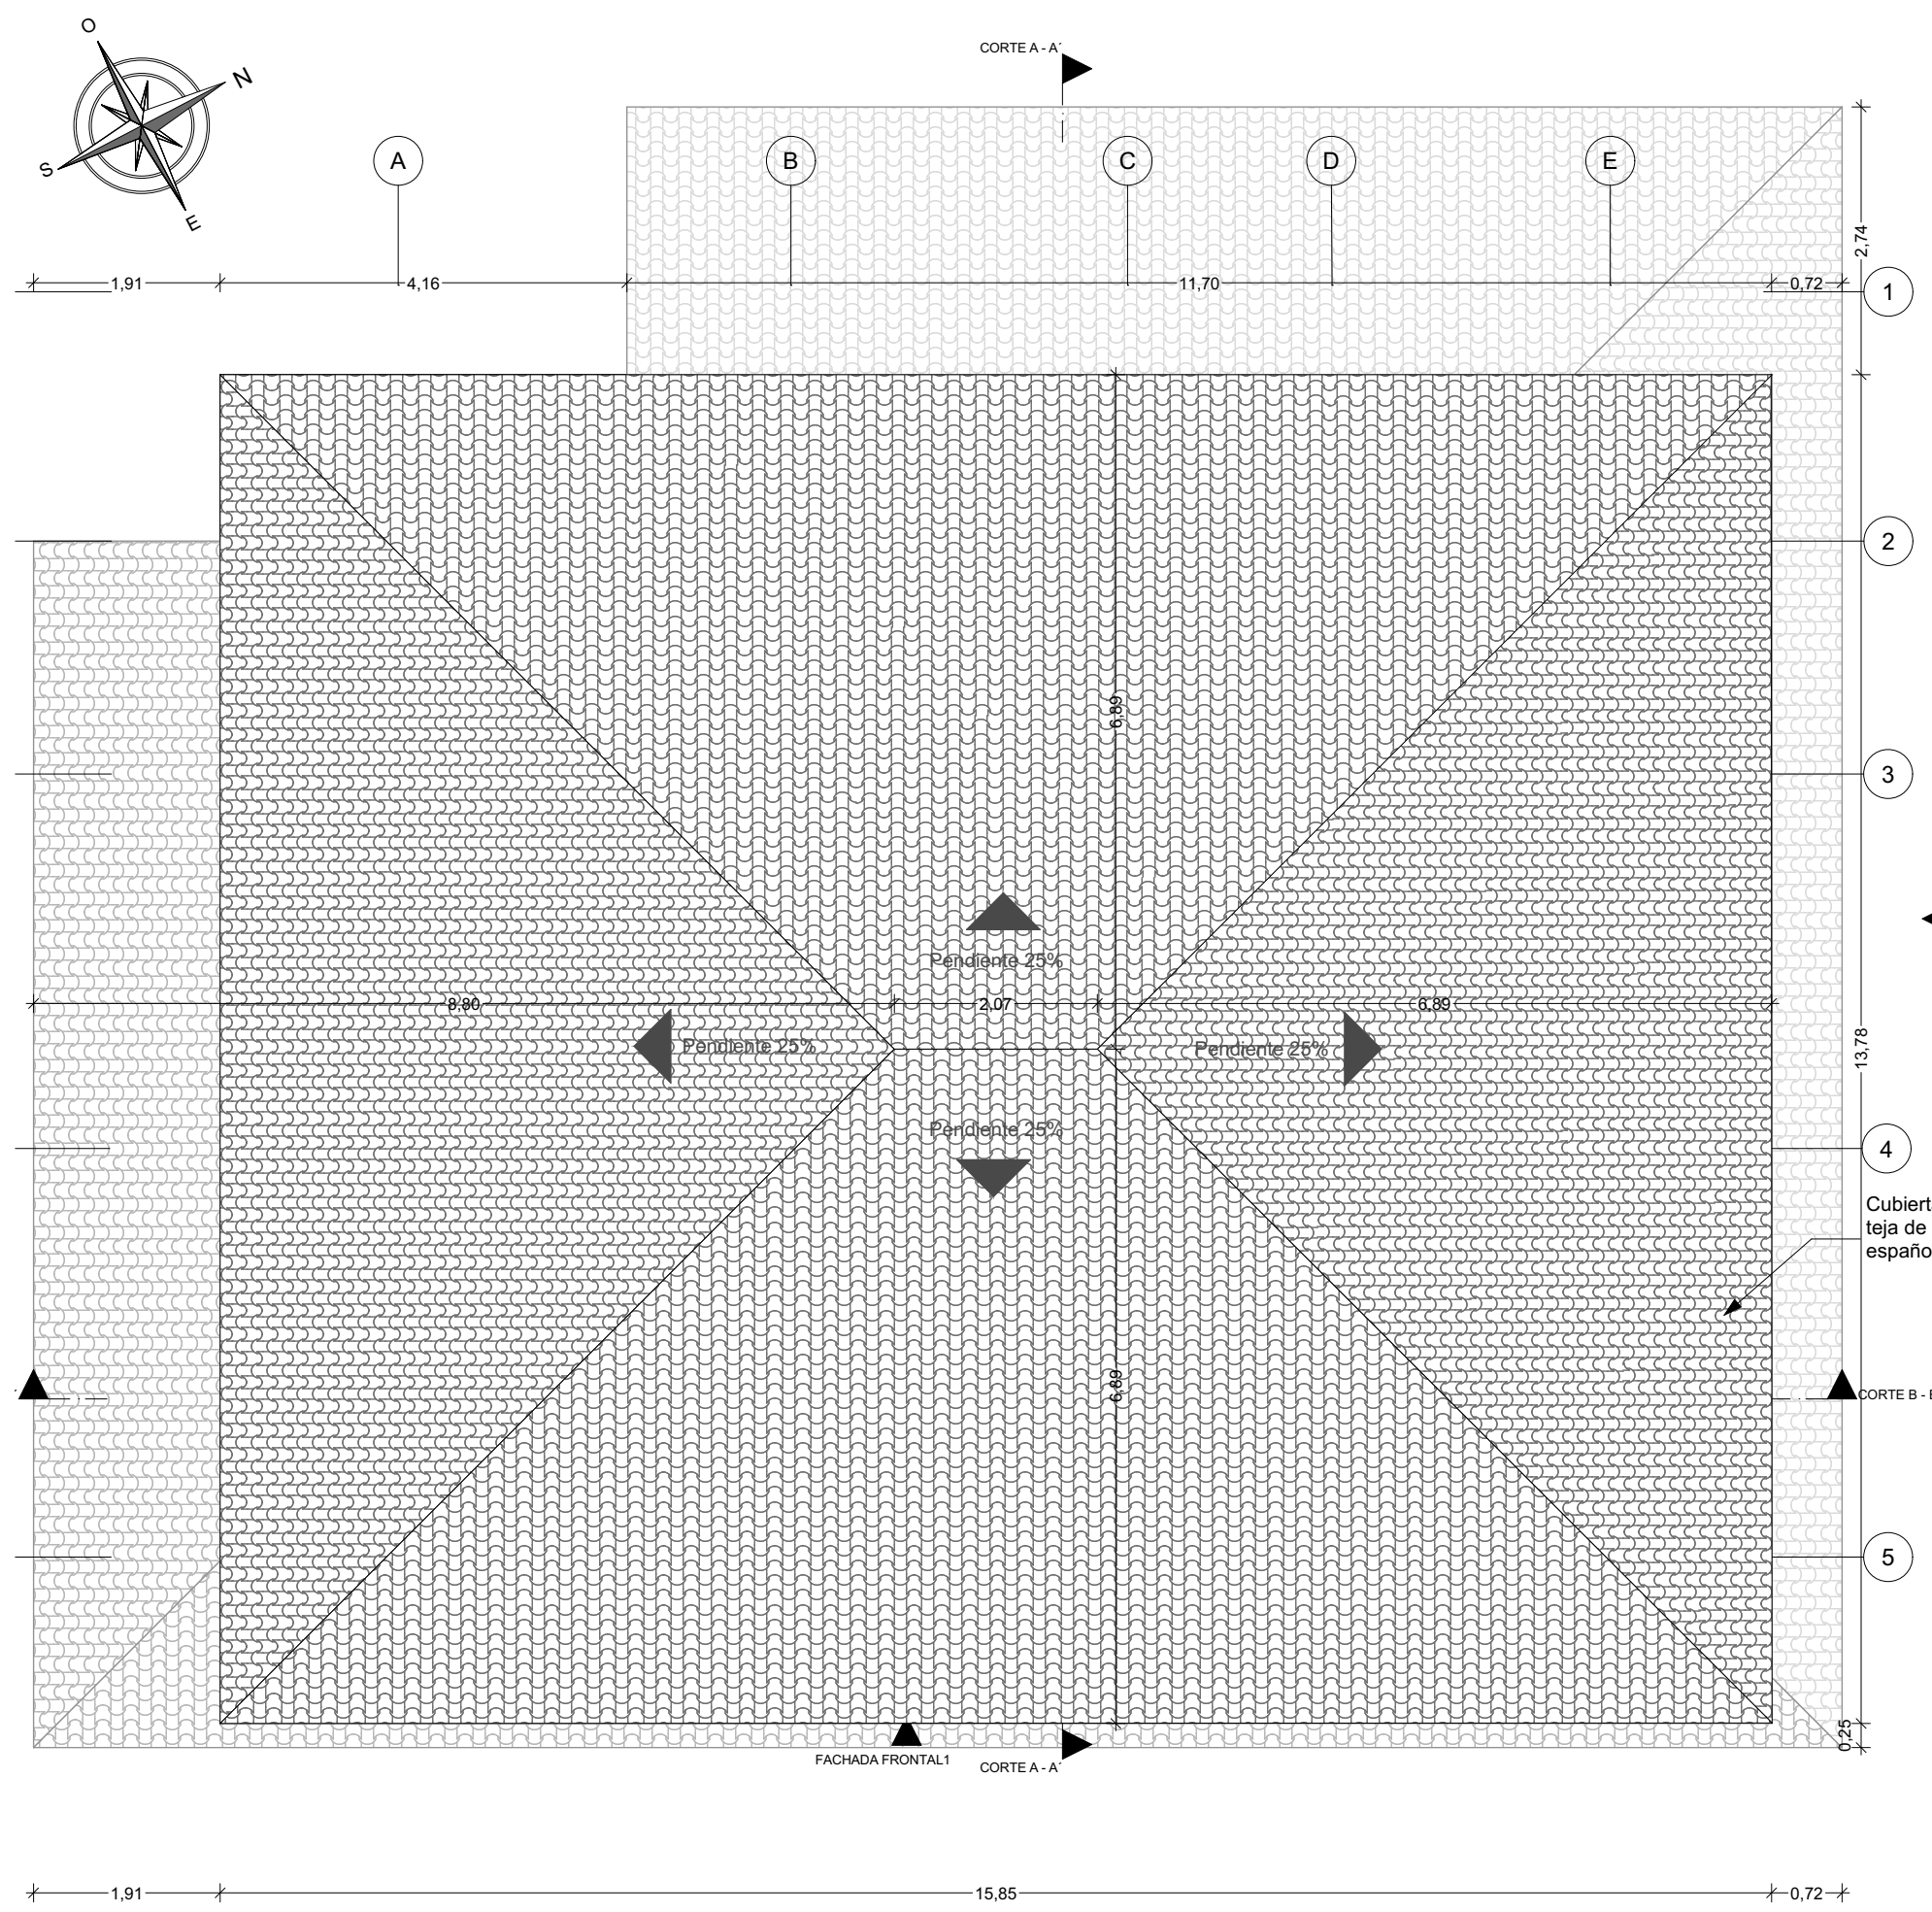


LOCALIZACIÓN

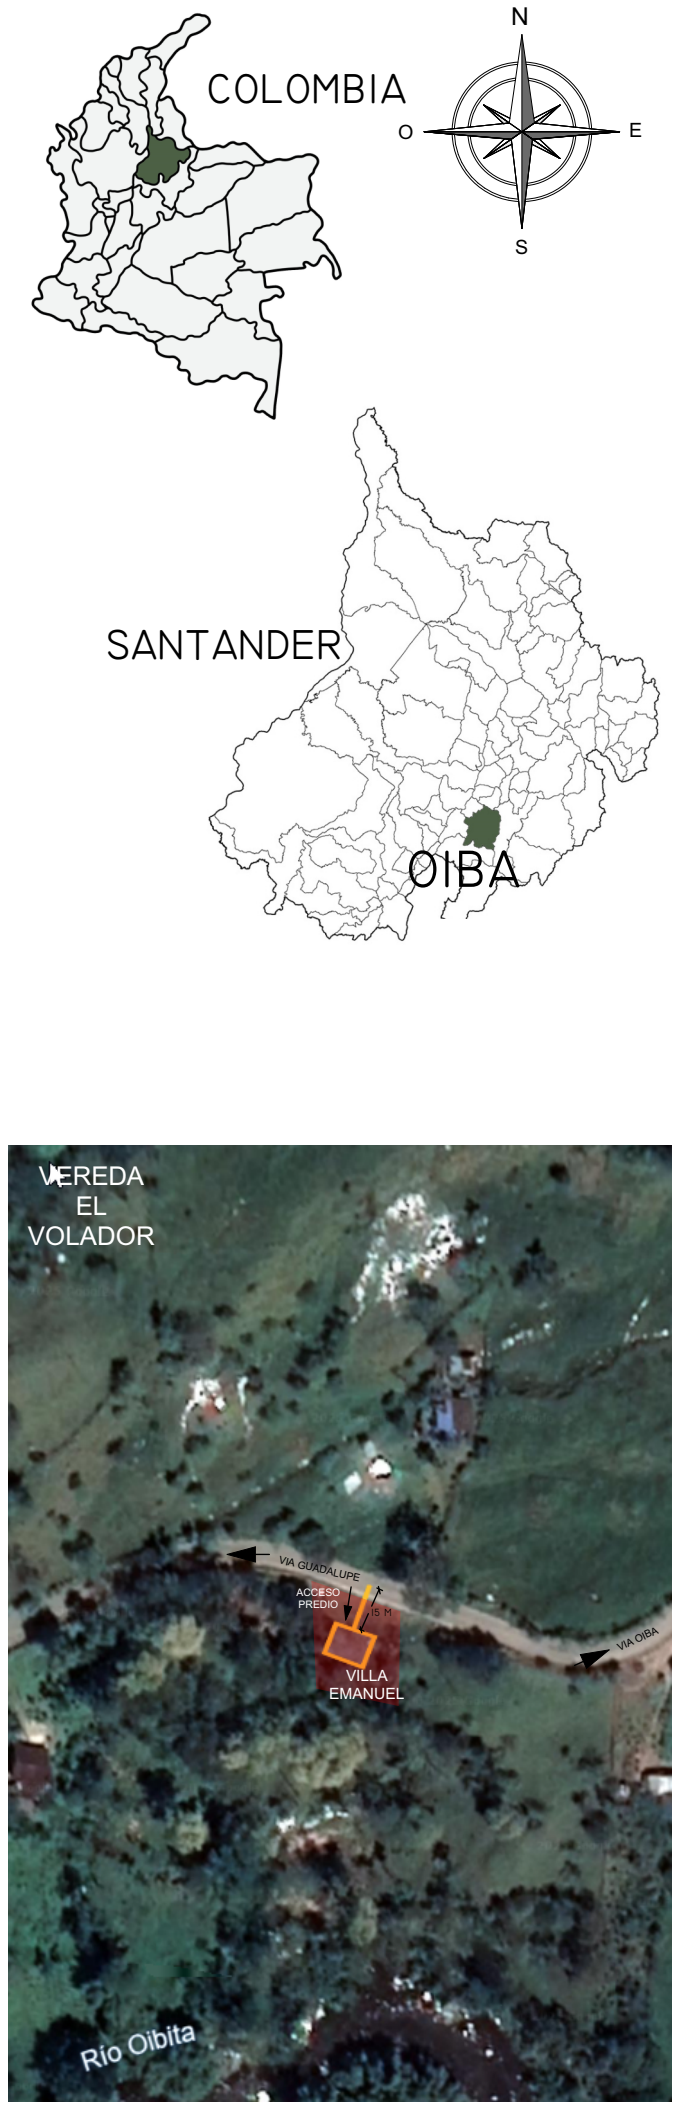


FACHADA PRINCIPAL




FACHADA LATERAL DERECHA

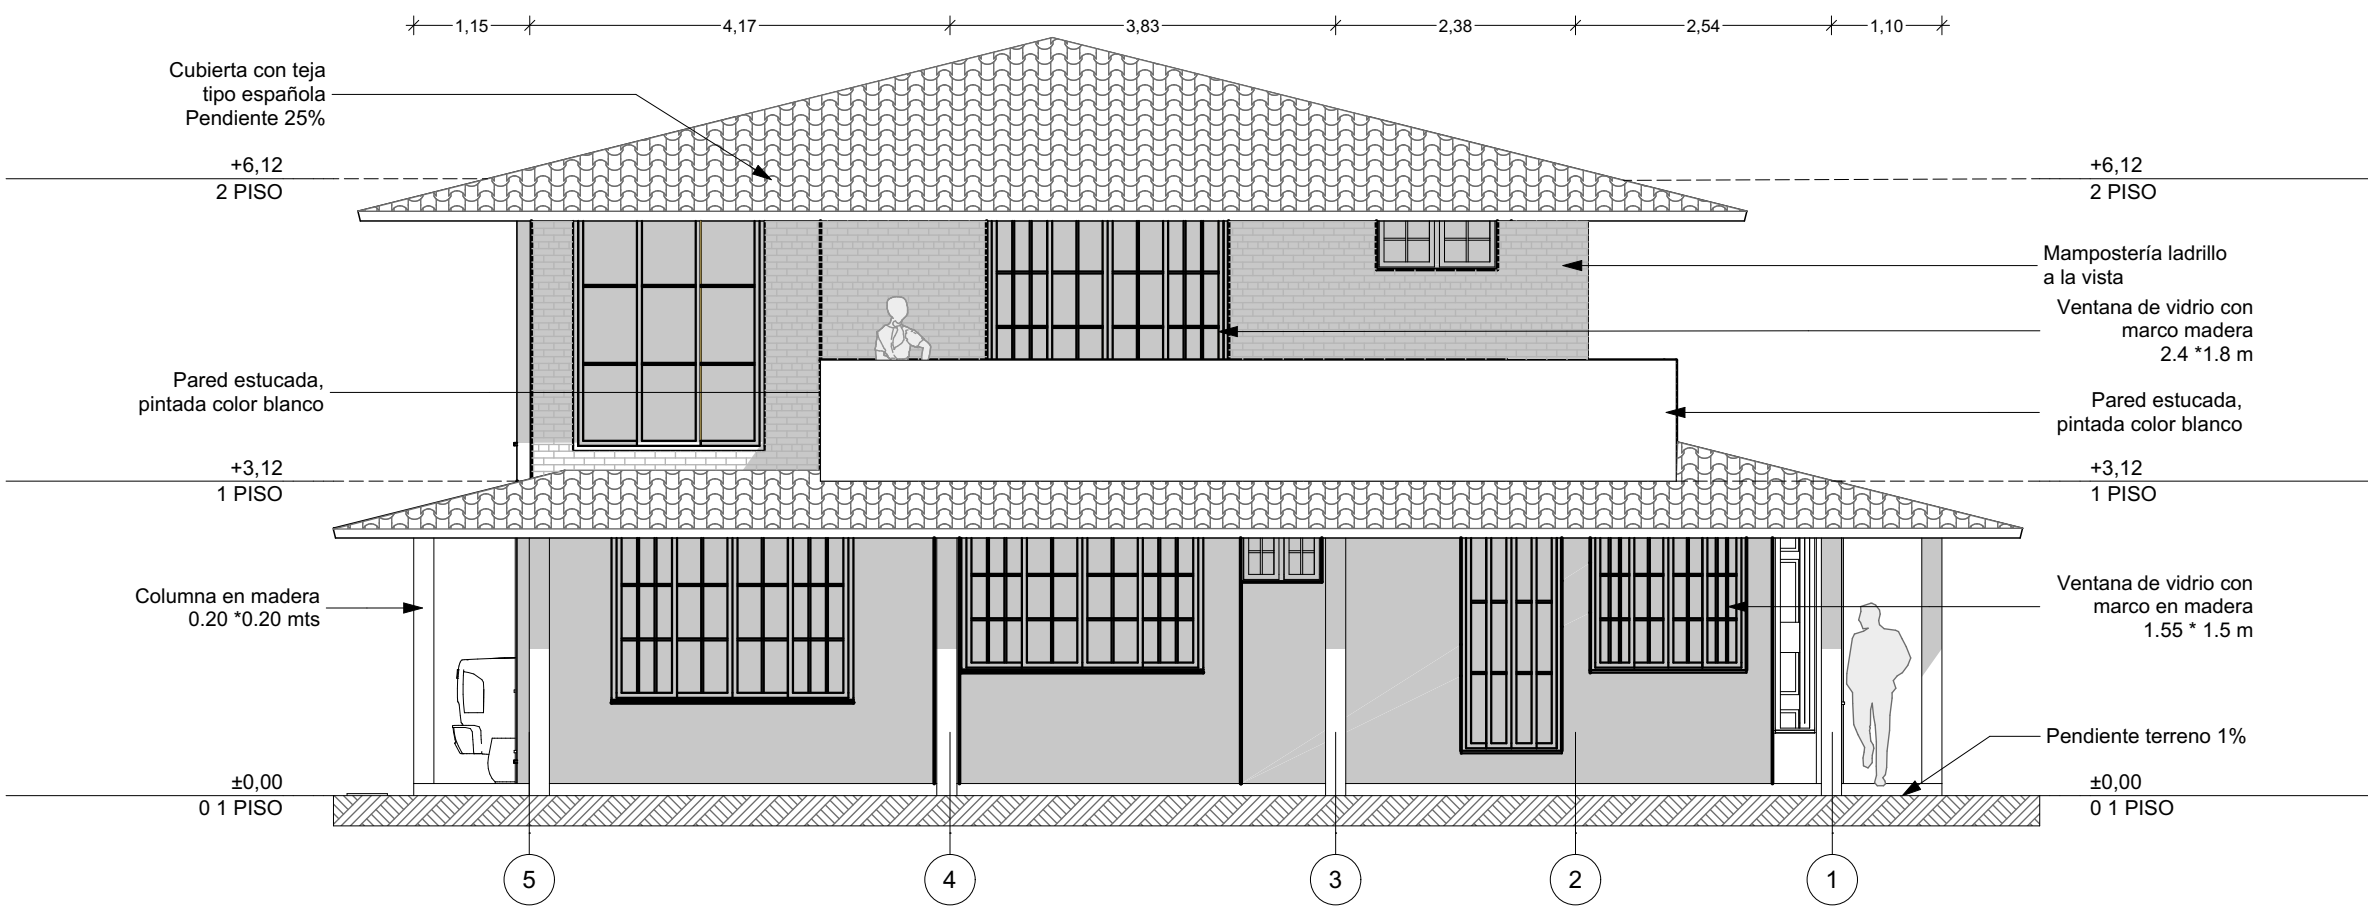

CORTE A - A'

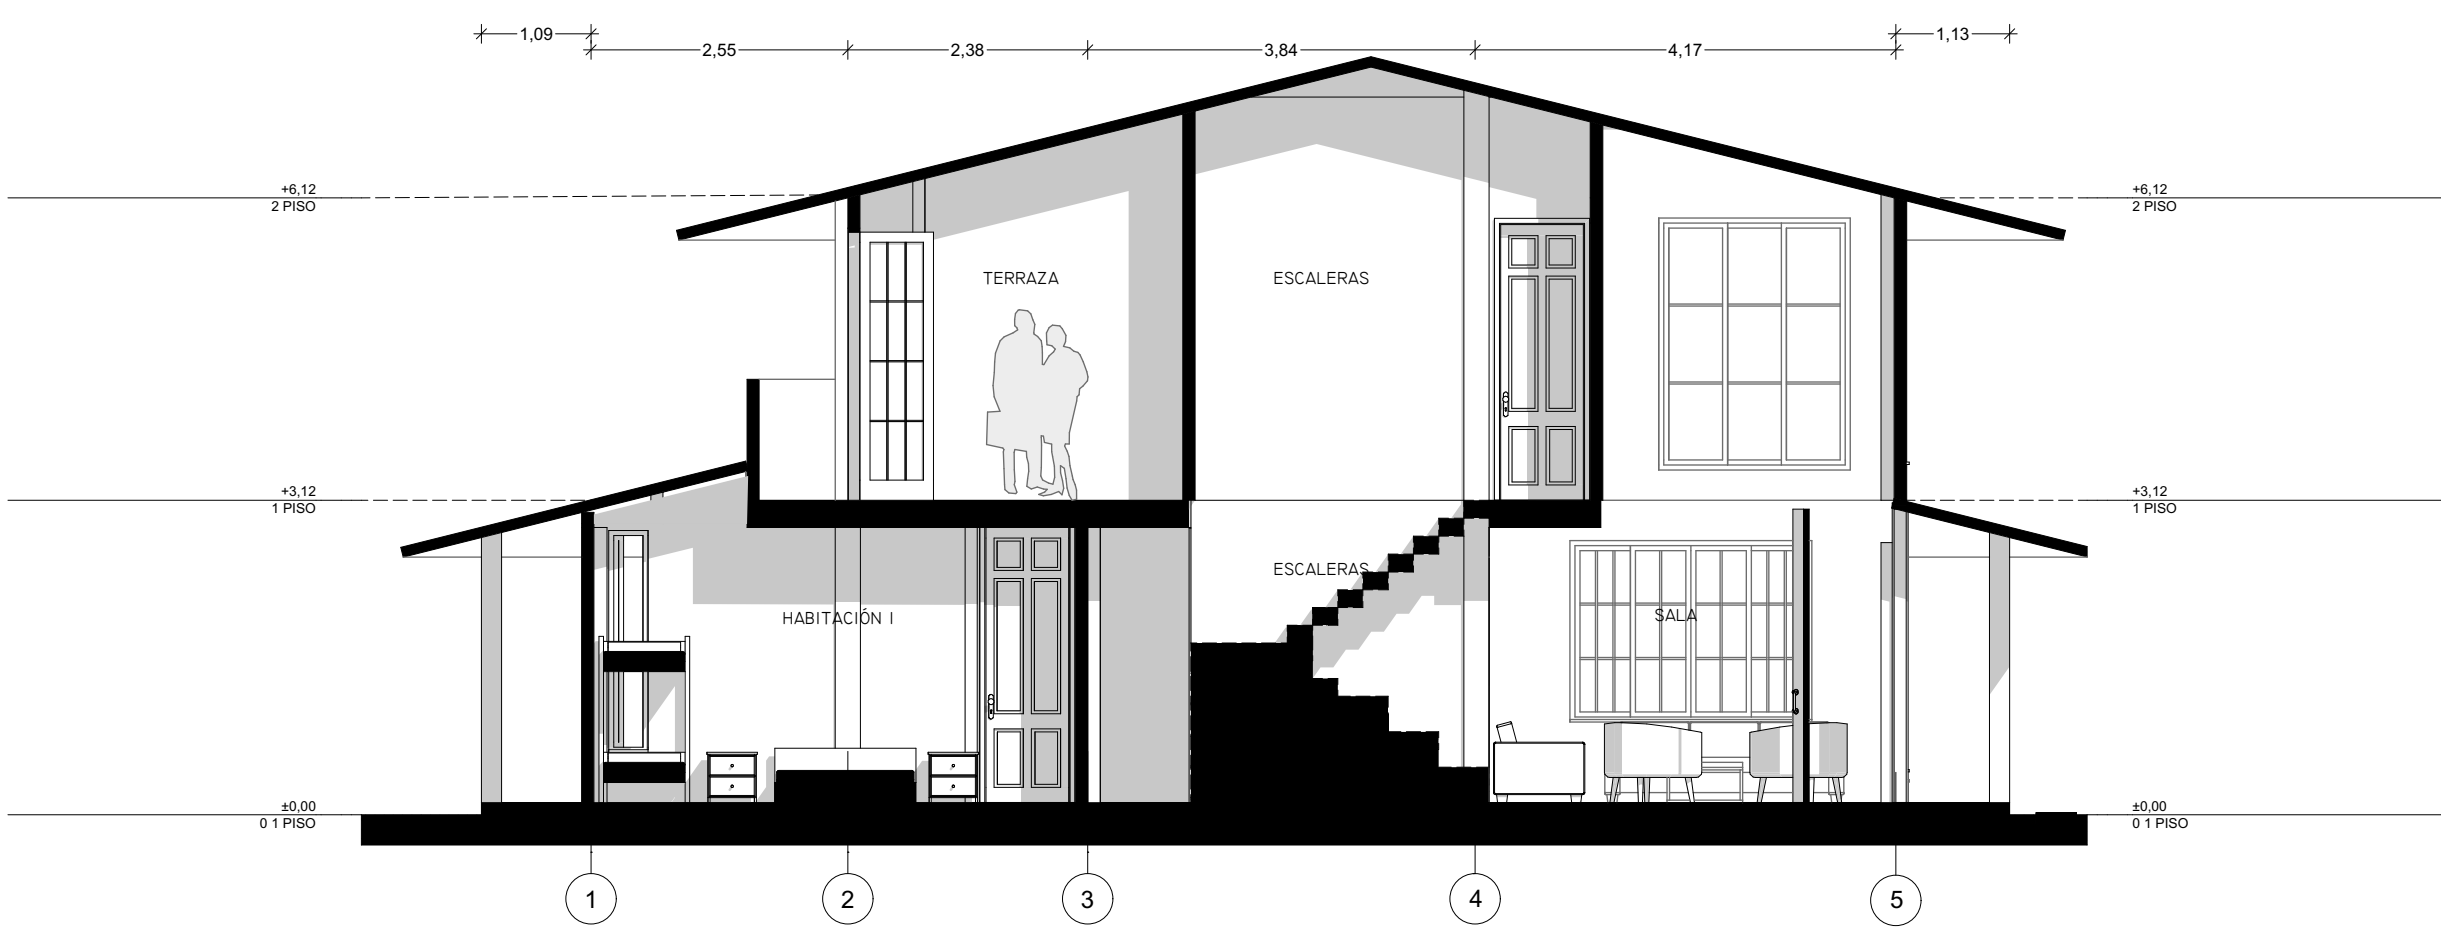

CORTE B - B'

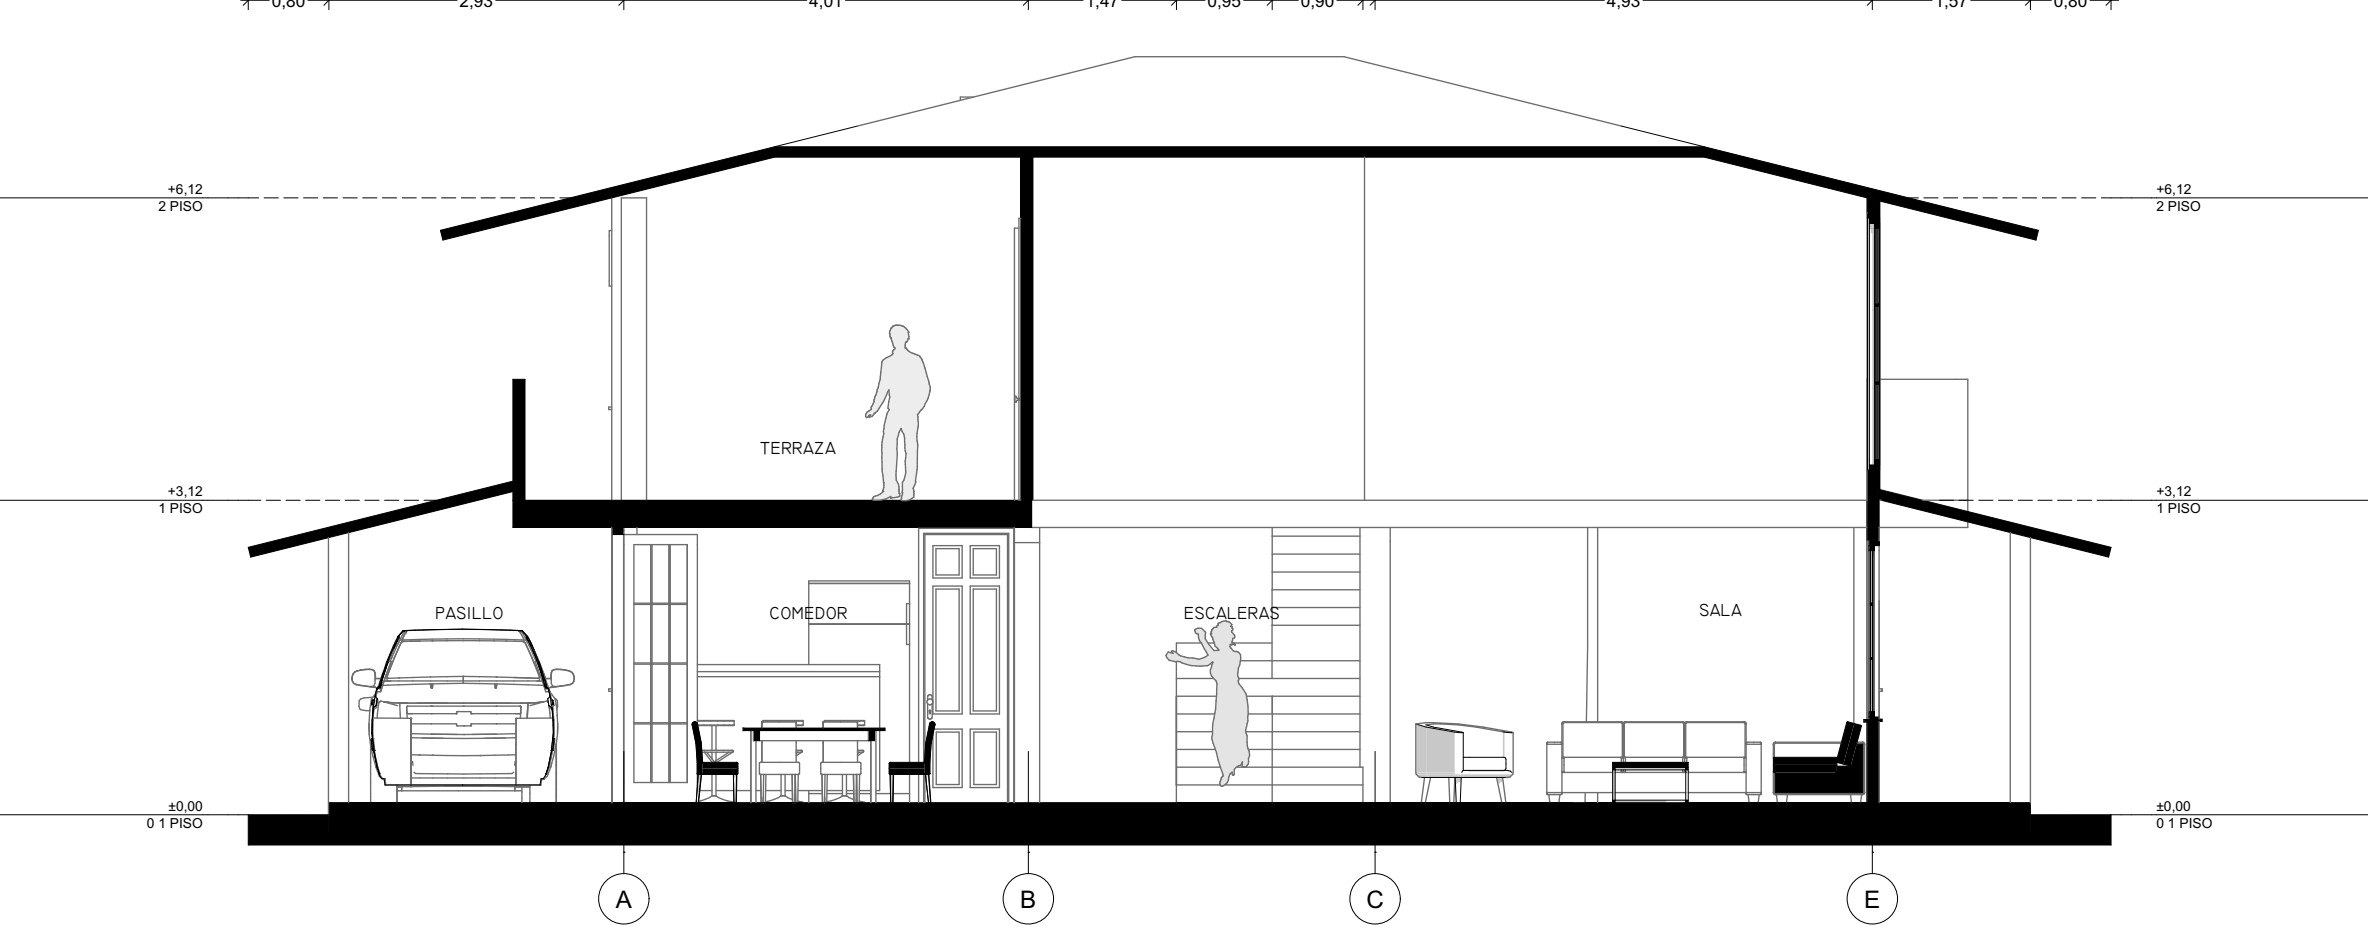

CUADRO DE AREAS	
ÁREA TOTAL DEL PREDIO	4.548 M2
ÁREA CONSTRUIDA PISO 1	235 M2
ÁREA CONSTRUIDA PISO 2	163 M2
ÁREA TOTAL CONSTRUIDA	398 M2



PROPIETARIOS:

MIGUEL ANGEL PINTO BLANCO

DIRECCIÓN:

PREDIO VILLA EMANUEL
VEREDA EL VOLADOR
OIBA, SANTANDER

APROBÓ:

JESSICA VIVIANA RANGEL E.
ARQUITECTA - DISEÑADORA DE ESPACIOS INTERIORES

DISEÑO:

ARQ. JESSICA VIVIANA RANGEL ESPINOSA
M. A30632018-109873588

CONTIENE:

PLANTAS ARQUITECTÓNICAS, FACHADA
, CUADRO DE ÁREAS Y
LOCALIZACIÓN

TRAMITE:

LICENCIA DE CONSTRUCCIÓN NUEVA

FECHA:

JULIO 2025

ESCALA:

1:75

PLANO:

I DE I

OBSERVACIONES:

RECOMENDACIONES ESTRUCTURALES
- REVISAR PLANOS Y MEMORIA DE CALCULO ESTRUCTURAL.