




PLANTA PRIMER PISO

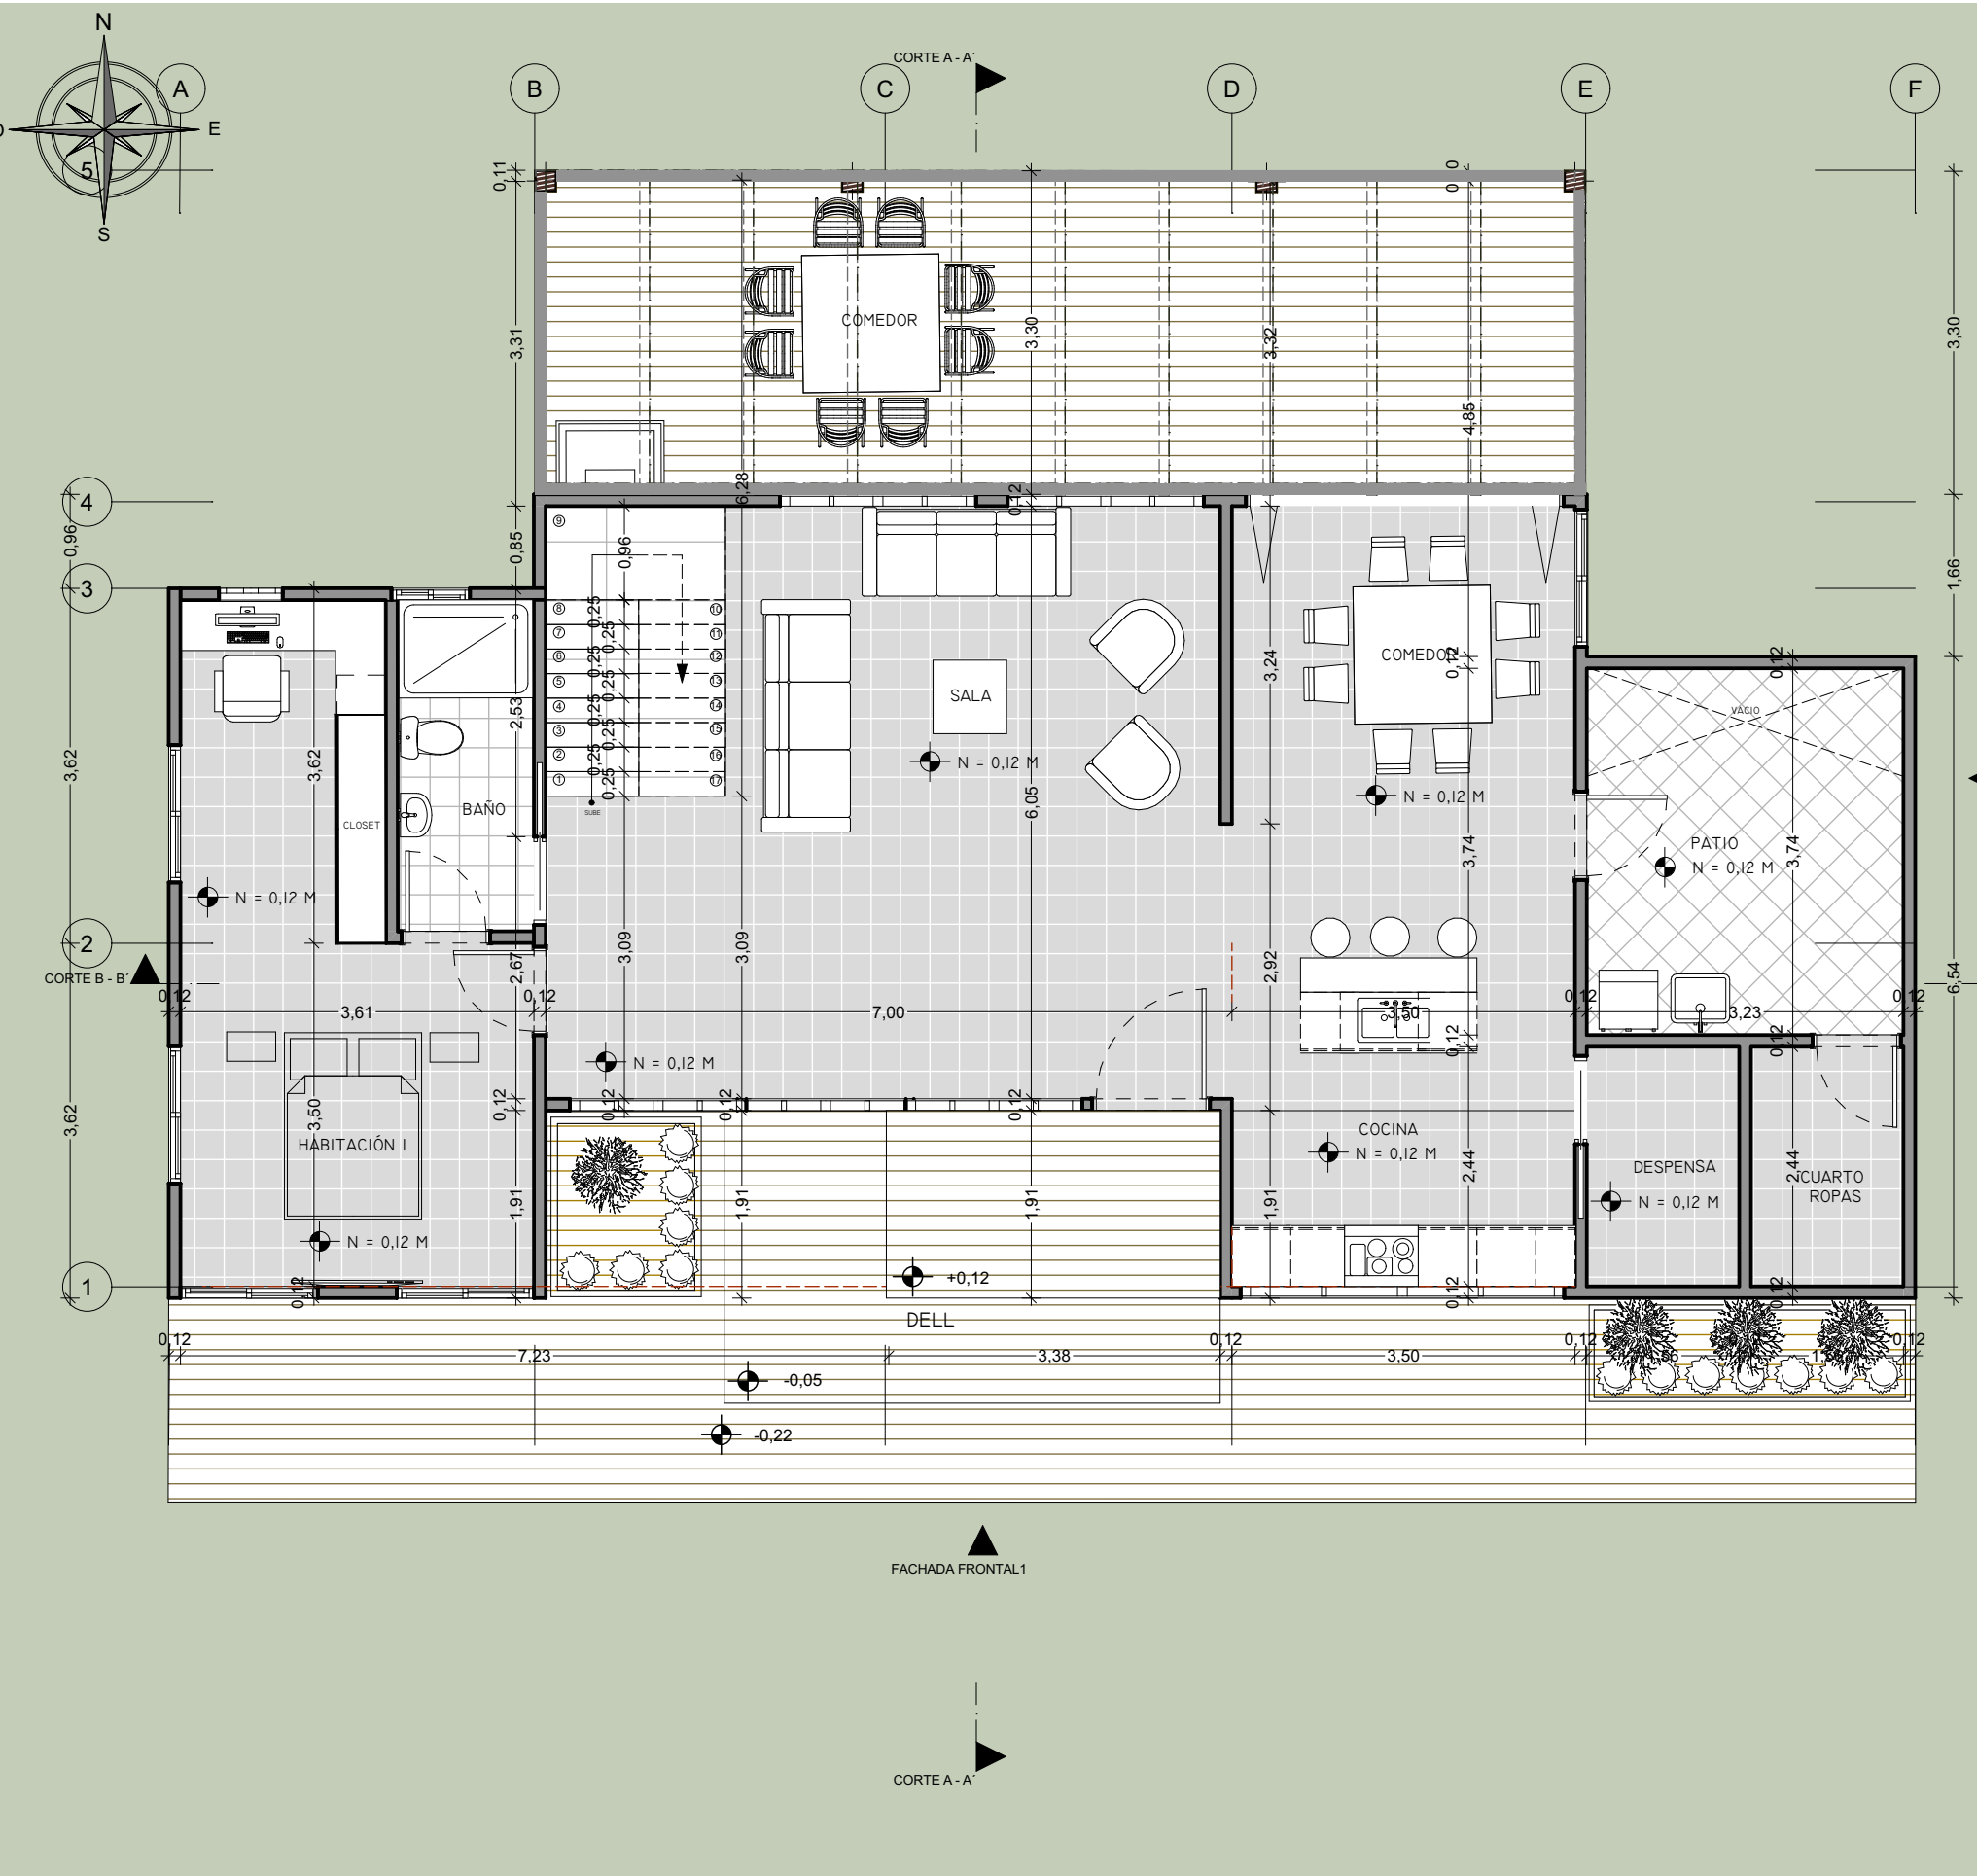


PLANTA SEGUNDO PISO

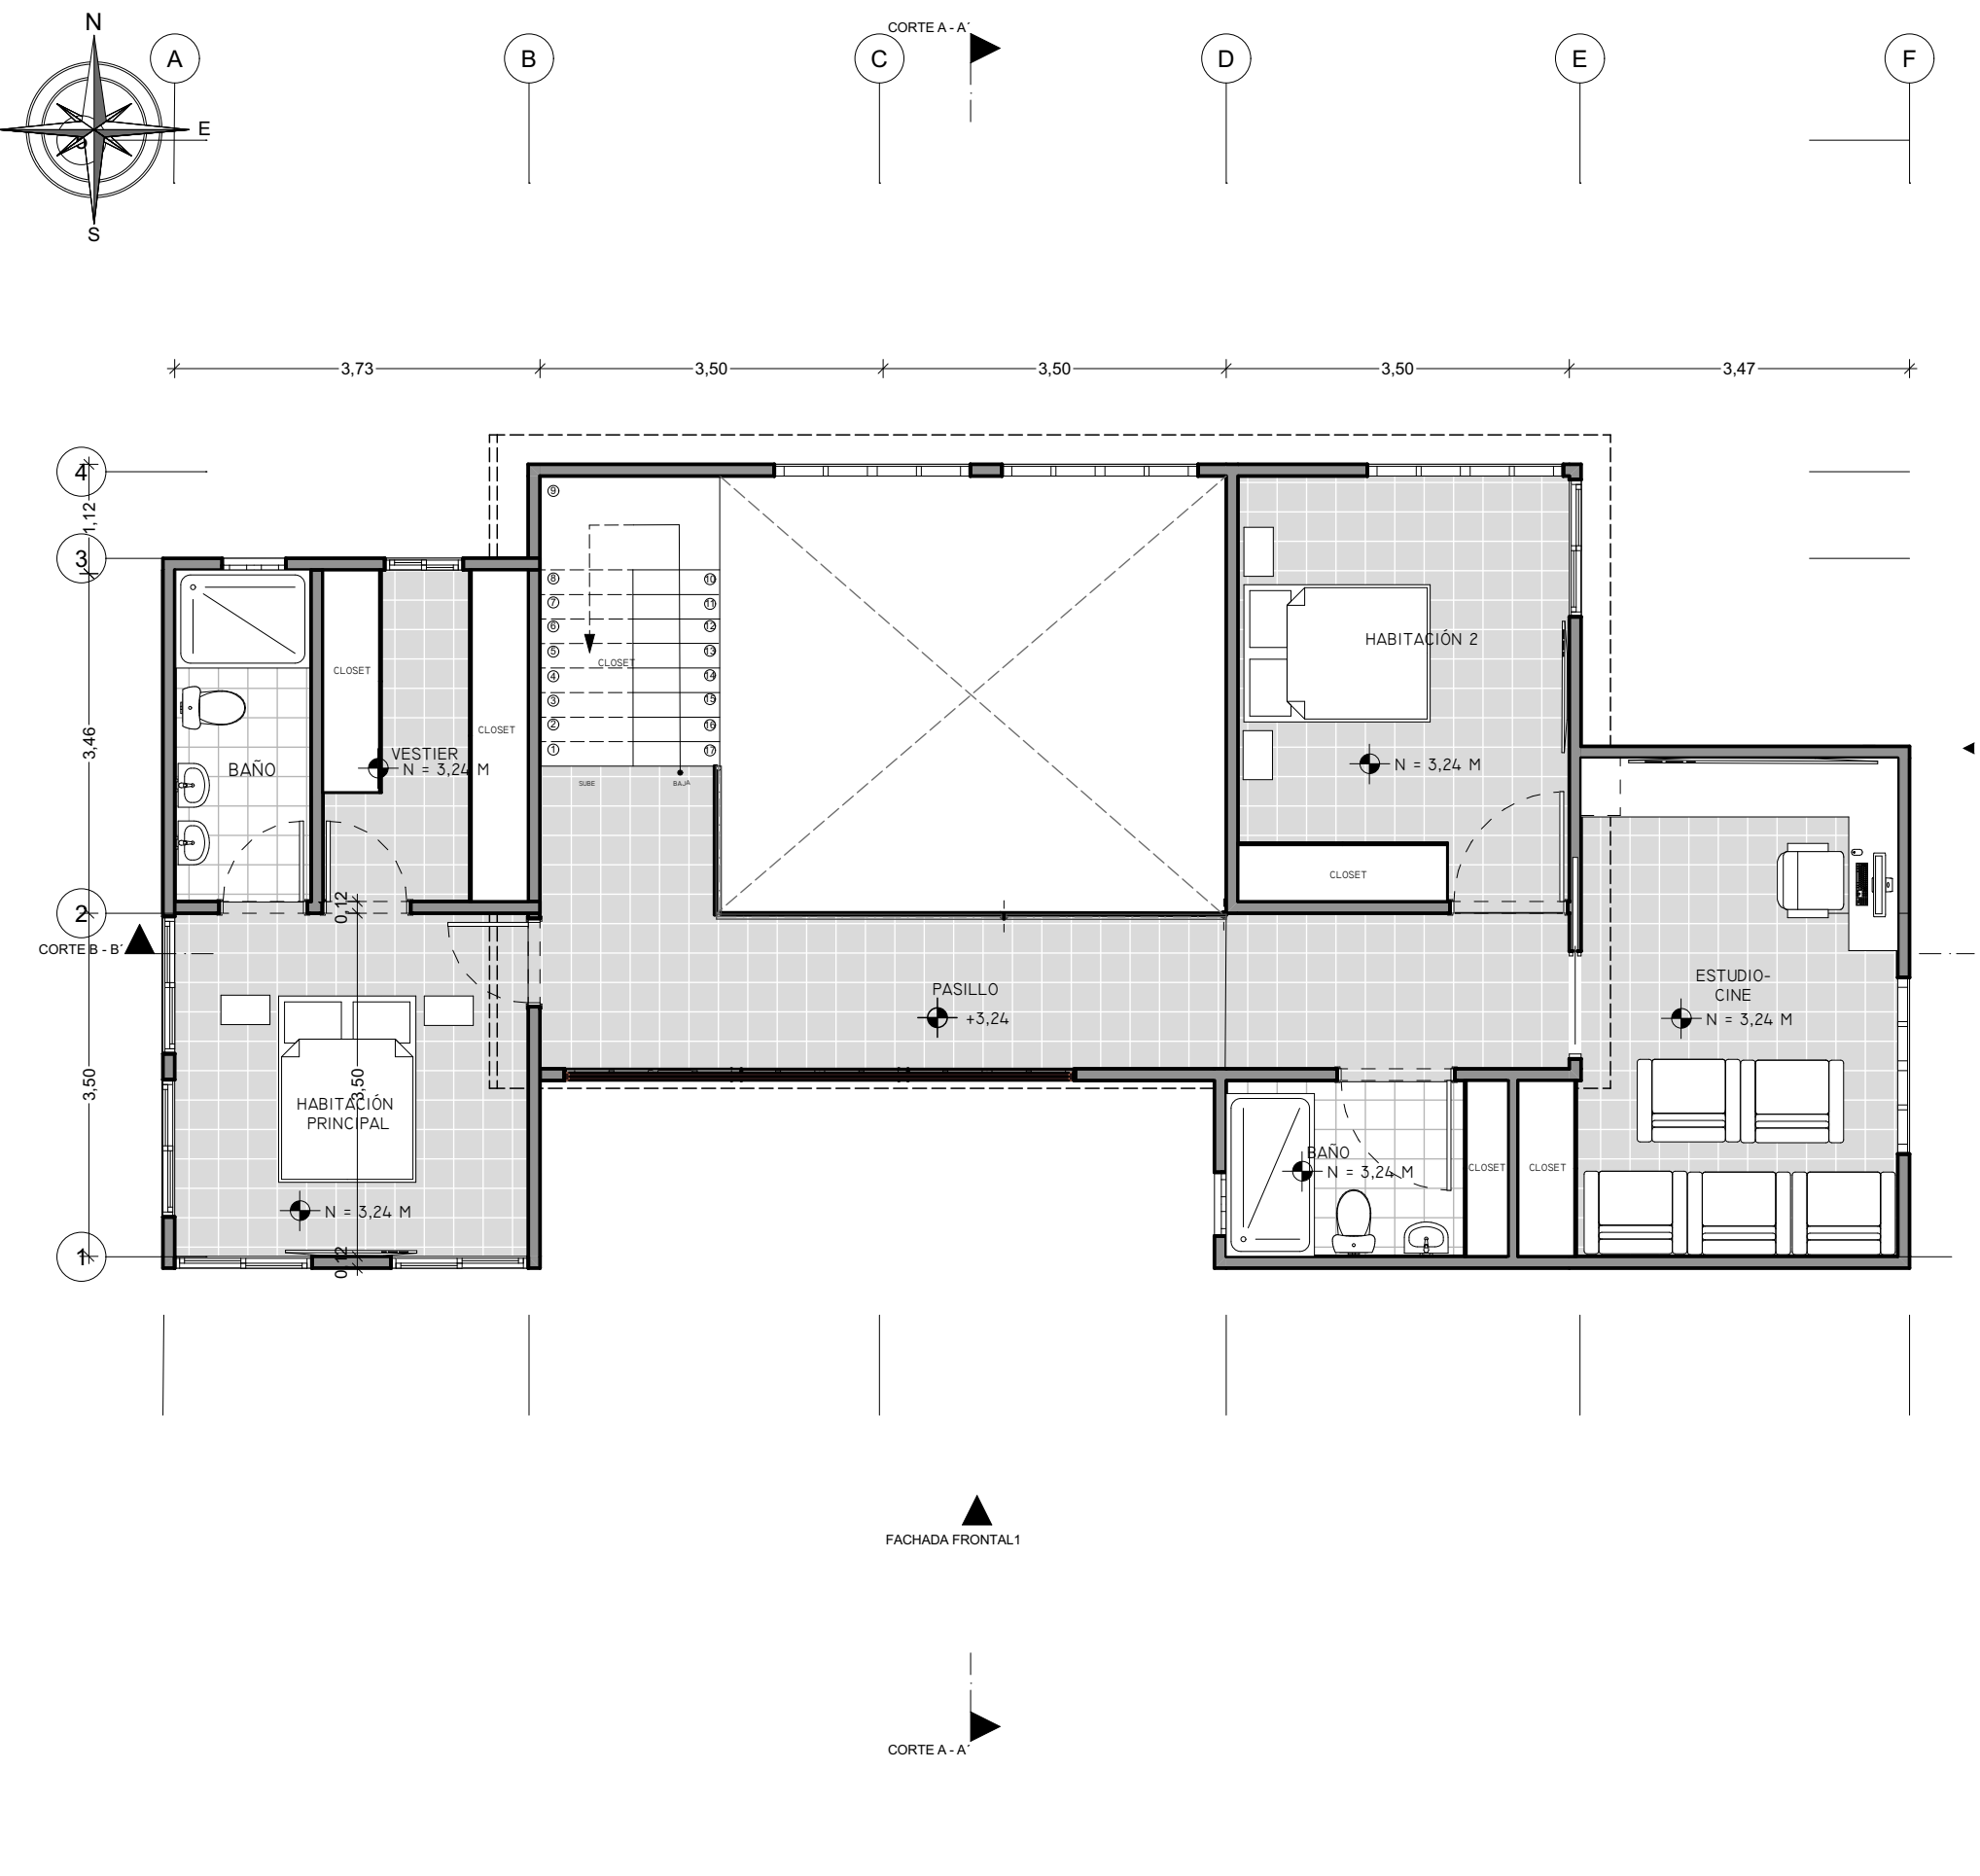

PLANTA DE CUBIERTA

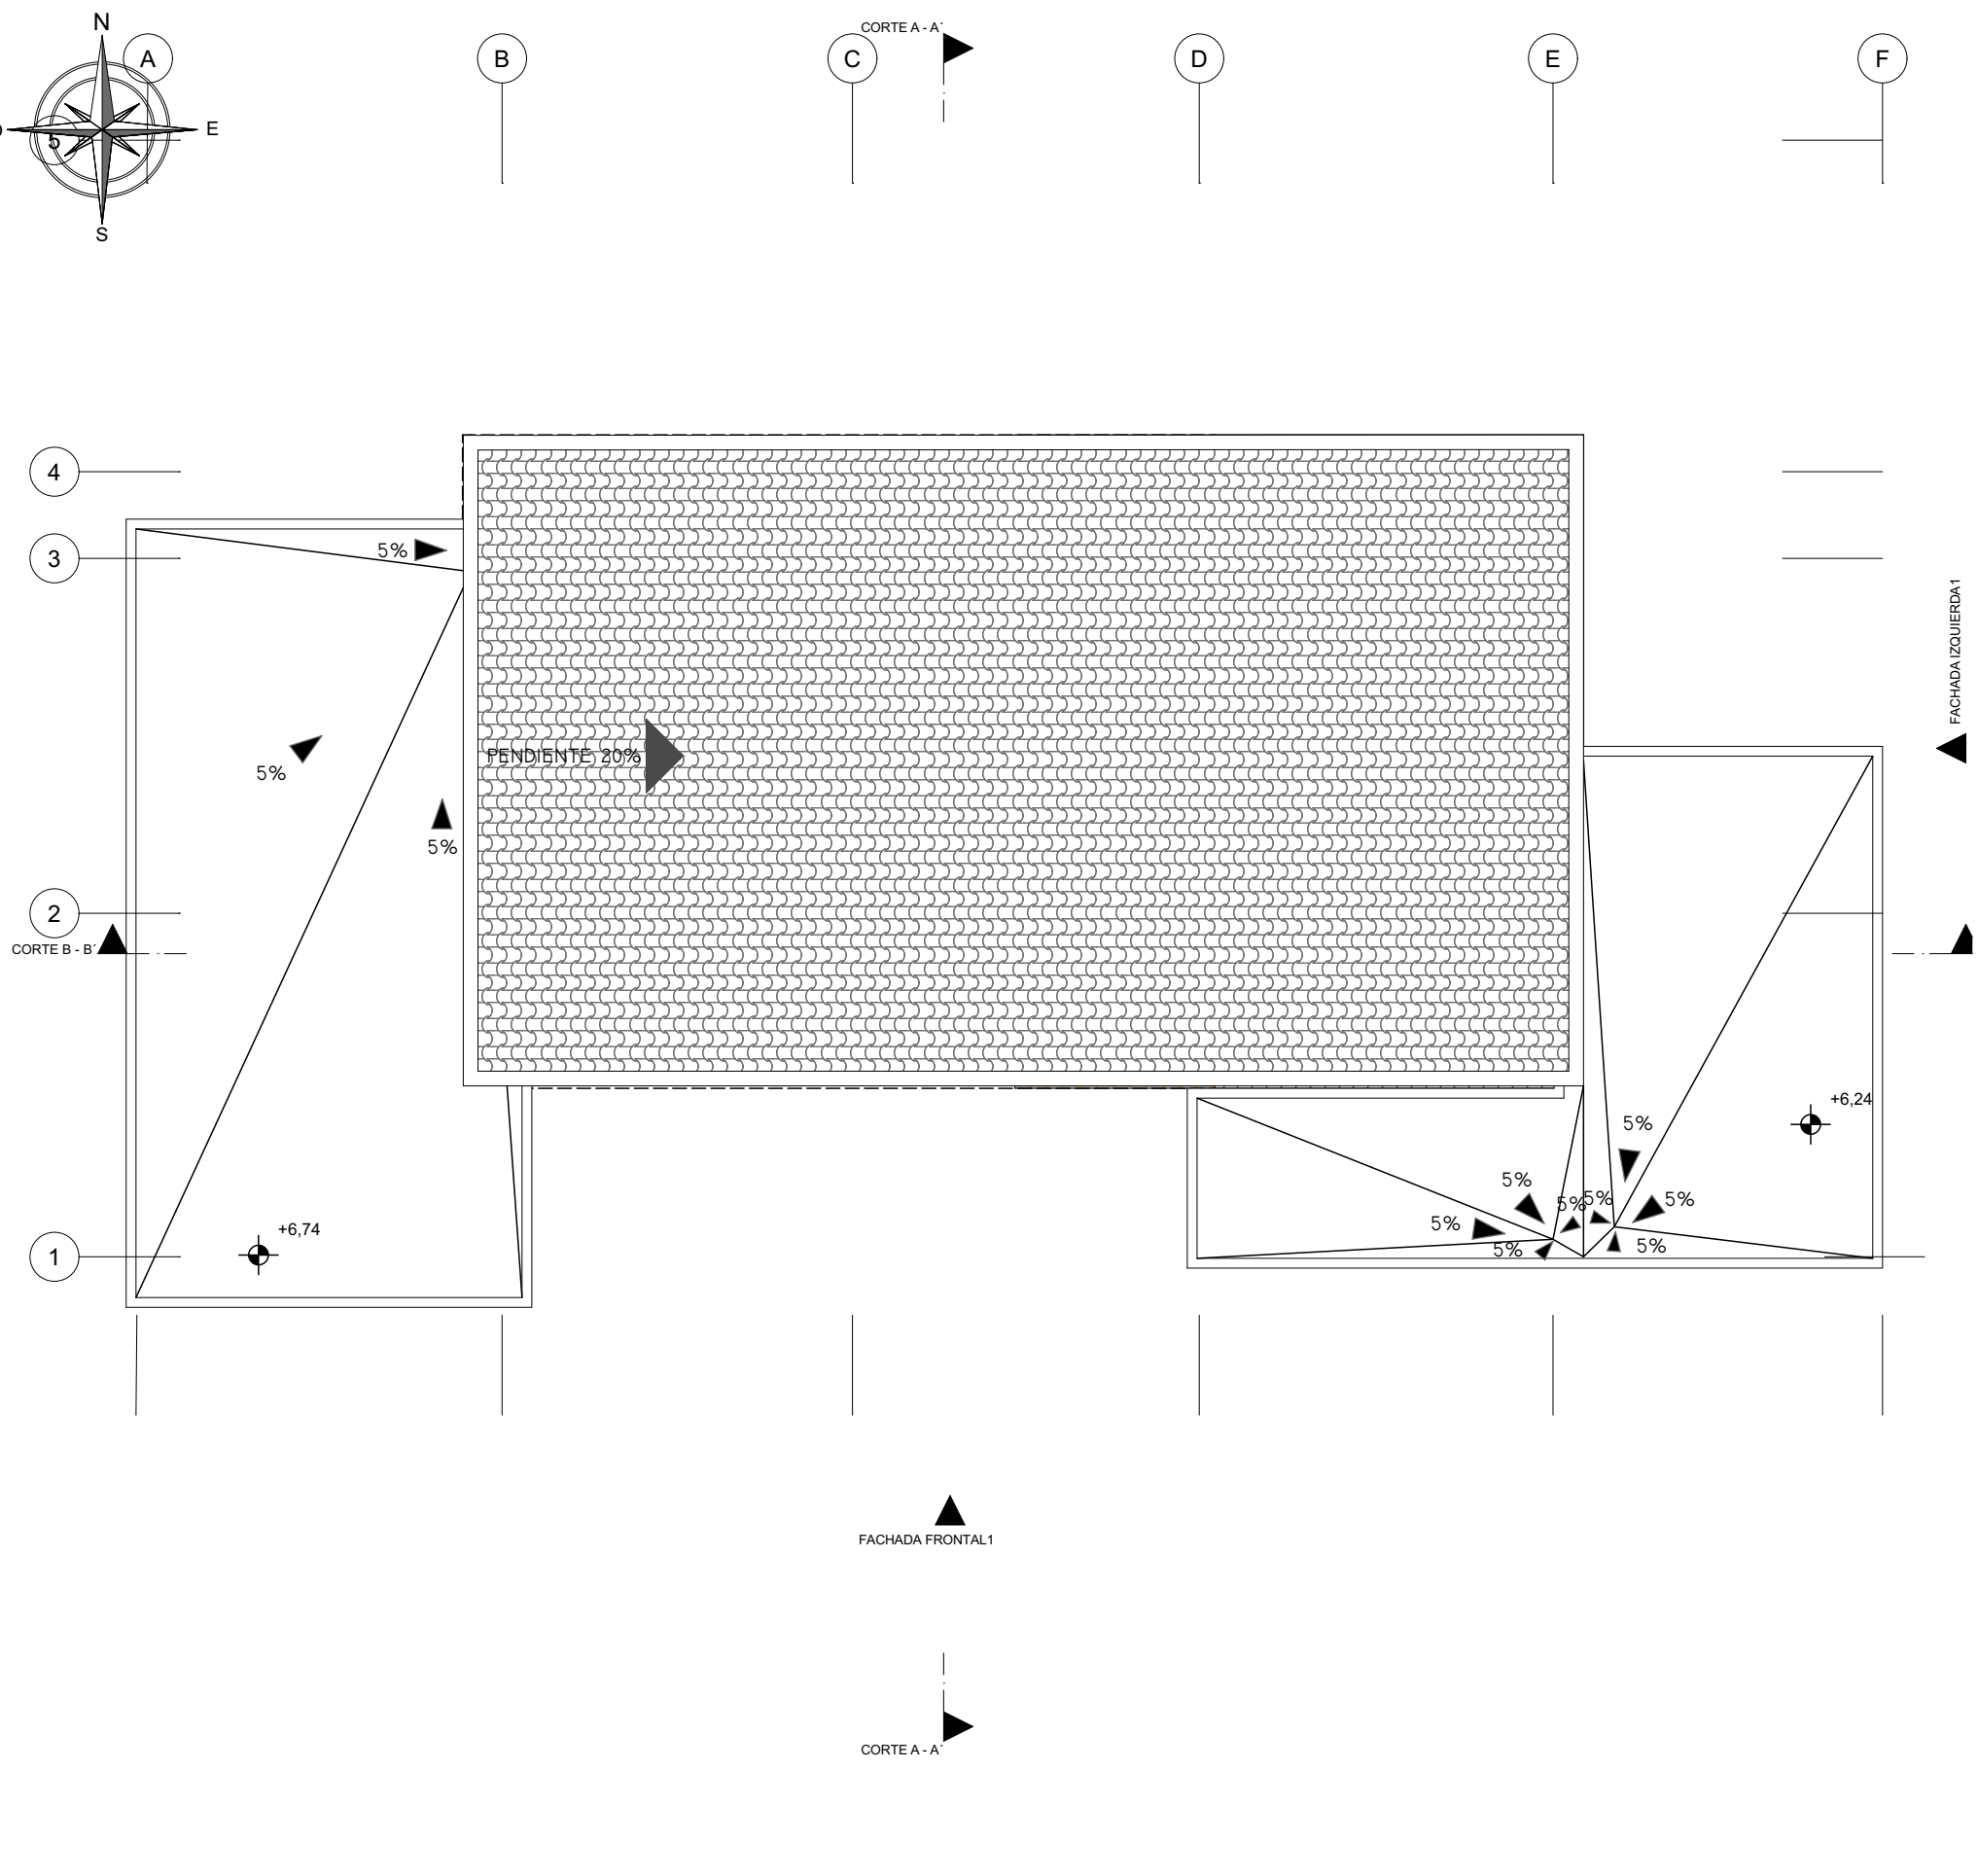

LOCALIZACIÓN

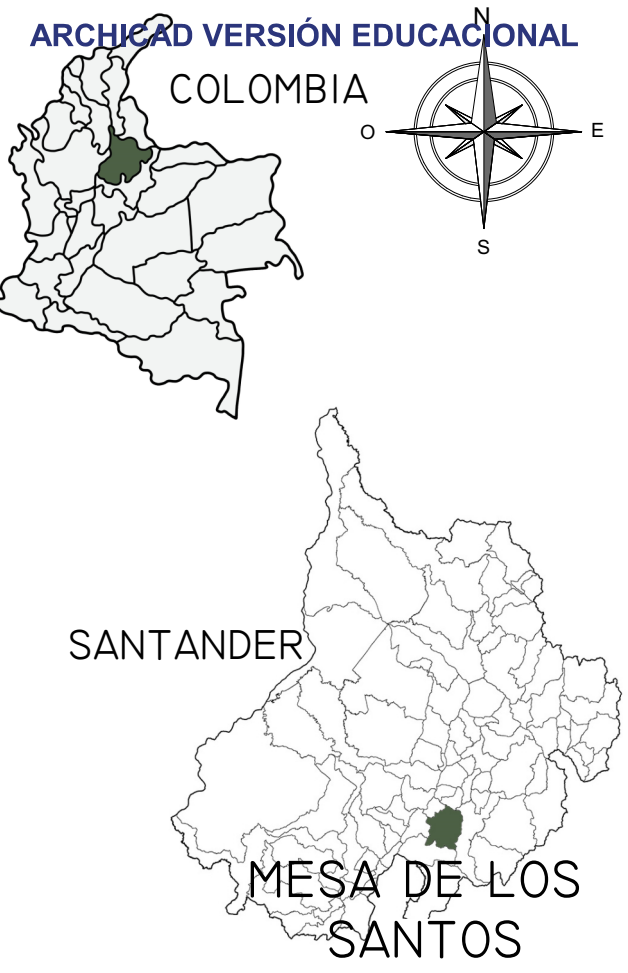


CUADRO DE ÁREAS	
ÁREA TOTAL DEL PREDIO	1332 M2
ÁREA CONSTRUIDA PISO 1	160 M2
ÁREA CONSTRUIDA PISO 2	120 M2
ÁREA TOTAL CONSTRUIDA	300 M2


FACHADA PRINCIPAL




CORTE A - A'

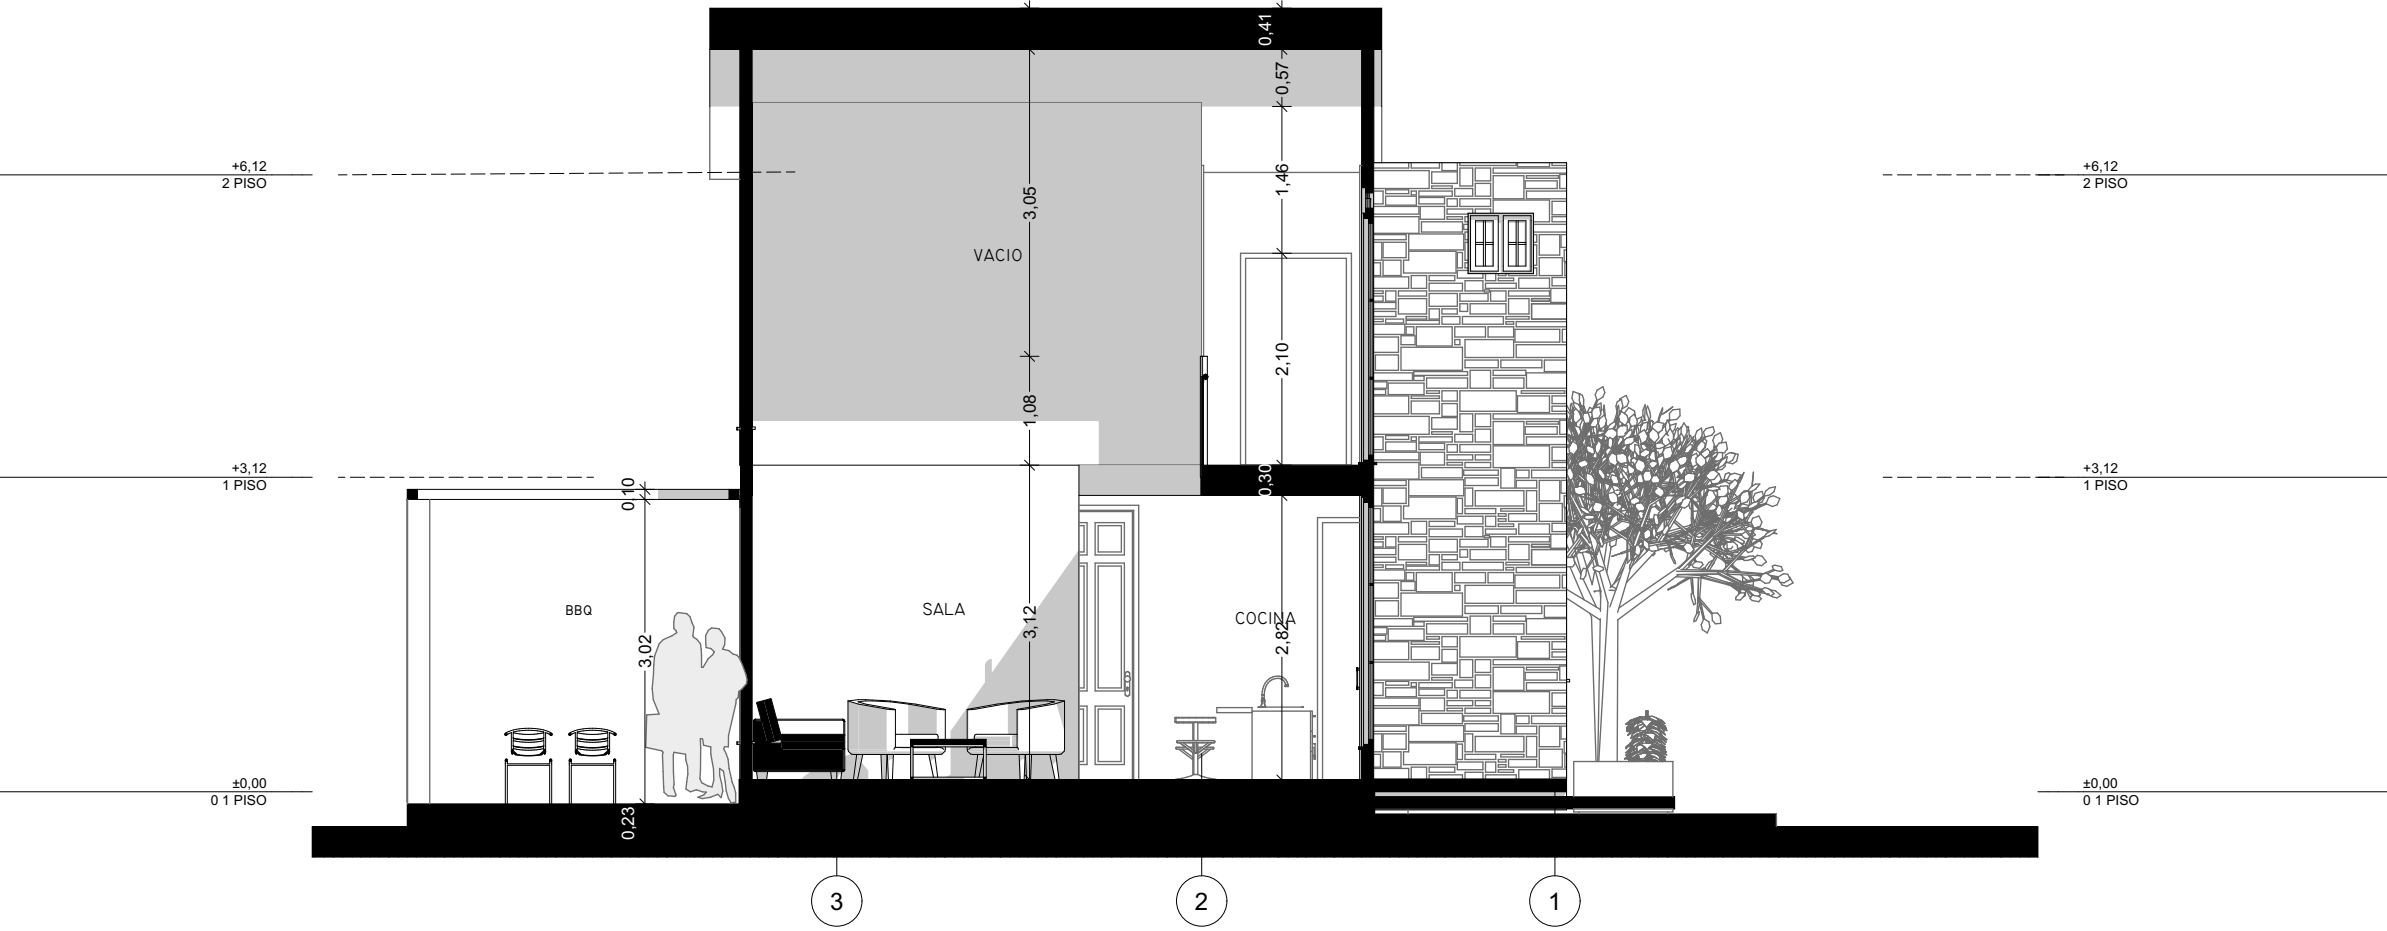

FACHADA LATERAL DERECHA

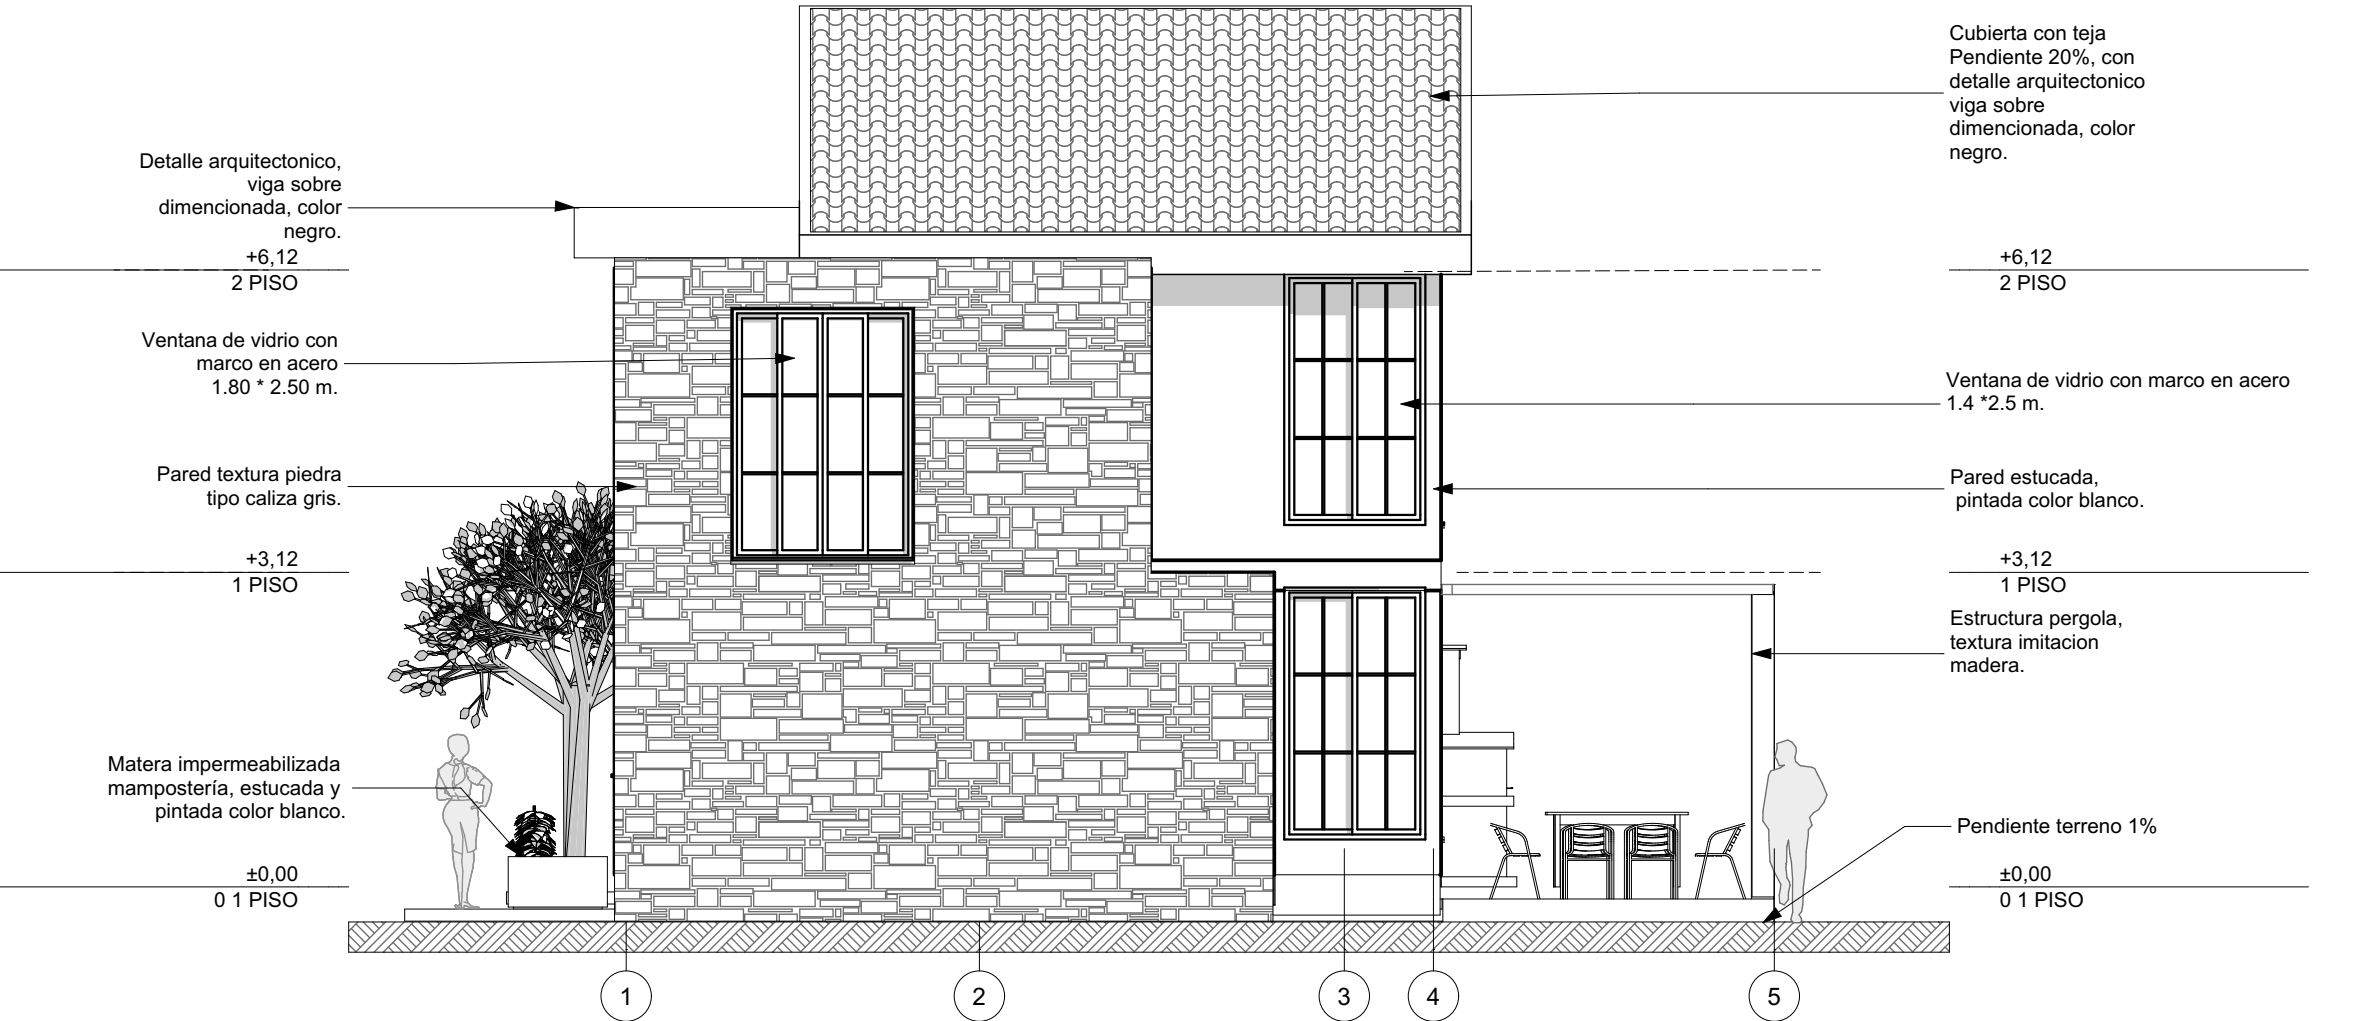

CORTE B - B'

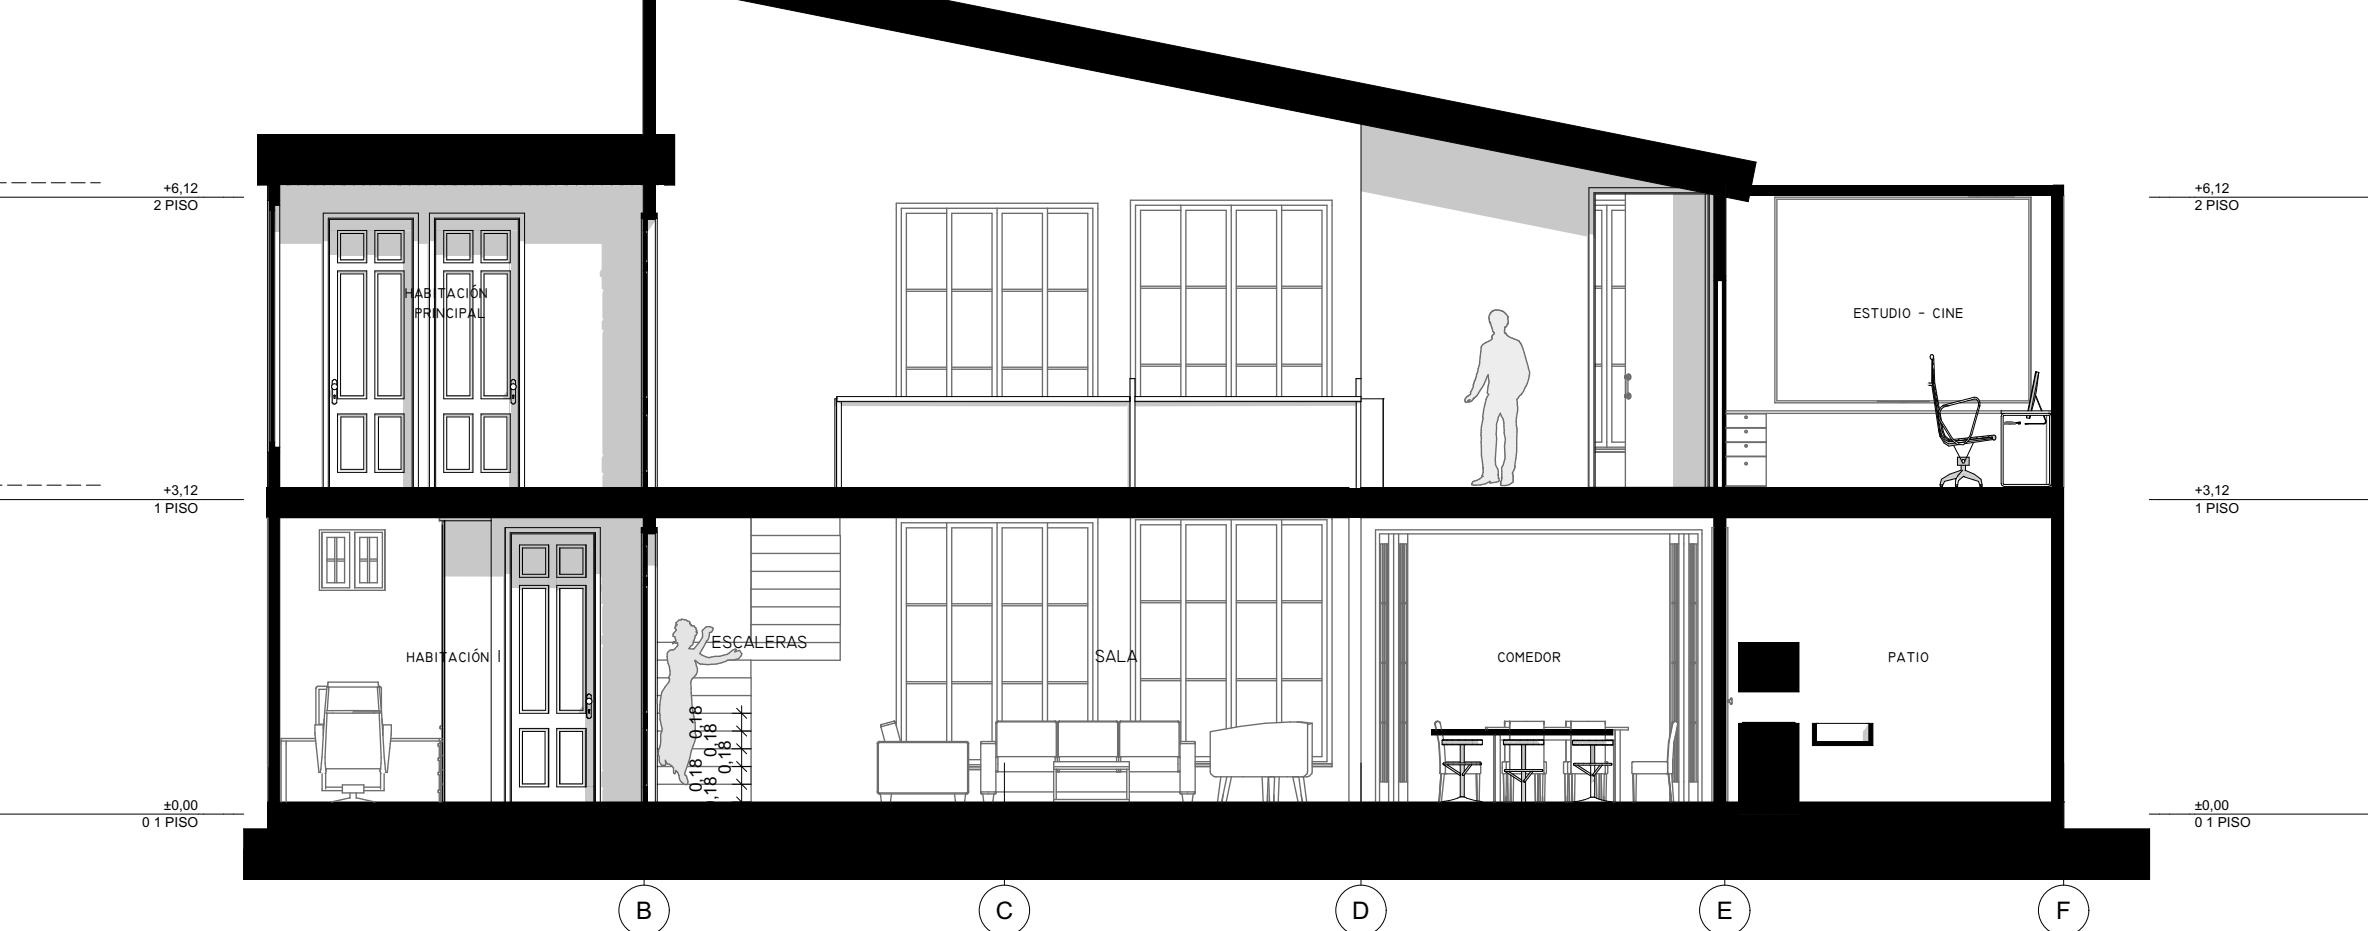

PROPIETARIOS:
CRISTIAN CORREA

DIRECCIÓN:
MESAS DE LOS SANTOS, SANTANDER

DISEÑO:

JESSICA VIVIANA RANGEL E.
ARQUITECTA - DISEÑADORA DE ESPACIOS INTERIORES
CEL. 311 720 48 49 - E-MAIL: RANGELJESSICAVIVIANA@GMAIL.COM
ARQ. JESSICA VIVIANA RANGEL ESPINOSA
M. A30632018-109873588

APROBÓ:

CONTIENE:
PLANTAS ARQUITECTÓNICAS, FACHADA
, CUADRO DE ÁREAS Y
LOCALIZACIÓN

TRAMITE:
CONSTRUCCIÓN NUEVA

FECHA:
MARZO 2026

ESCALA:
1:75

PLANO:
I DE I

OBSERVACIONES:
RECOMENDACIONES ESTRUCTURALES
- REVISAR PLANOS Y MEMORIA DE CALCULO ESTRUCTURAL.