





PLANTA PRIMER PISO

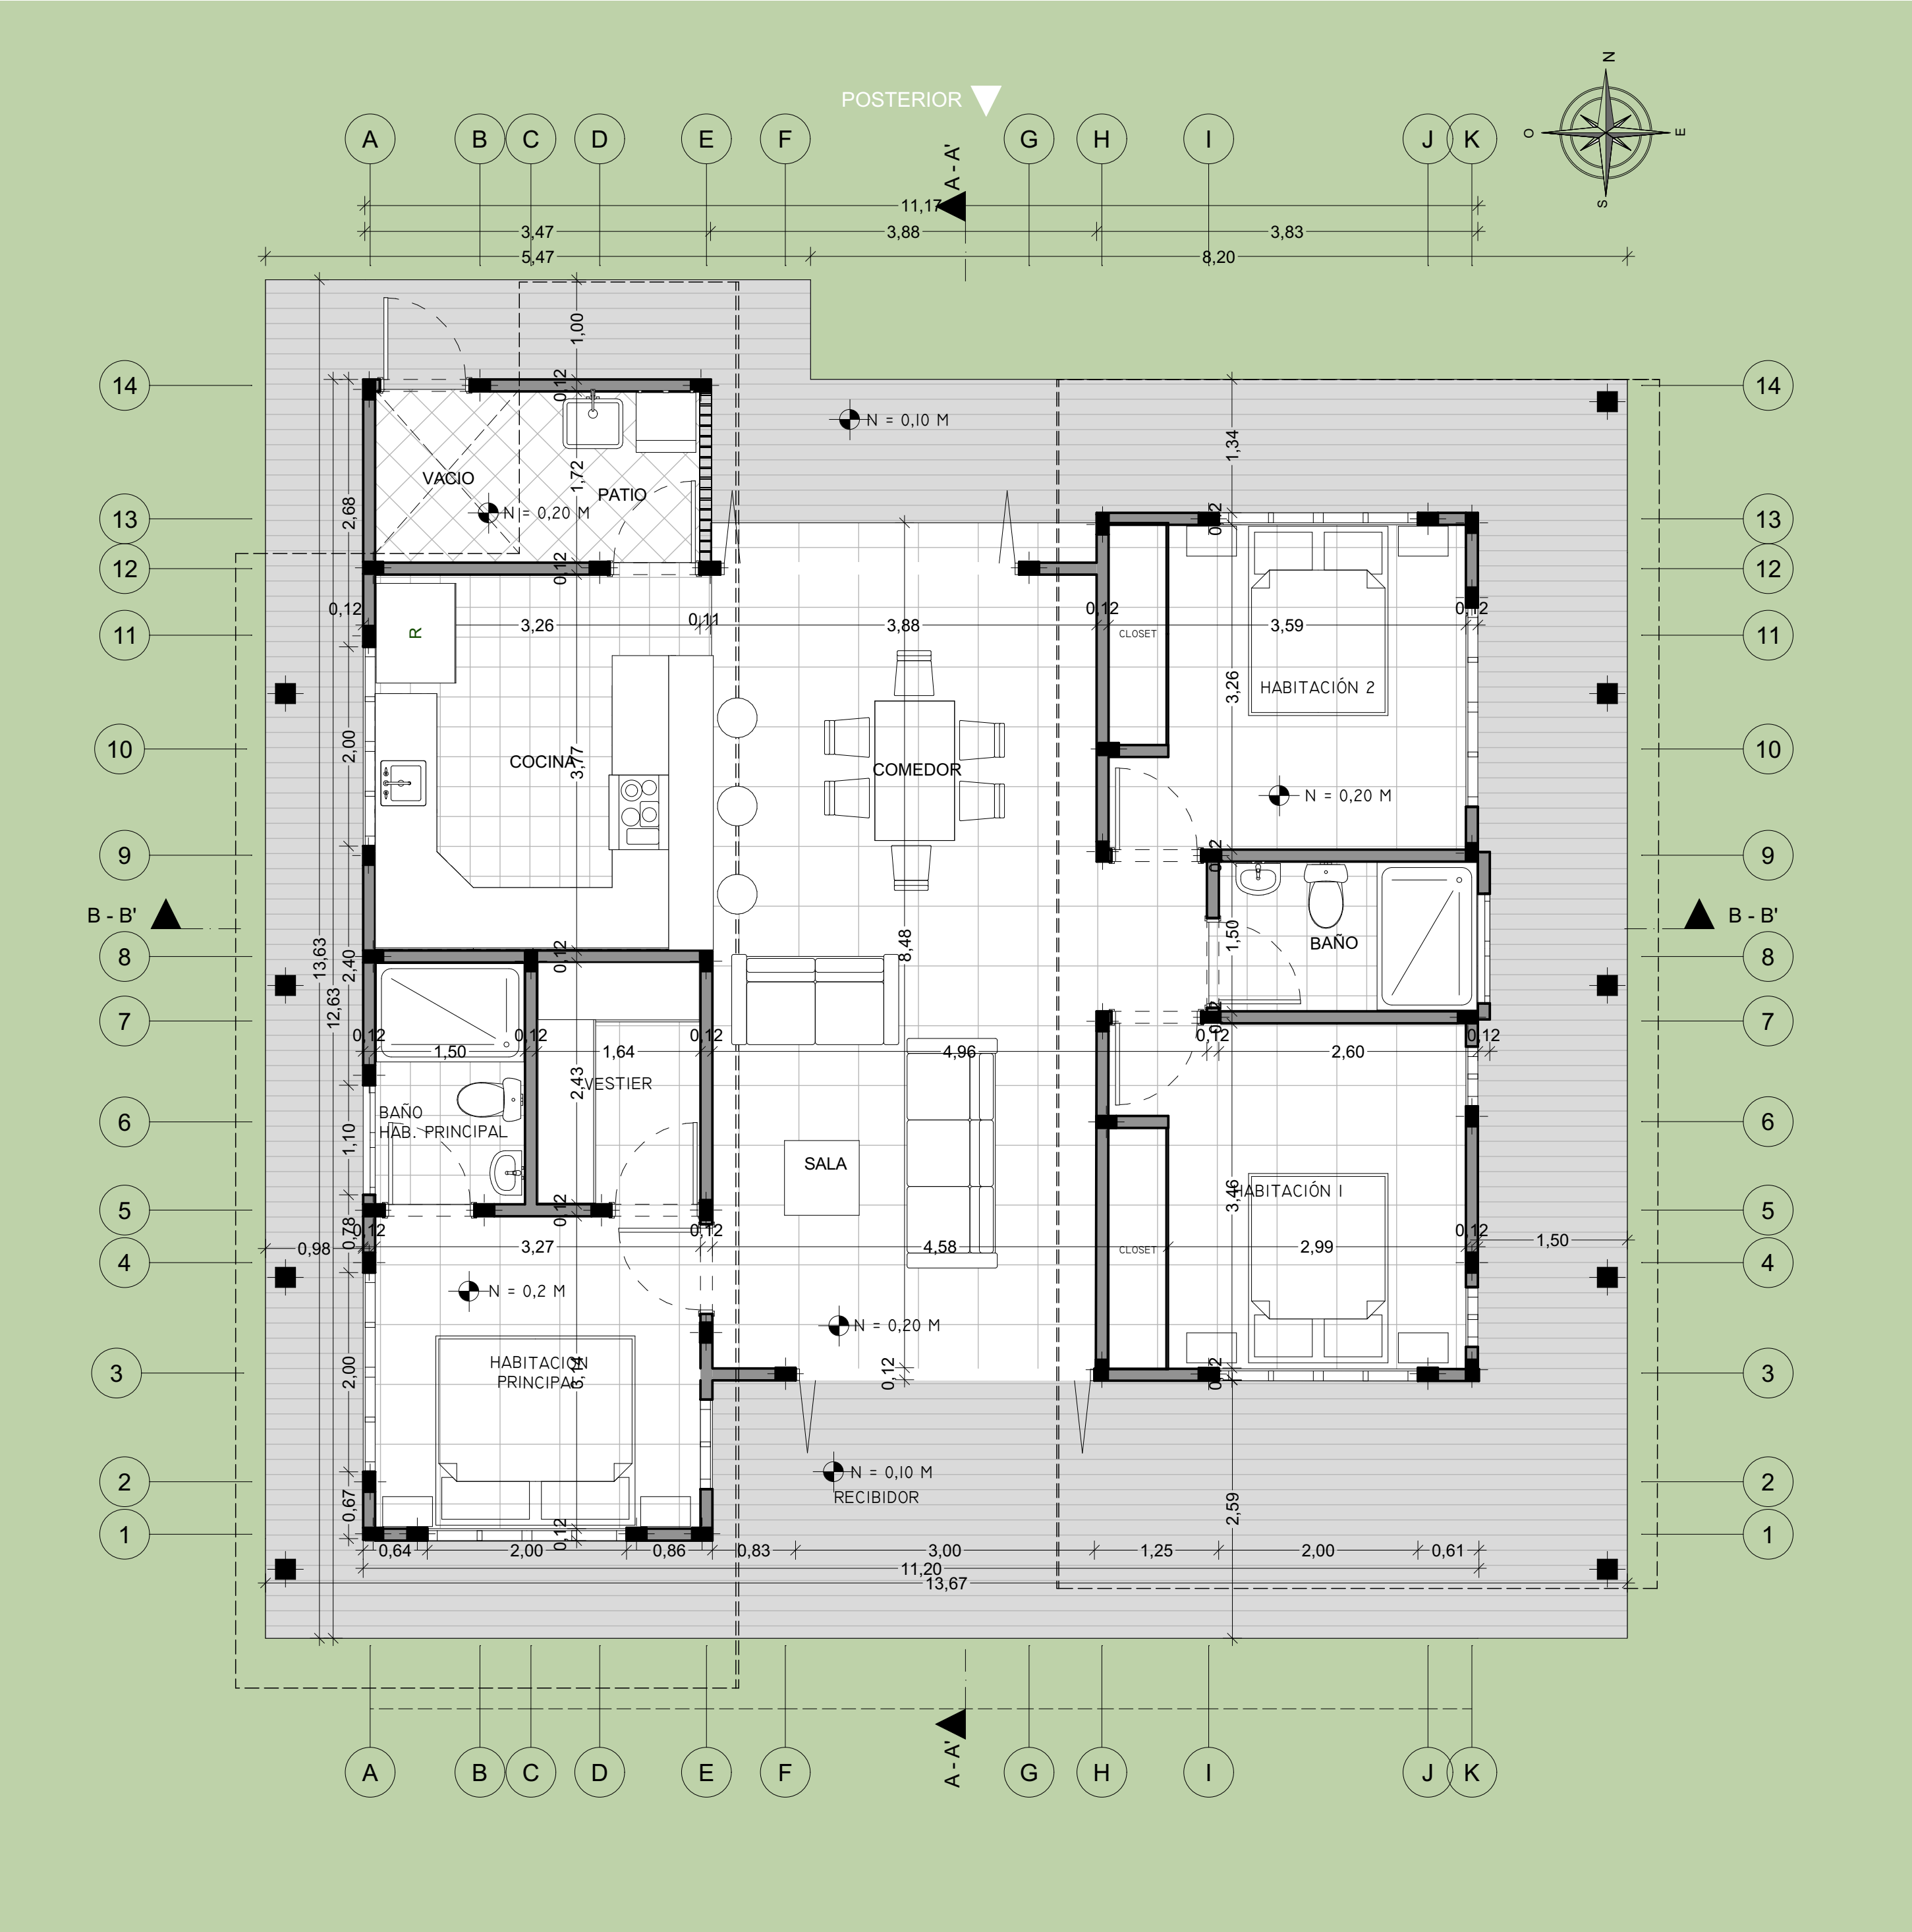


FACHADA PRINCIPAL

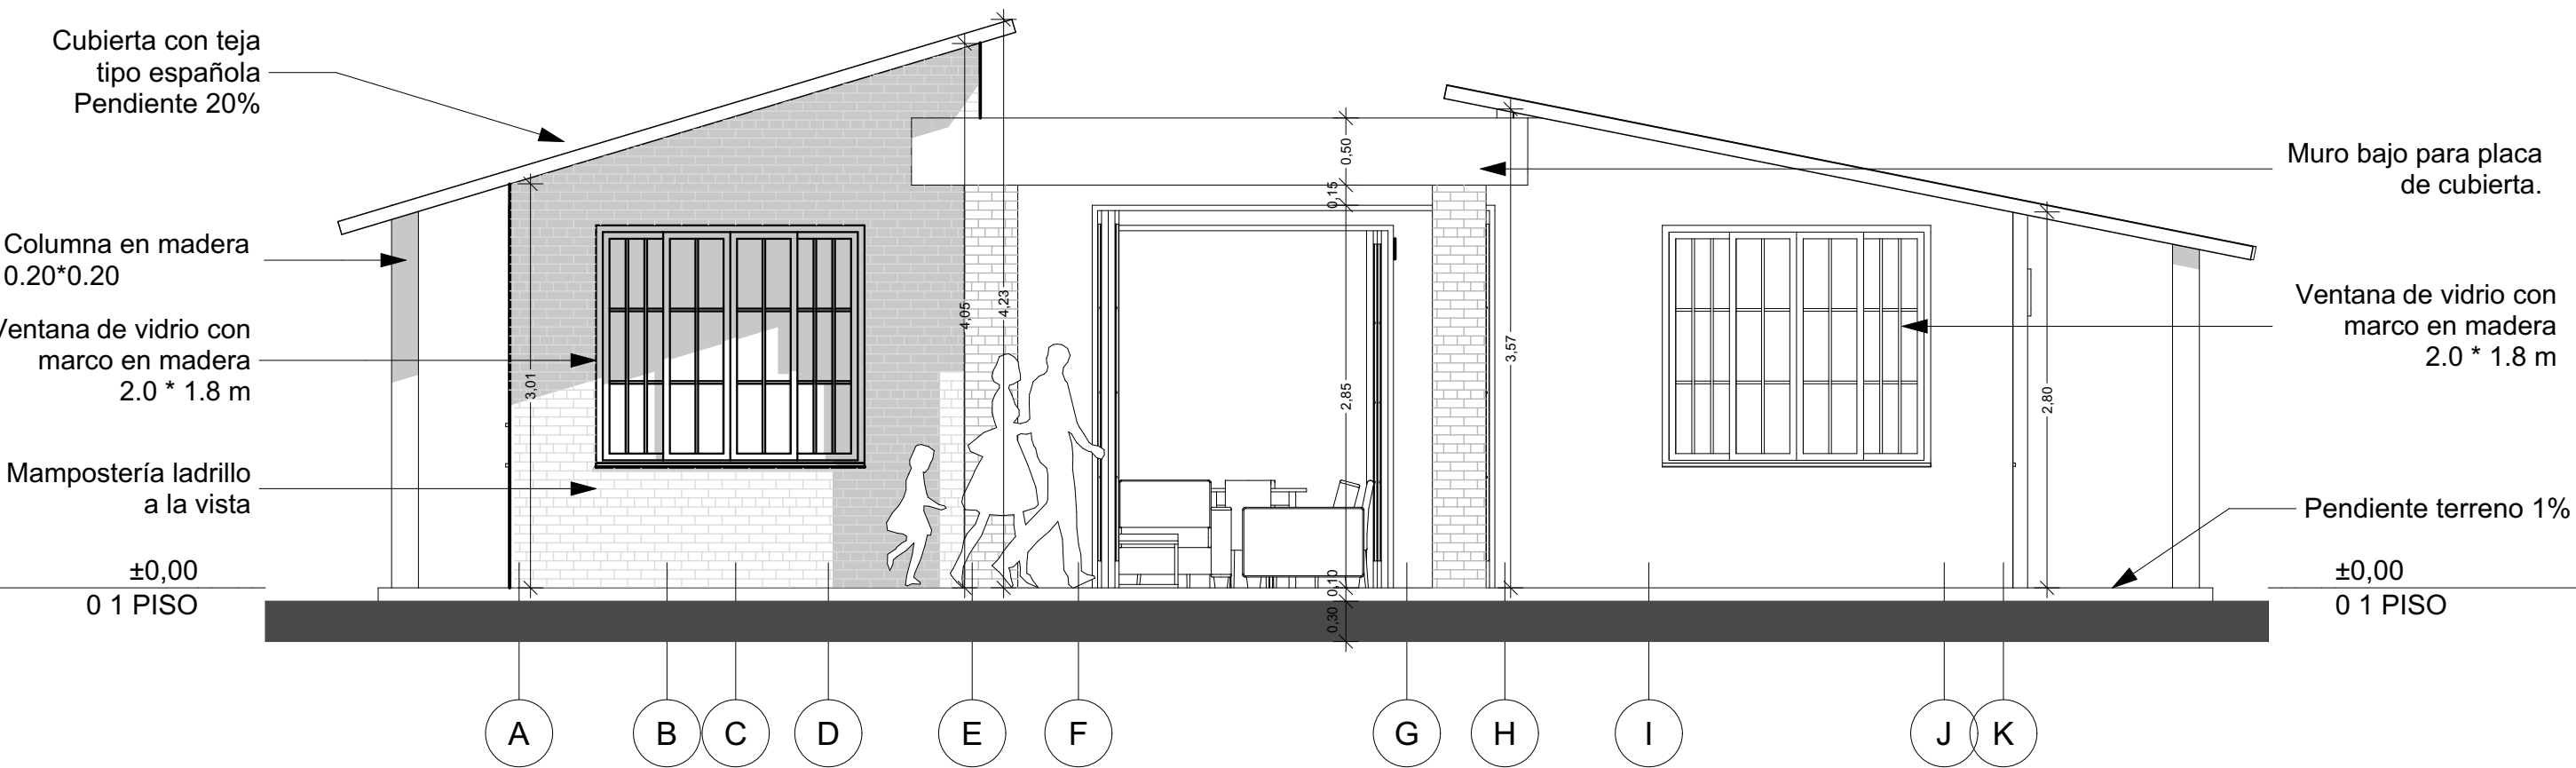

PLANTA DE CUBIERTA

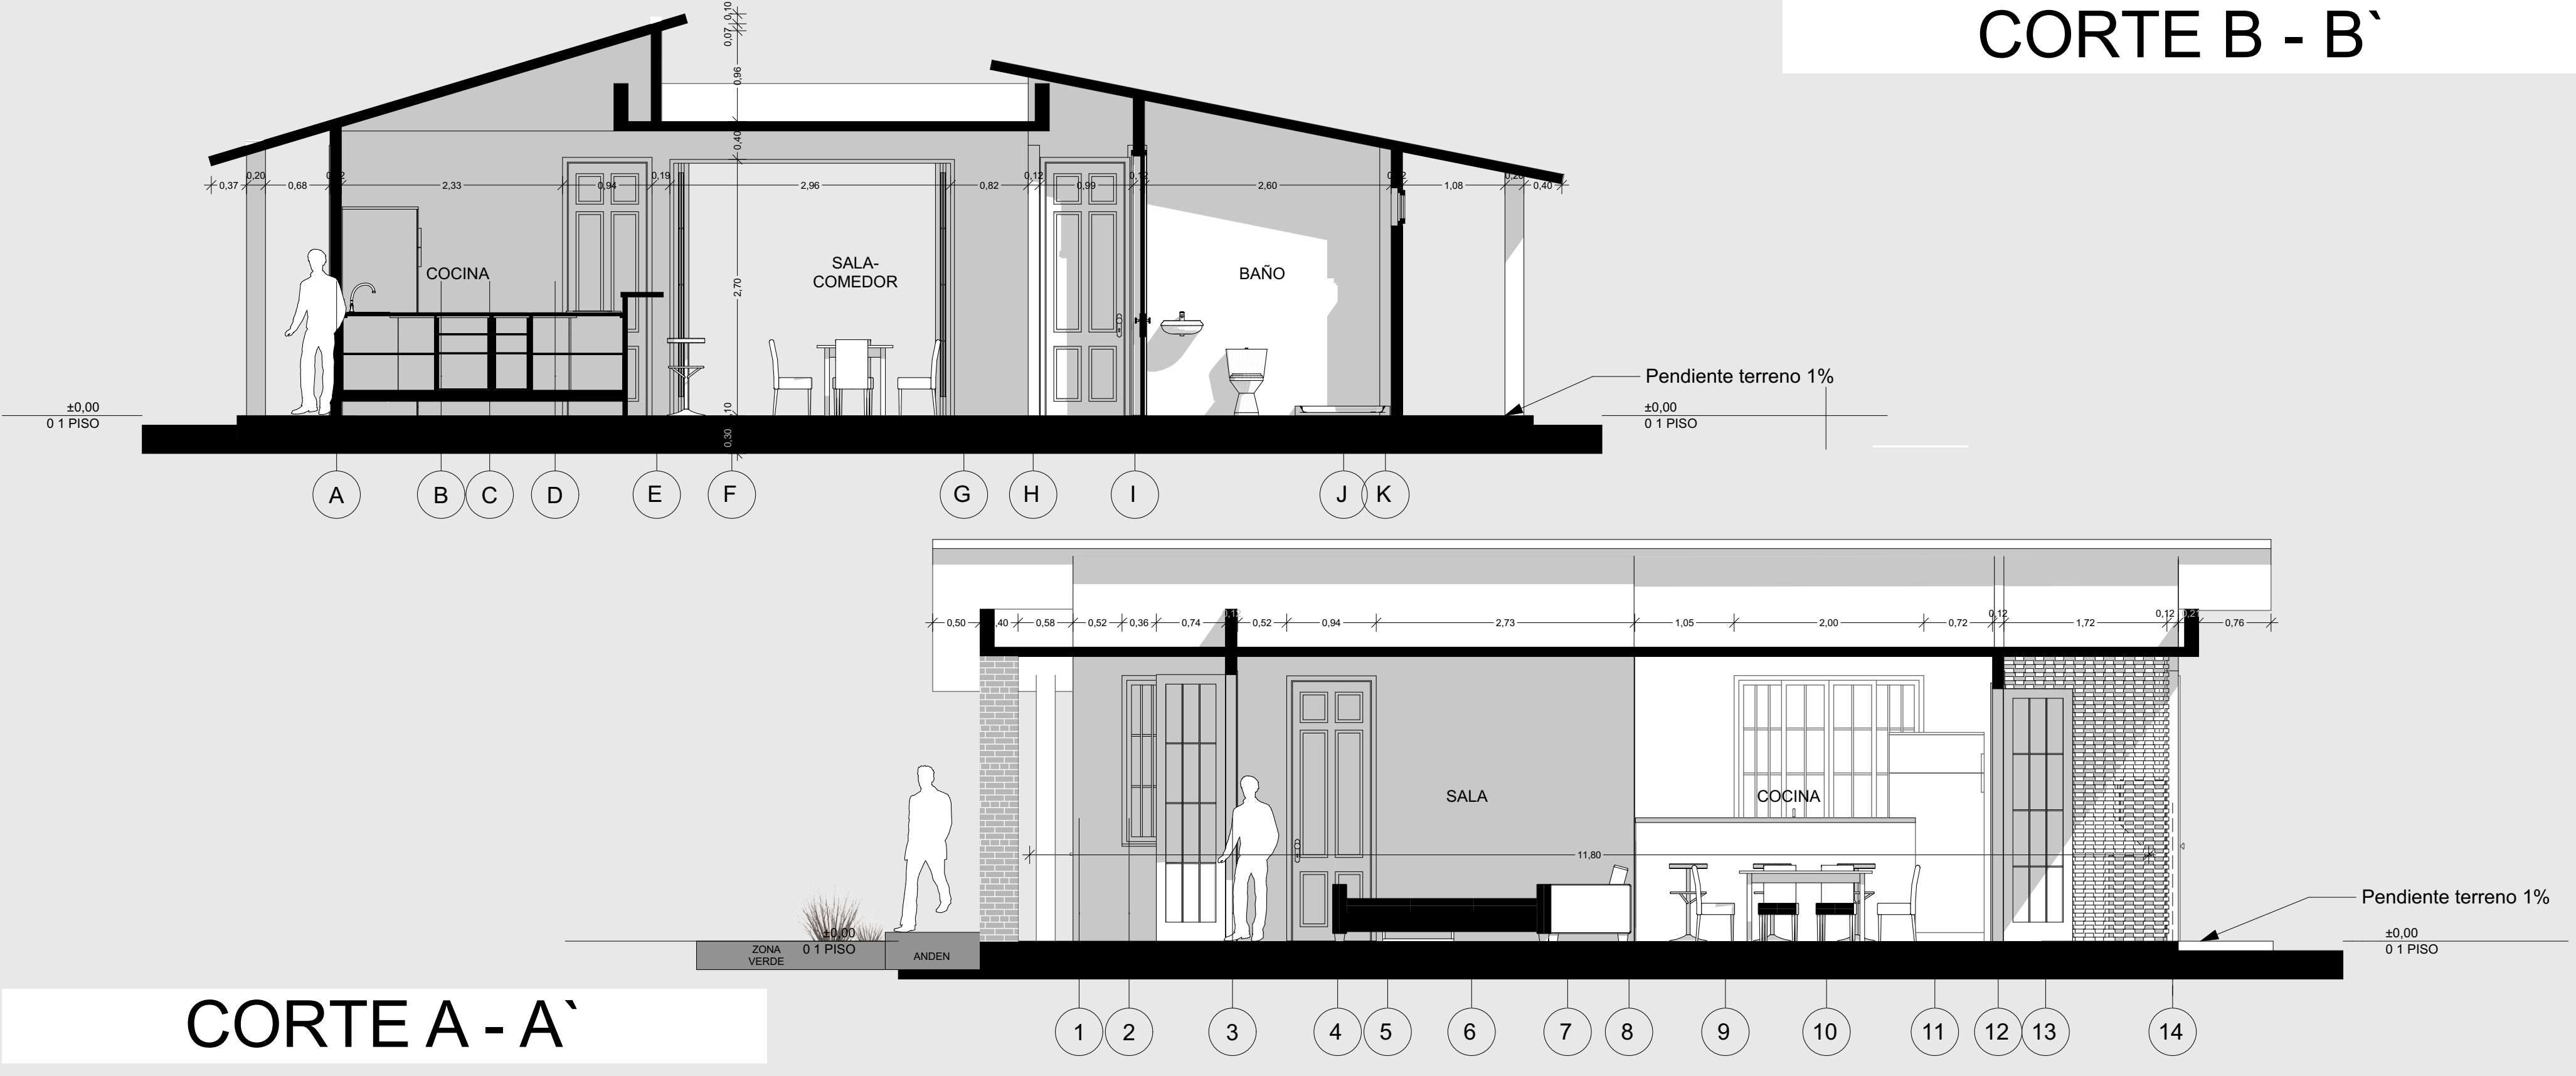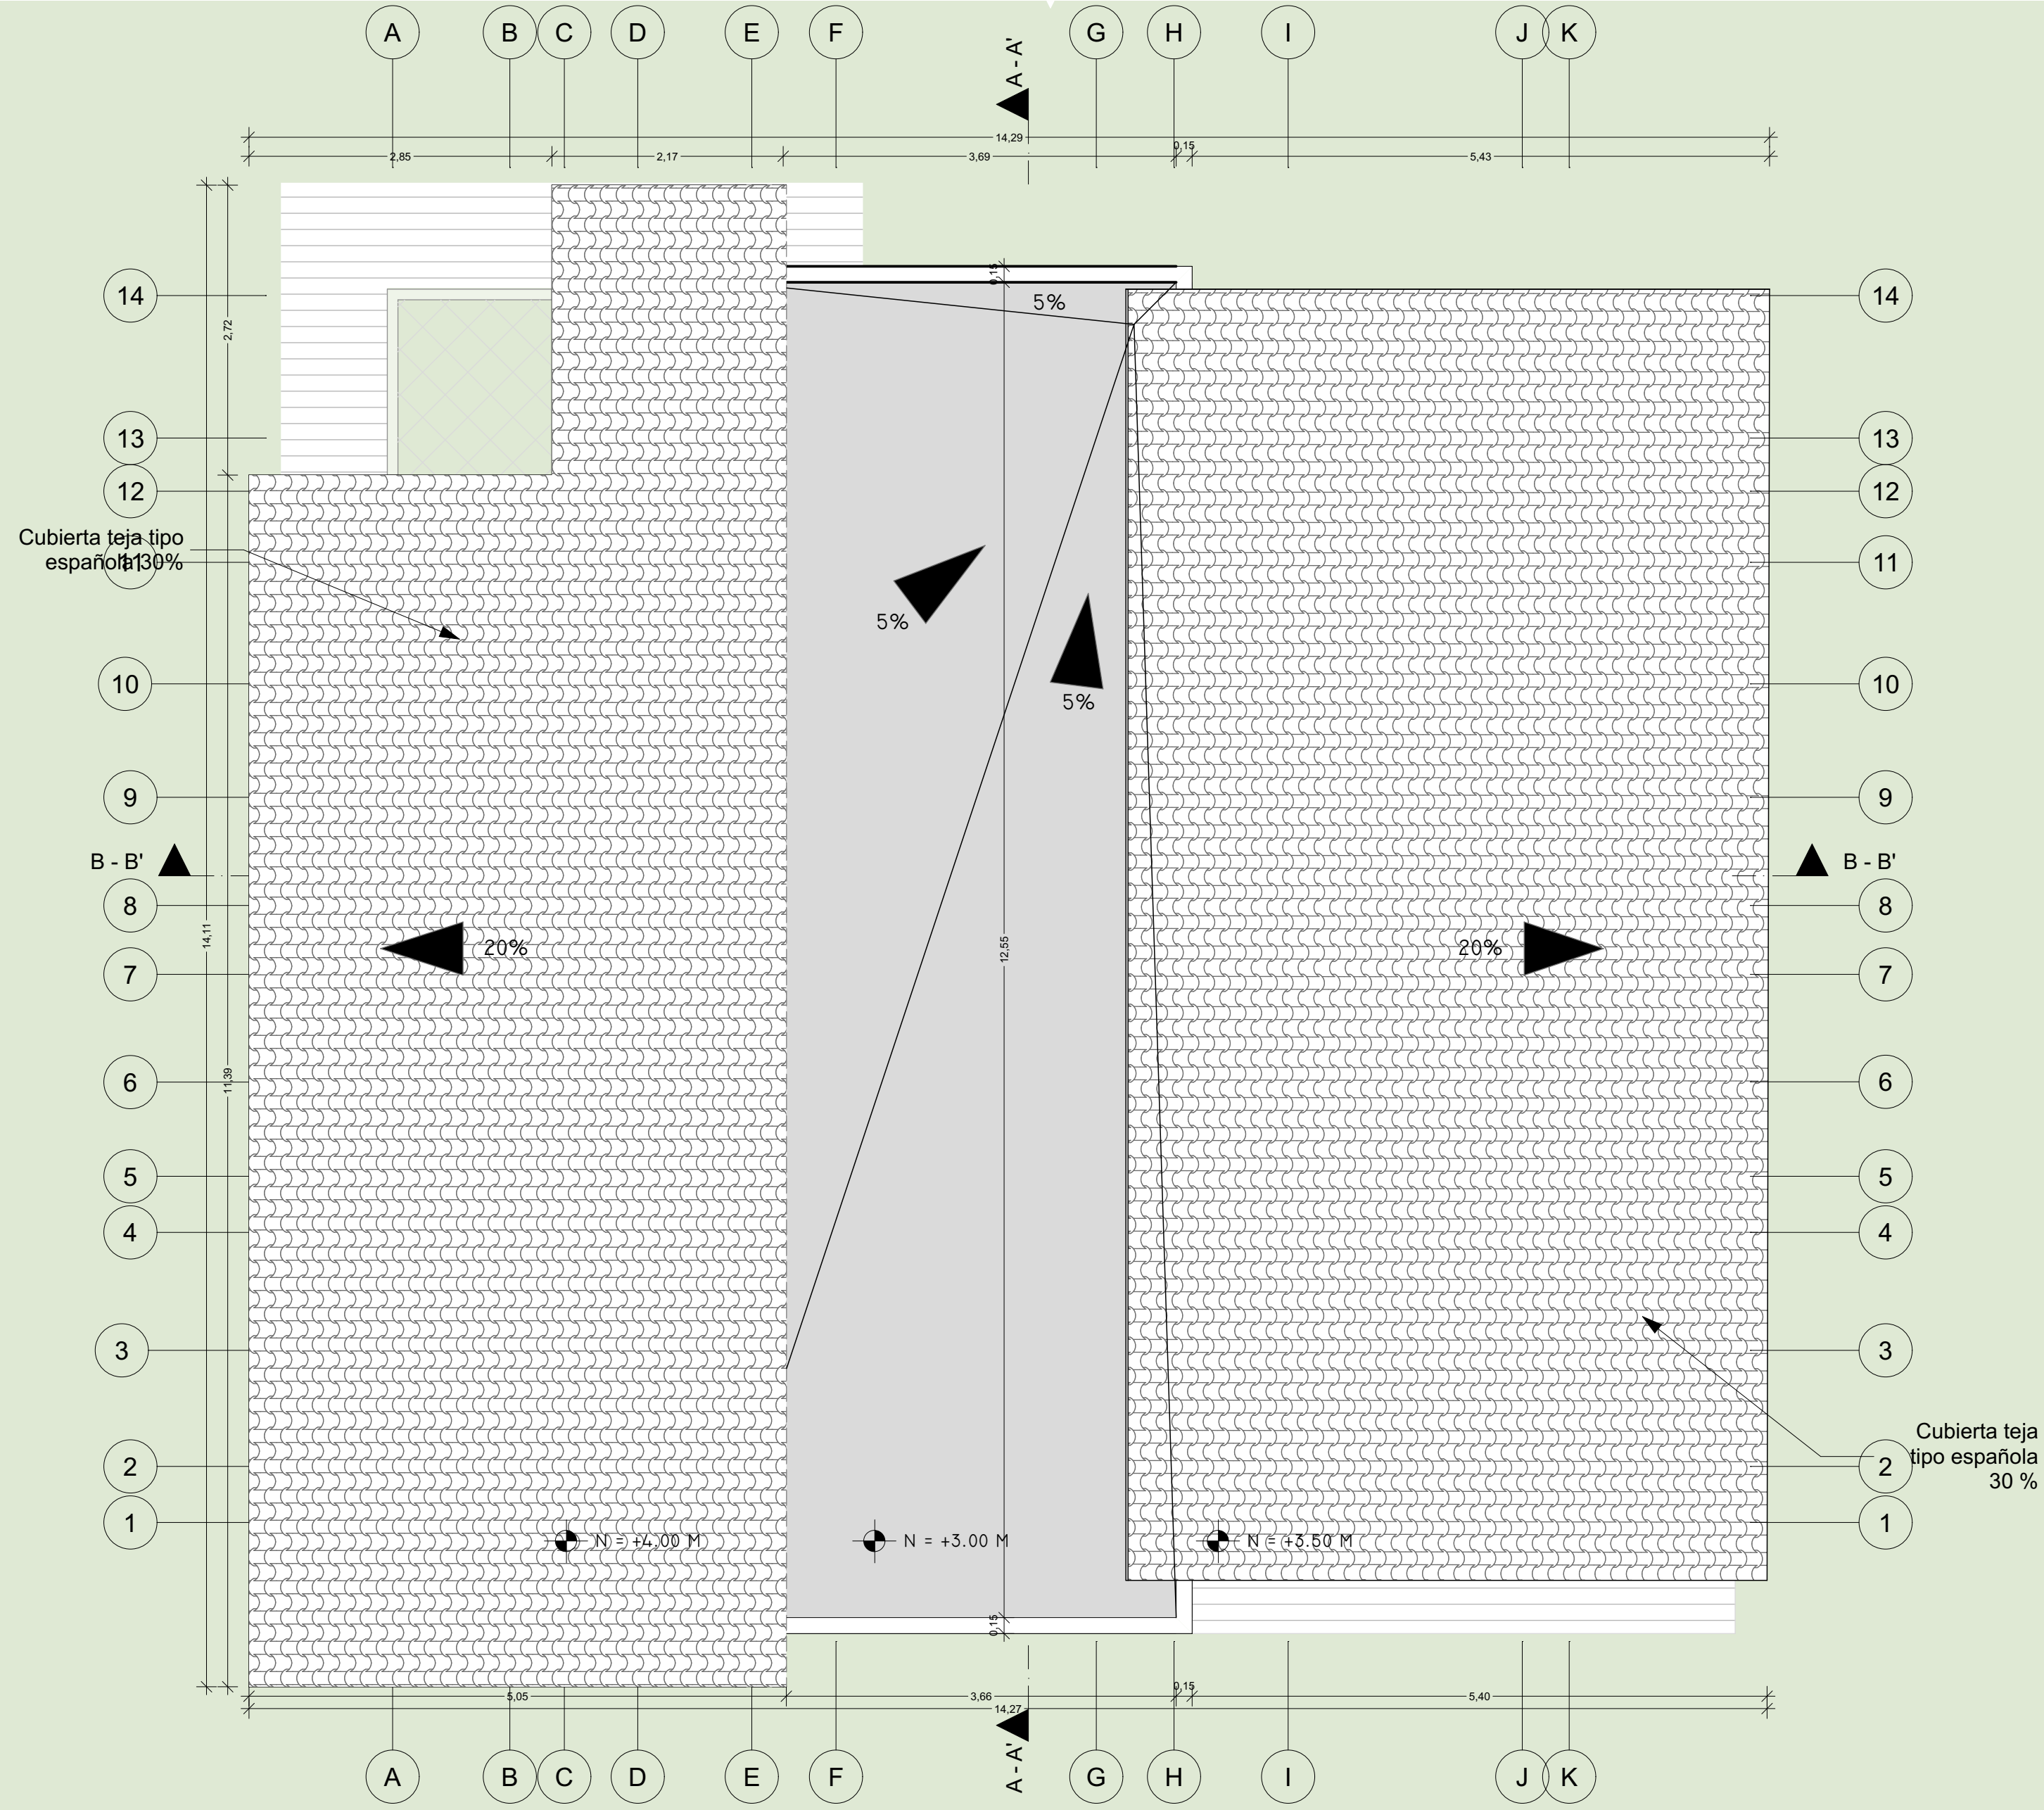

ARCHICAD VERSIÓN EDUCACIONAL

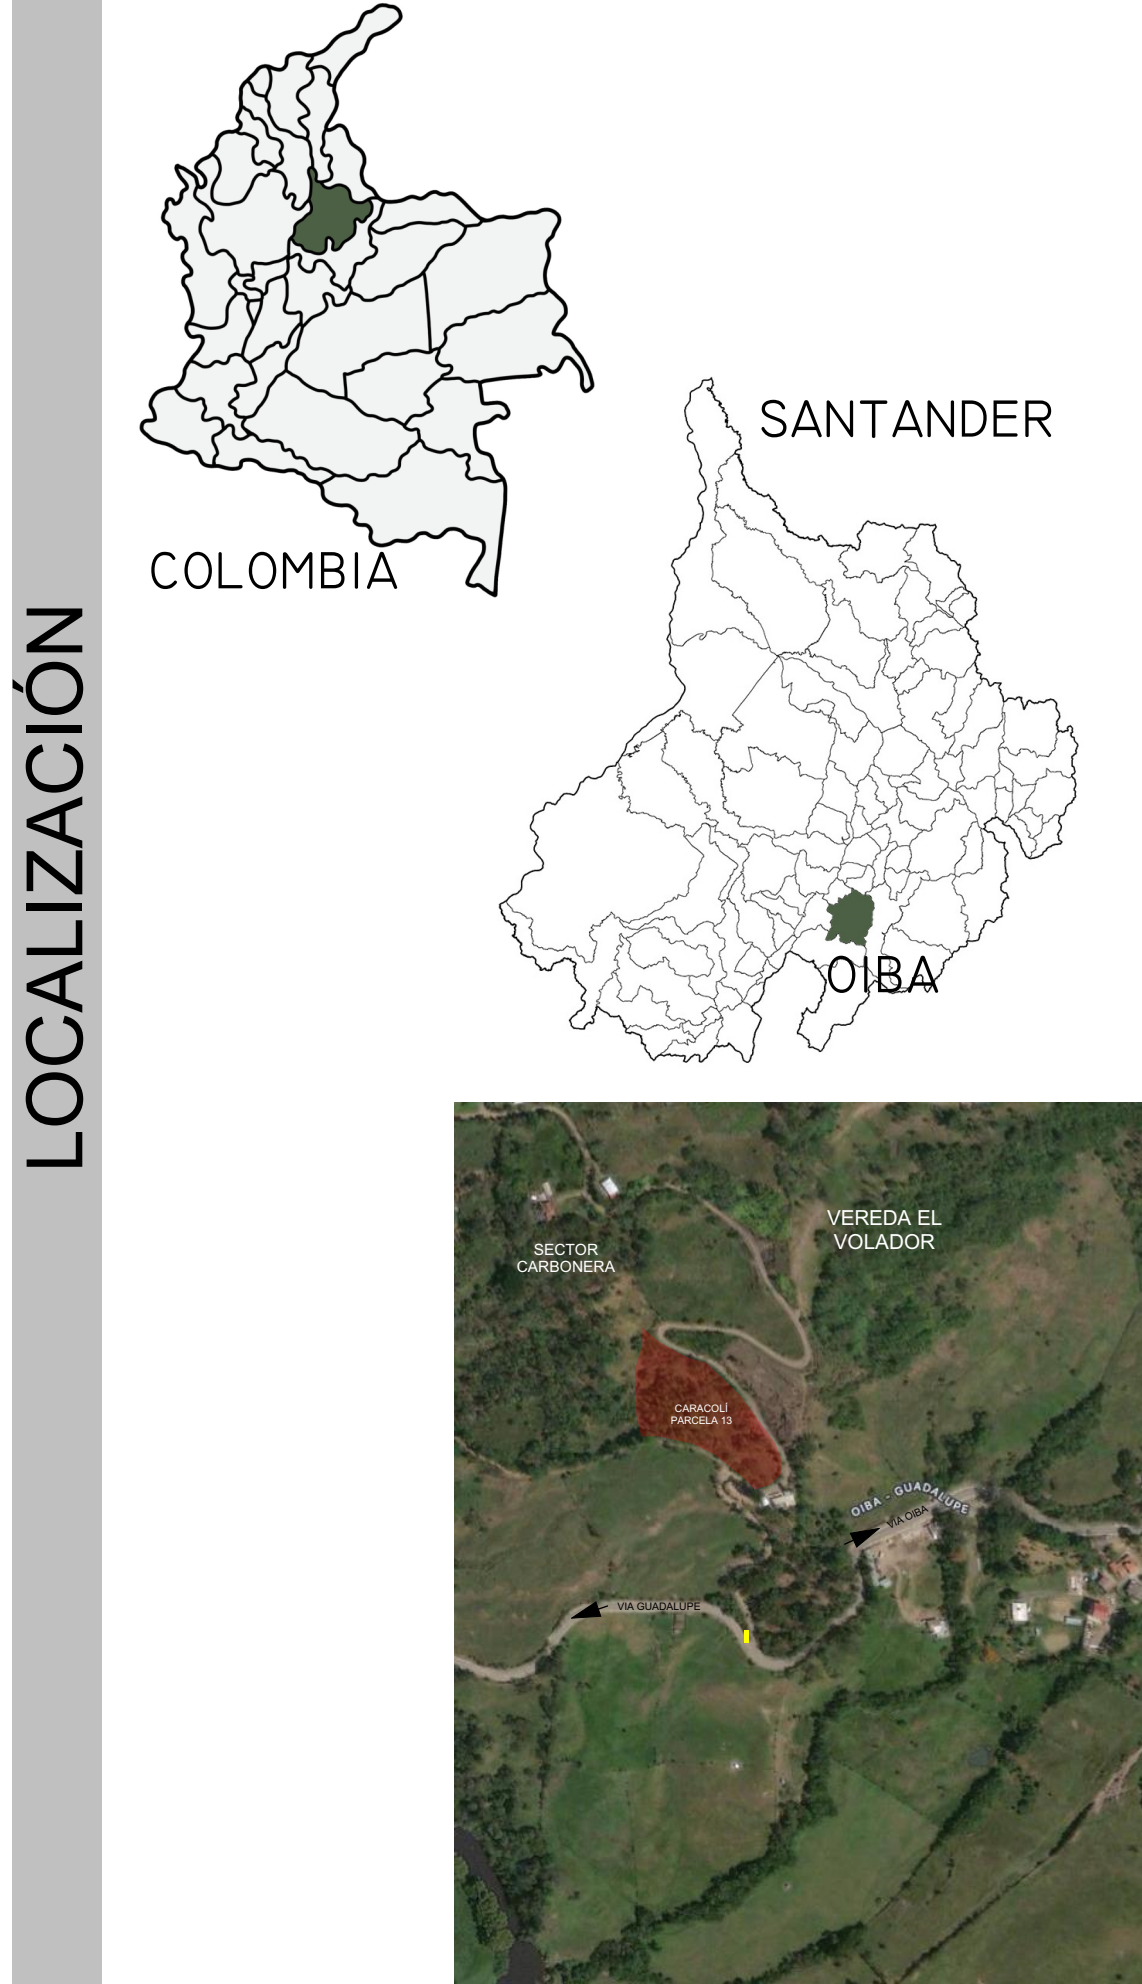

CUADRO DE AREAS	
ÁREA TOTAL DEL PREDIO	4 HAS 1130 M2
ÁREA CONSTRUIDA PISO 1	106 M2
ÁREA TOTAL CONSTRUIDA	106 M2

CORTE B - B'

CORTE A - A'

PROPIETARIOS:
LUZ MARINA BLANCO
MARIA ISABEL PINTO BLANCO

DIRECCIÓN:
CARACOLI PARCELA 13
OIBA, SANTANDER

ESPECI COL
CONSTRUCCIONES

JESSICA VIVIANA RANGEL E.
ARQUITECTA - DISEÑADORA DE ESPACIOS INTERIORES

DISEÑÓ:
ARQ. JESSICA VIVIANA RANGEL ESPINOSA
M. A30632018-I09873588

APROBÓ:

CONTIENE:
PLANTAS ARQUITECTÓNICAS, CORTES,
FACHADA, CUADRO DE ÁREAS Y
LOCALIZACIÓN

TRAMITE:
LICENCIA DE CONSTRUCCIÓN NUEVA

FECHA
OCTUBRE 2024

ESCALA
1:50

PLANO
I DE I

OBSERVACIONES