

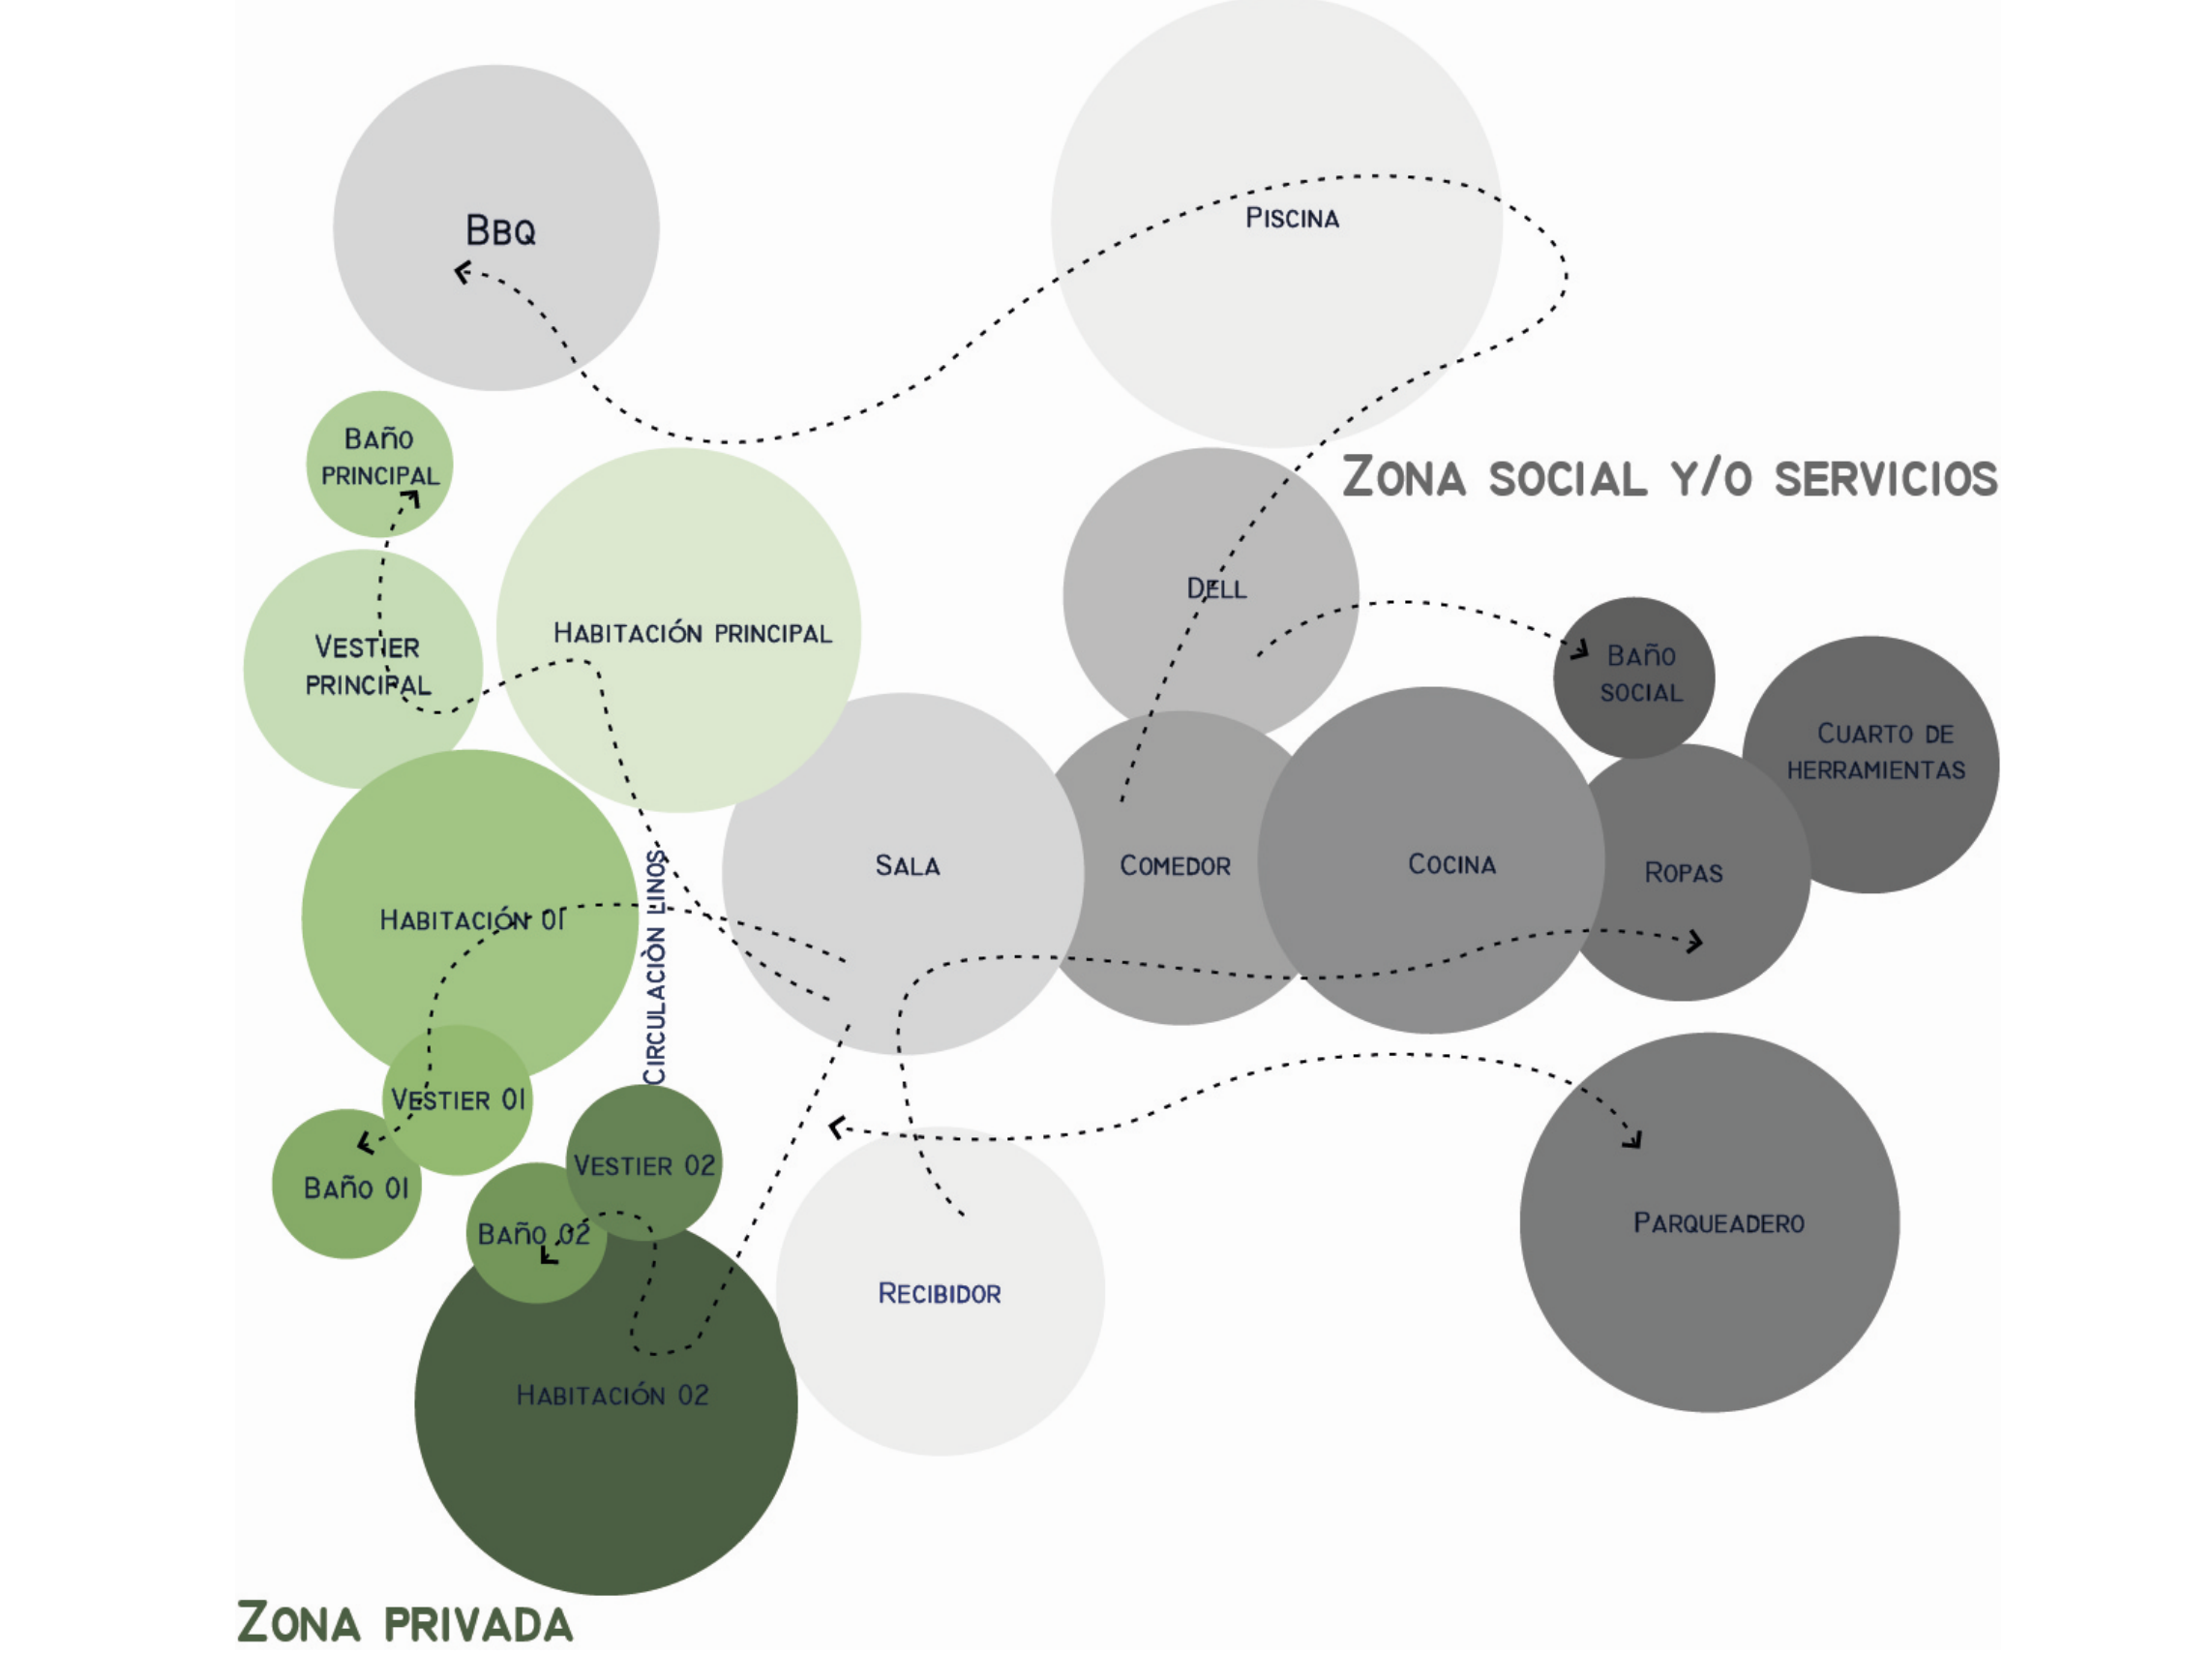


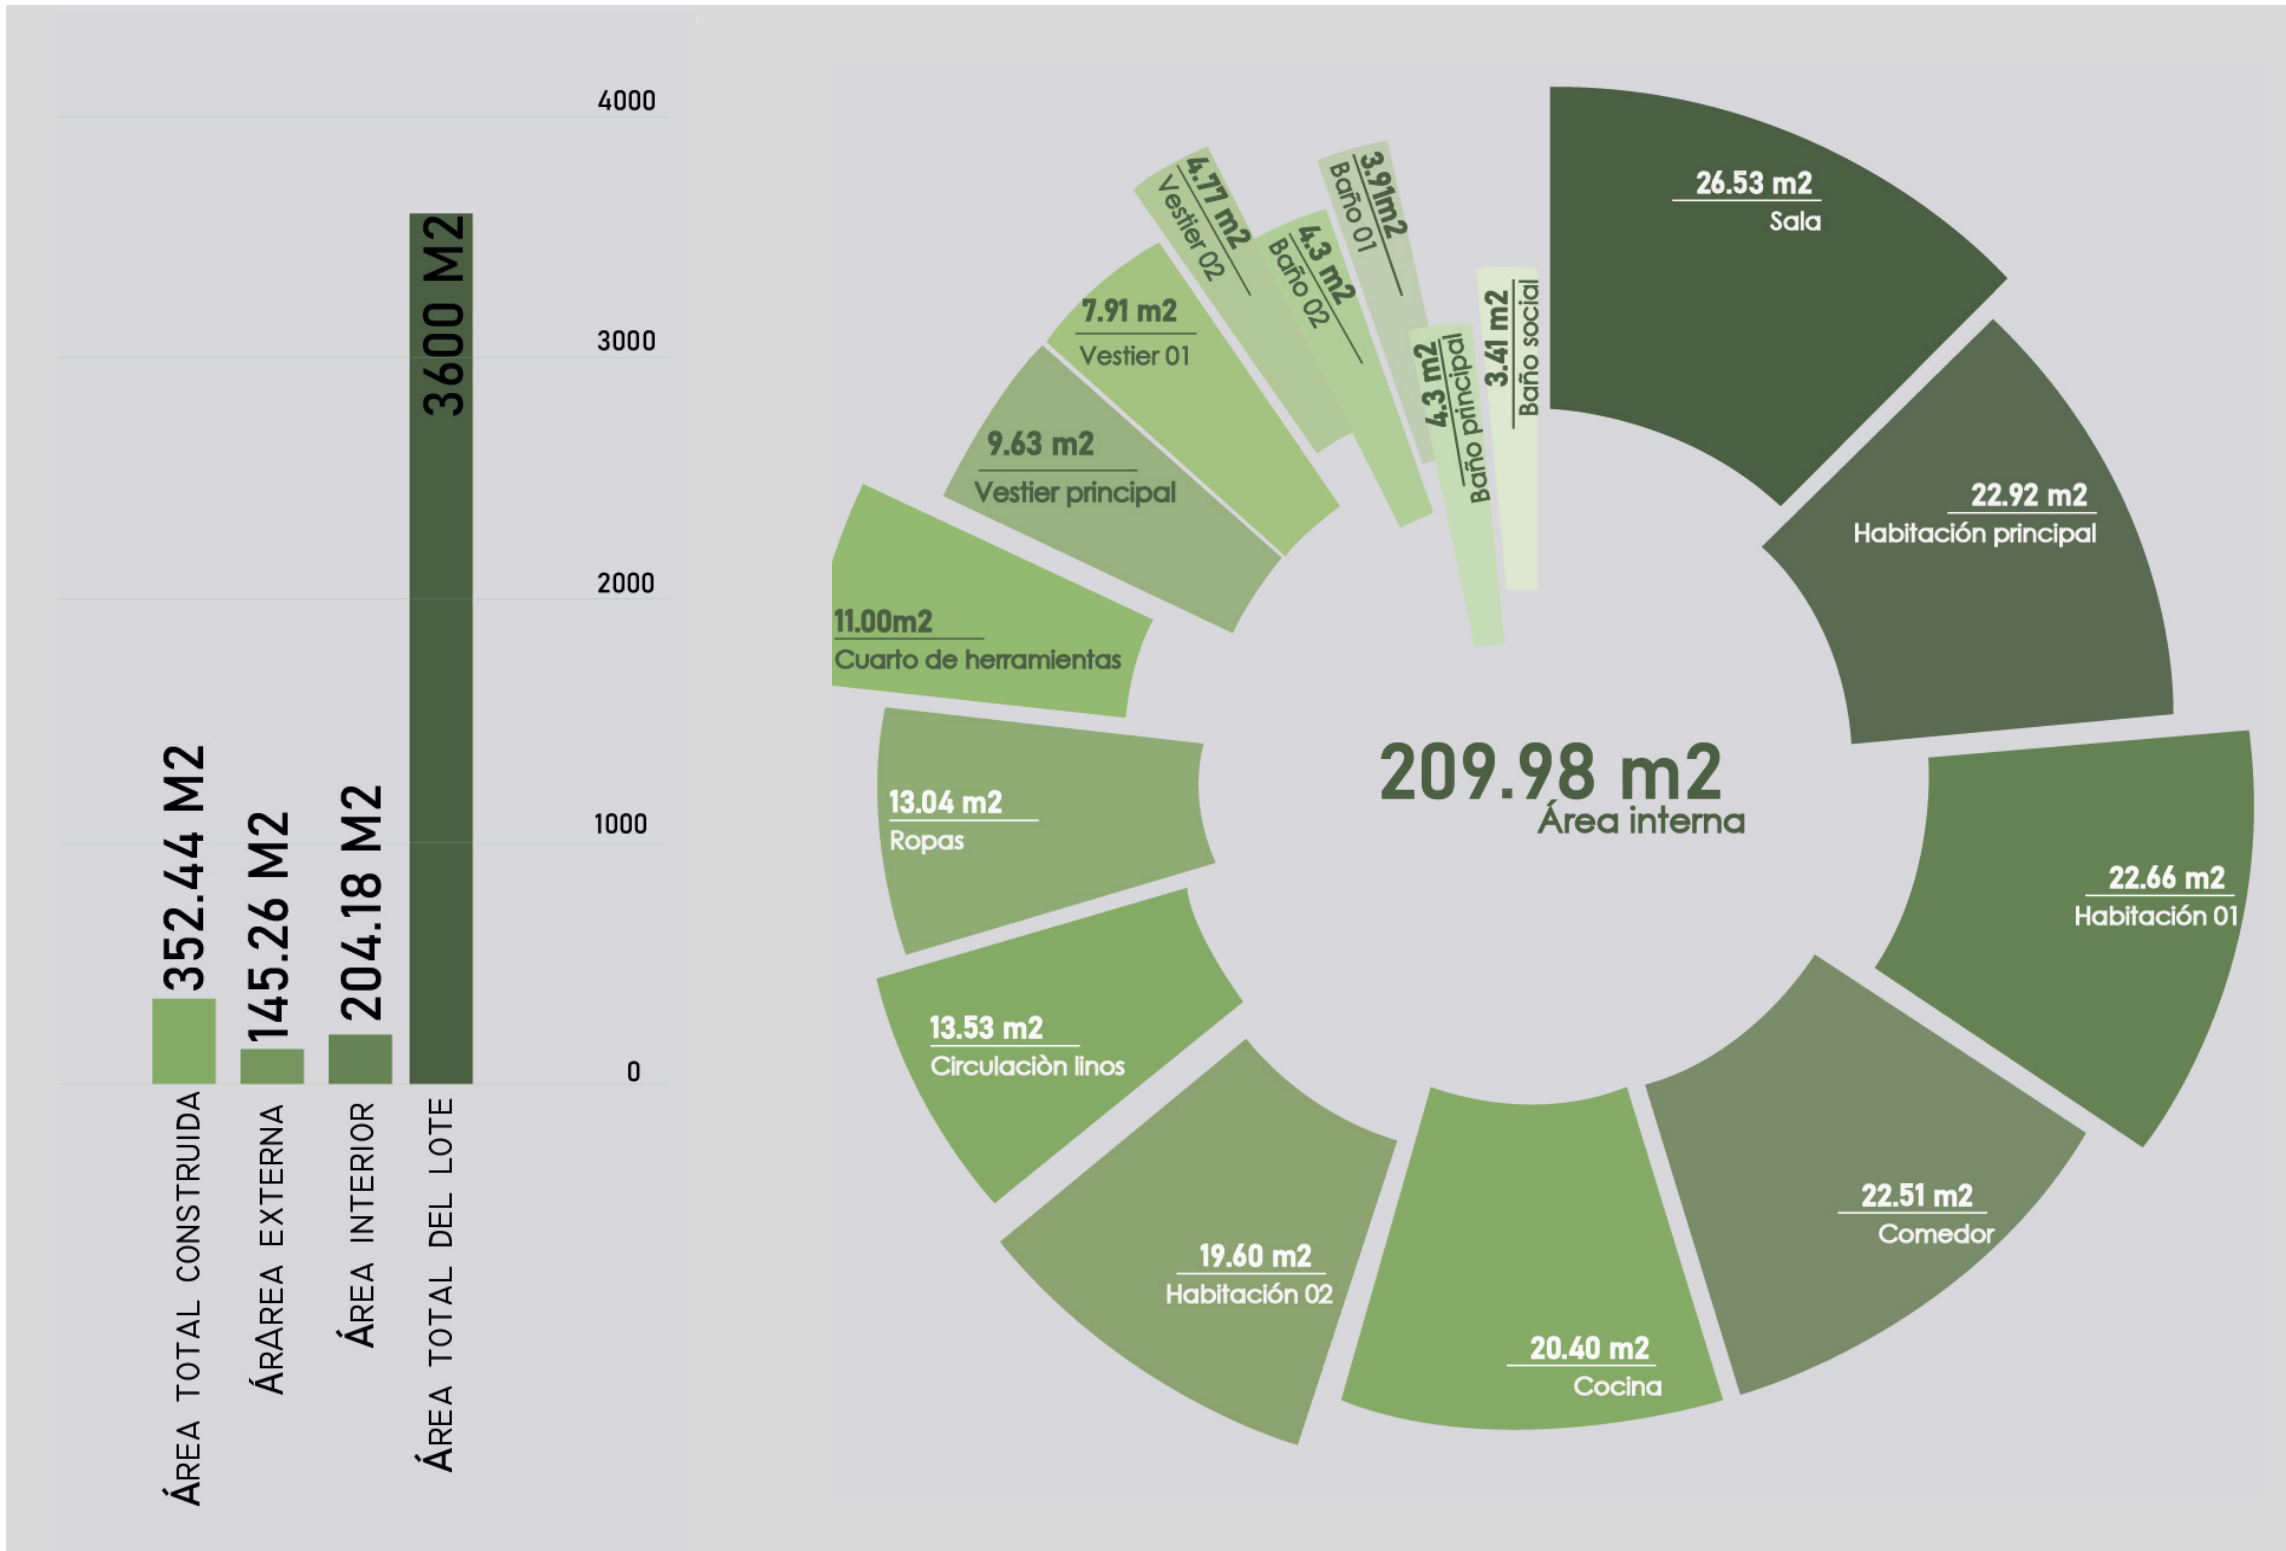

PLANTA ARQUITECTÓNICA PRIMER PISO

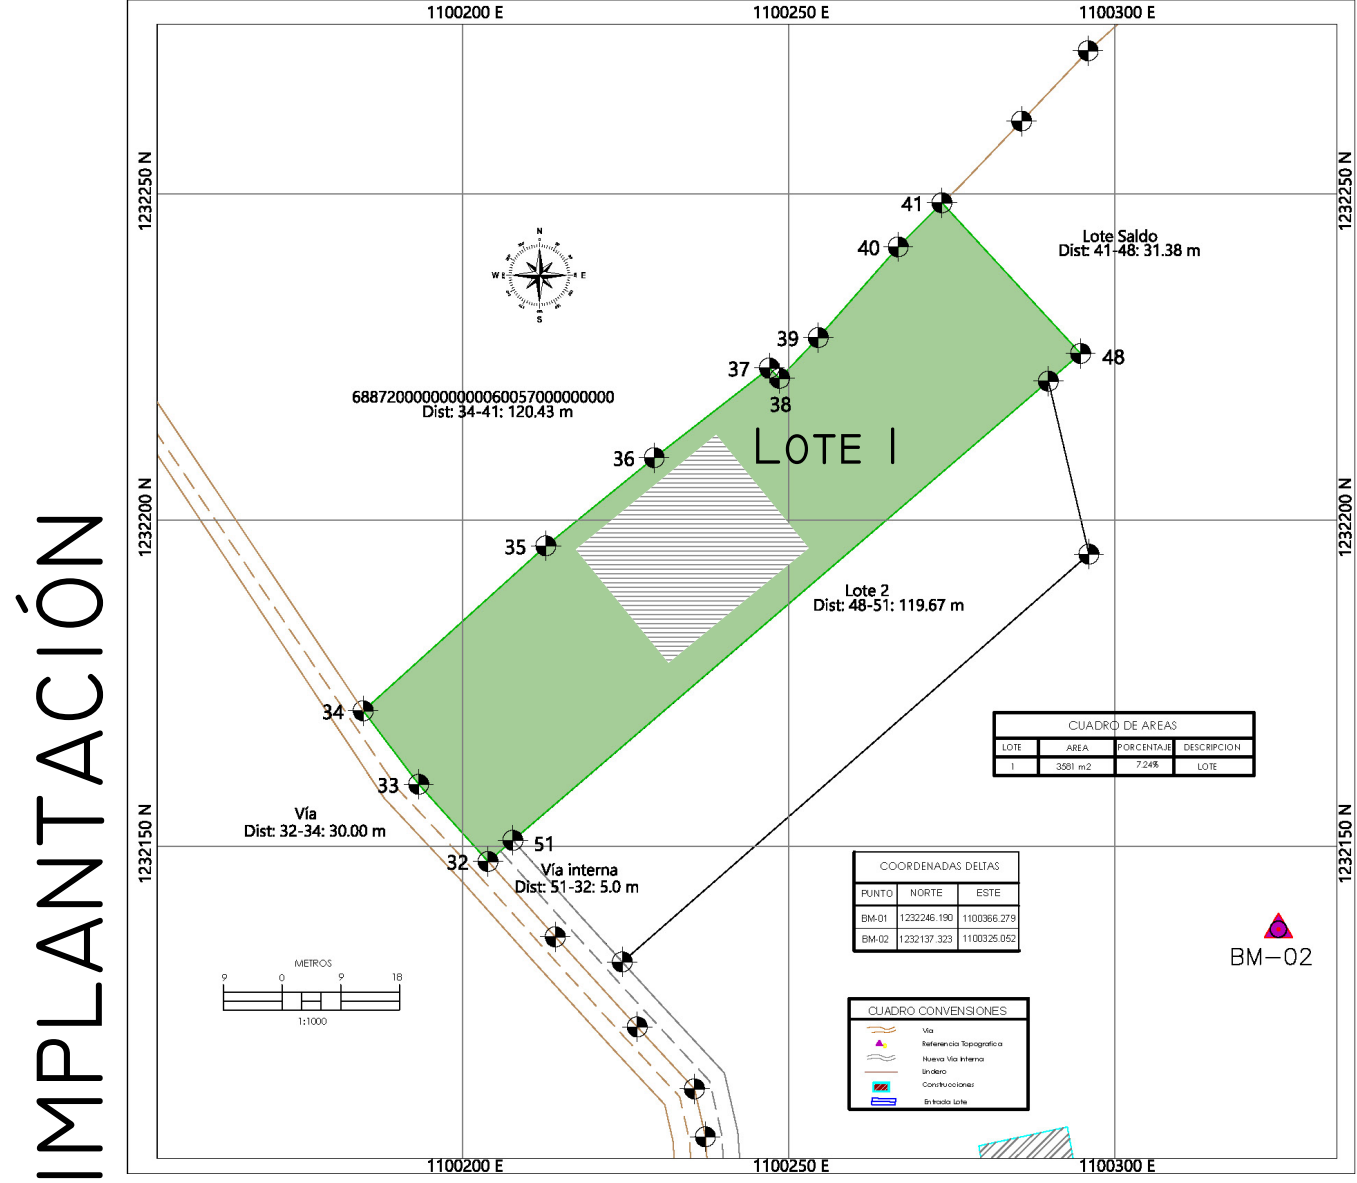

PROPIETARIOS:

ANDERSON MEJIA
IRIS CAROLINA REYES

DIRECCIÓN:

FINCA MIRABELLA
VILLANUEVA, SANTANDER

DISEÑO:

Arq. Jessica Viviana Rangel Espinosa
MAT. A30632018-1098735889

CONTIENE:

PLANO ARQUITECTONICO
PLANTA 1

TRAMITE:

CONSTRUCCIÓN VIVIENDA NUEVA

FECHA:

ENERO 2024

ESCALA:

1:50

PLANO:

1 DE 1

OBSERVACIONES