



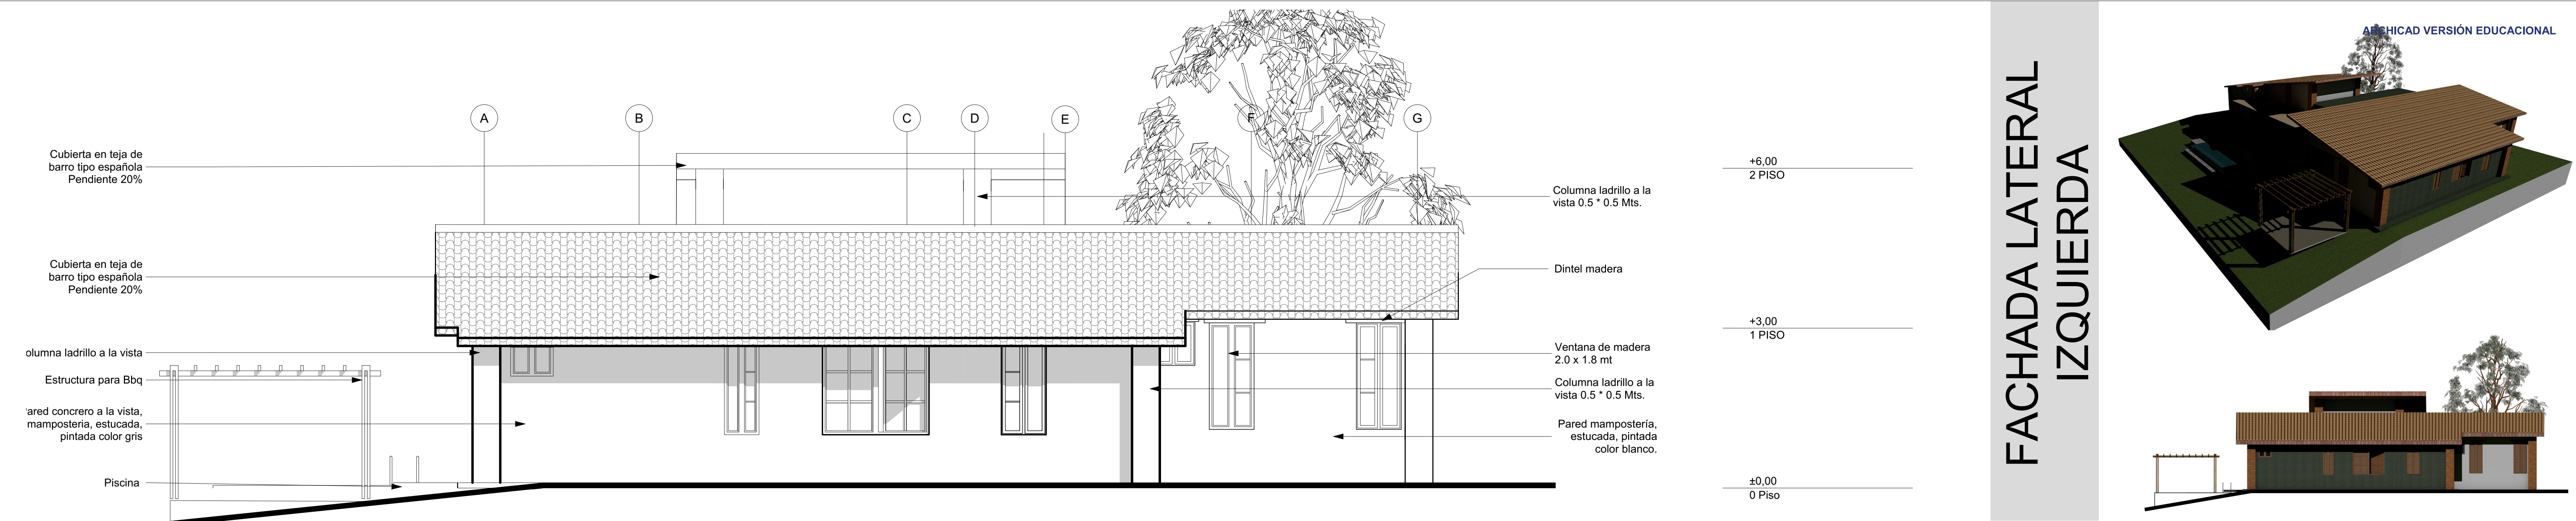


PLANO DE CUBIERTAS

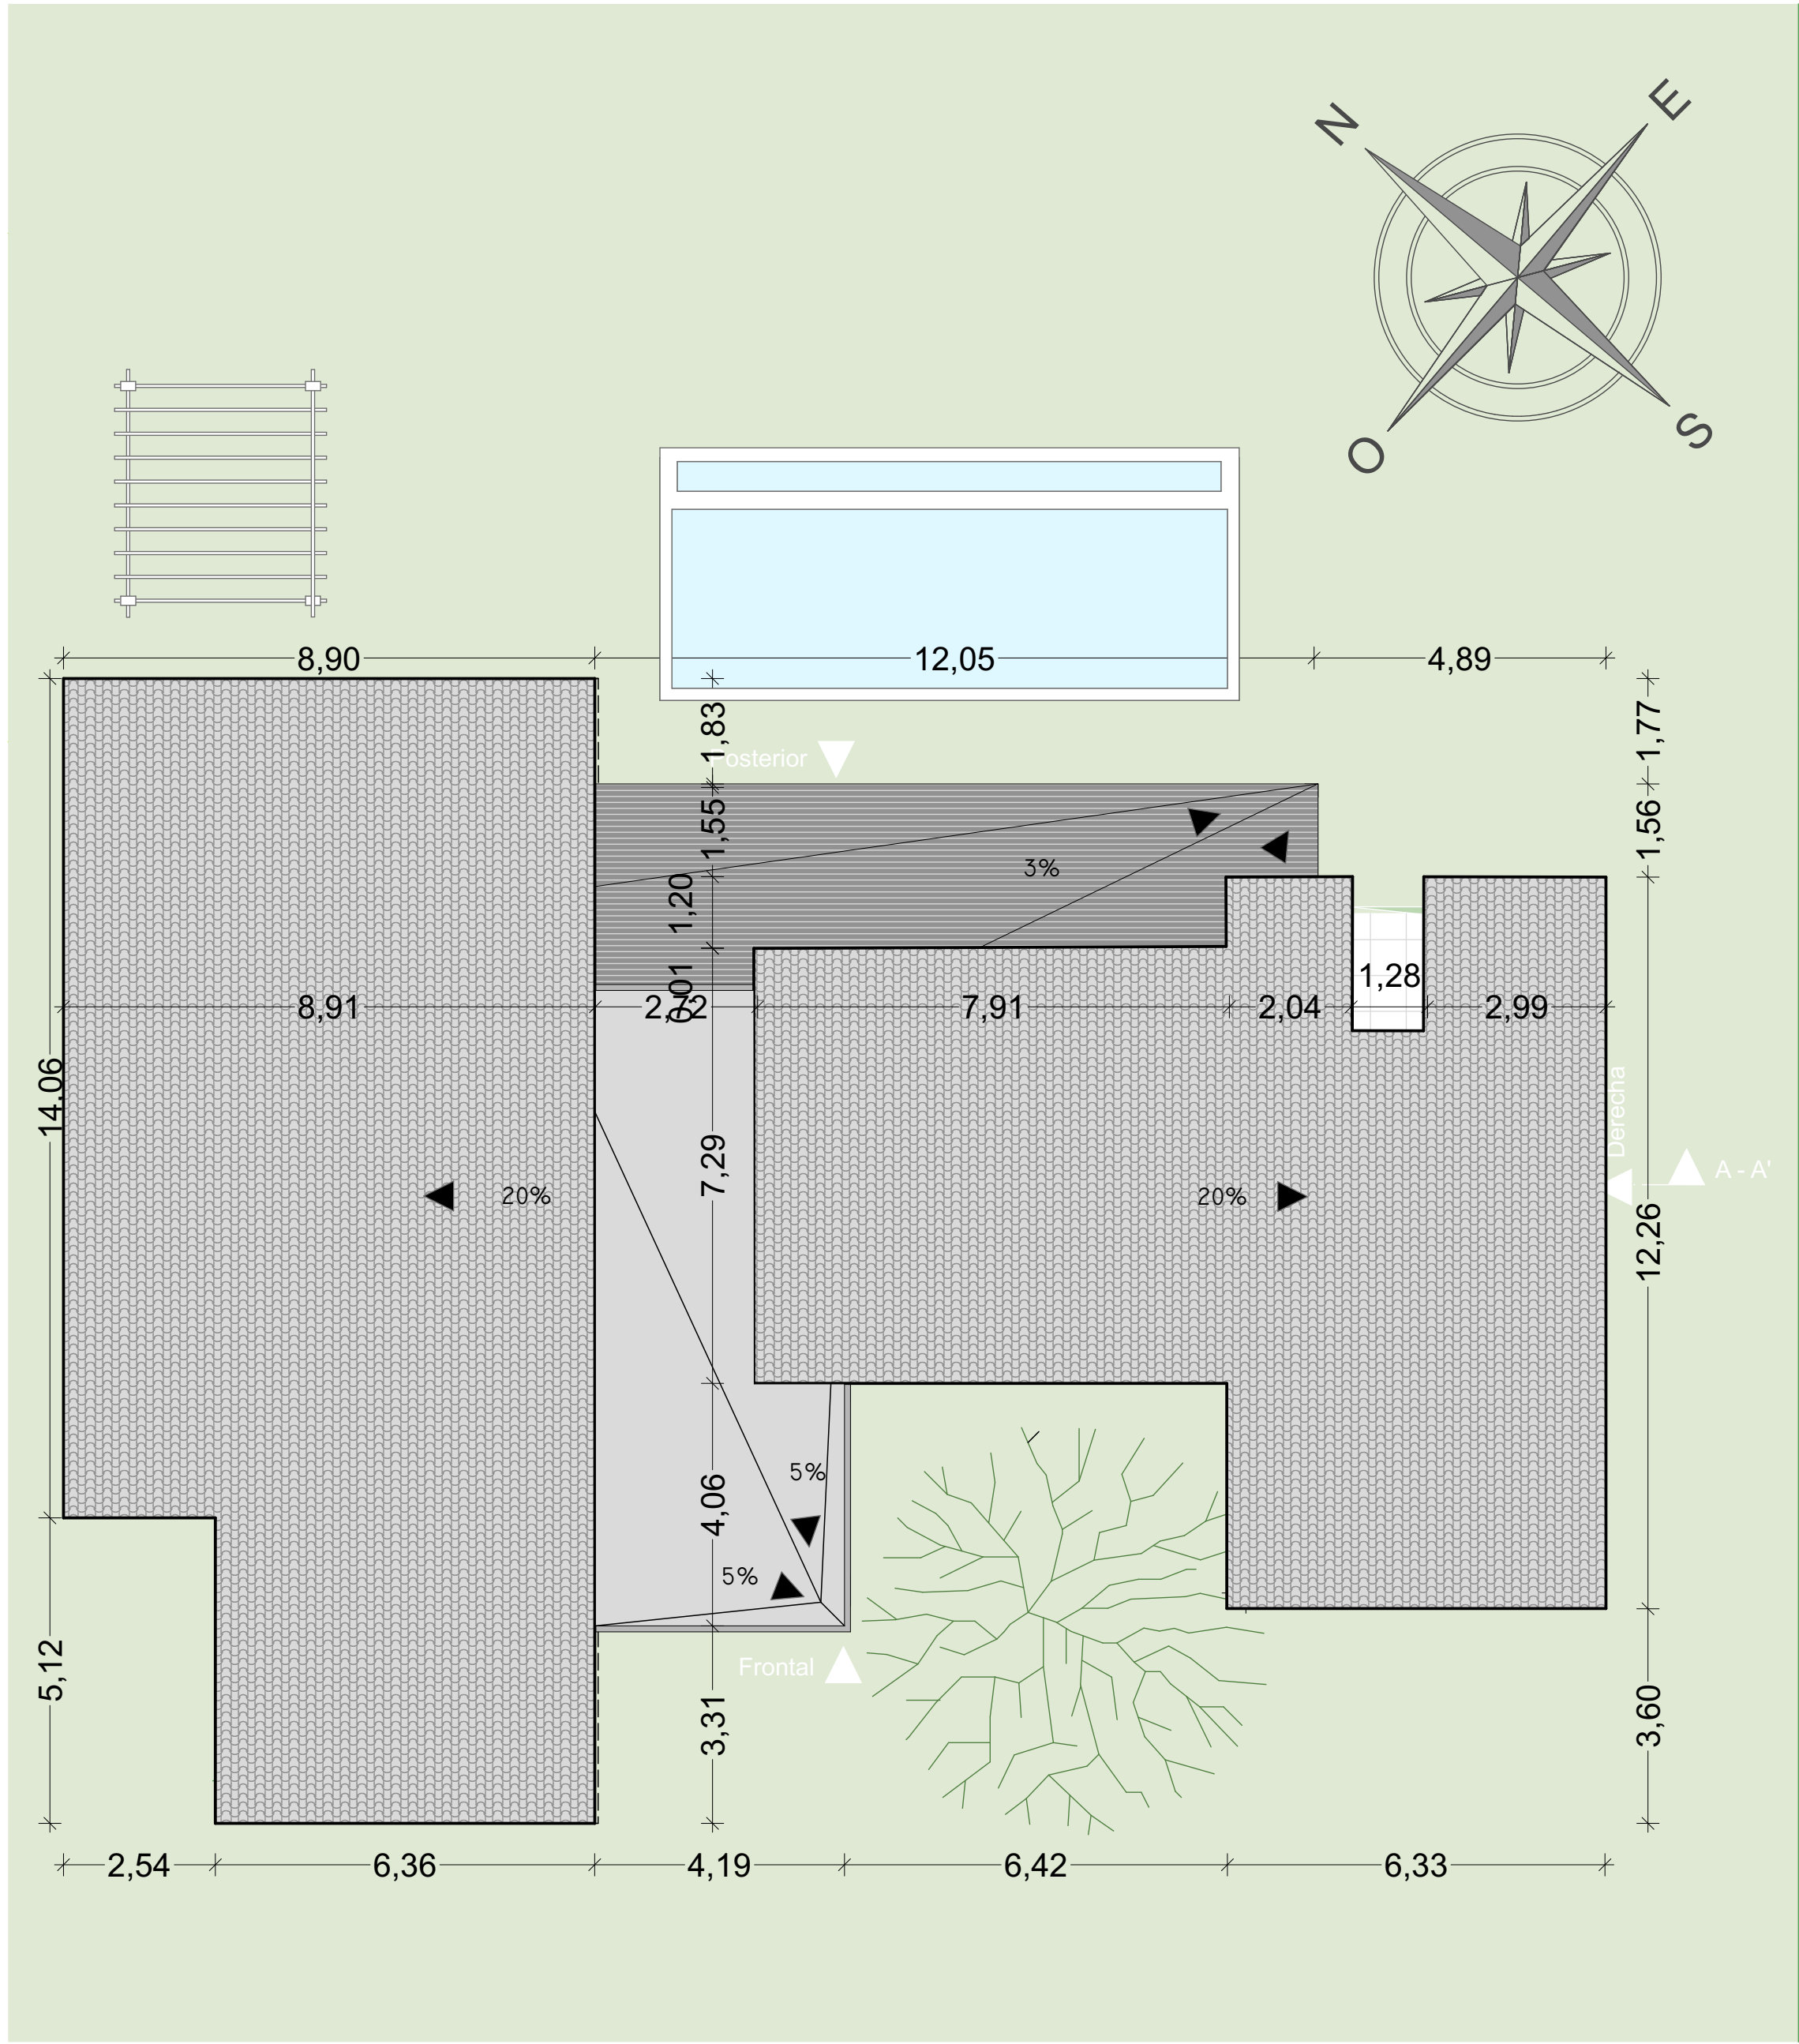


DETALLES CONSTRUCTIVOS


D-1. PLACA CUBIERTA

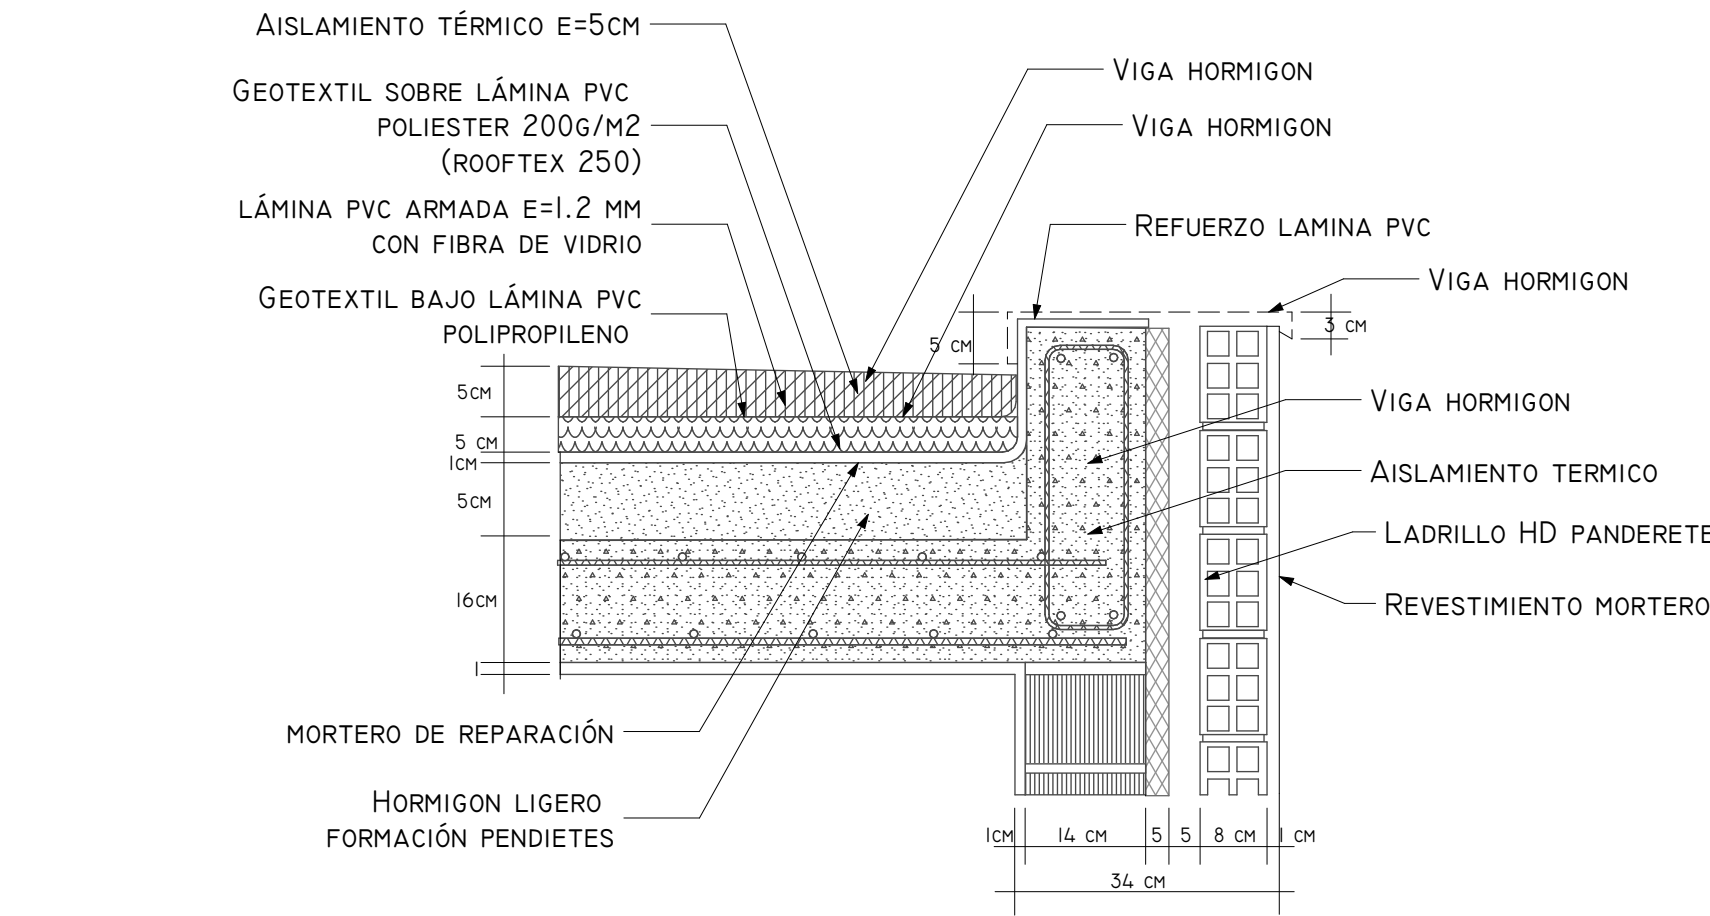


D-2. CONTENEDOR DE RAÍCES

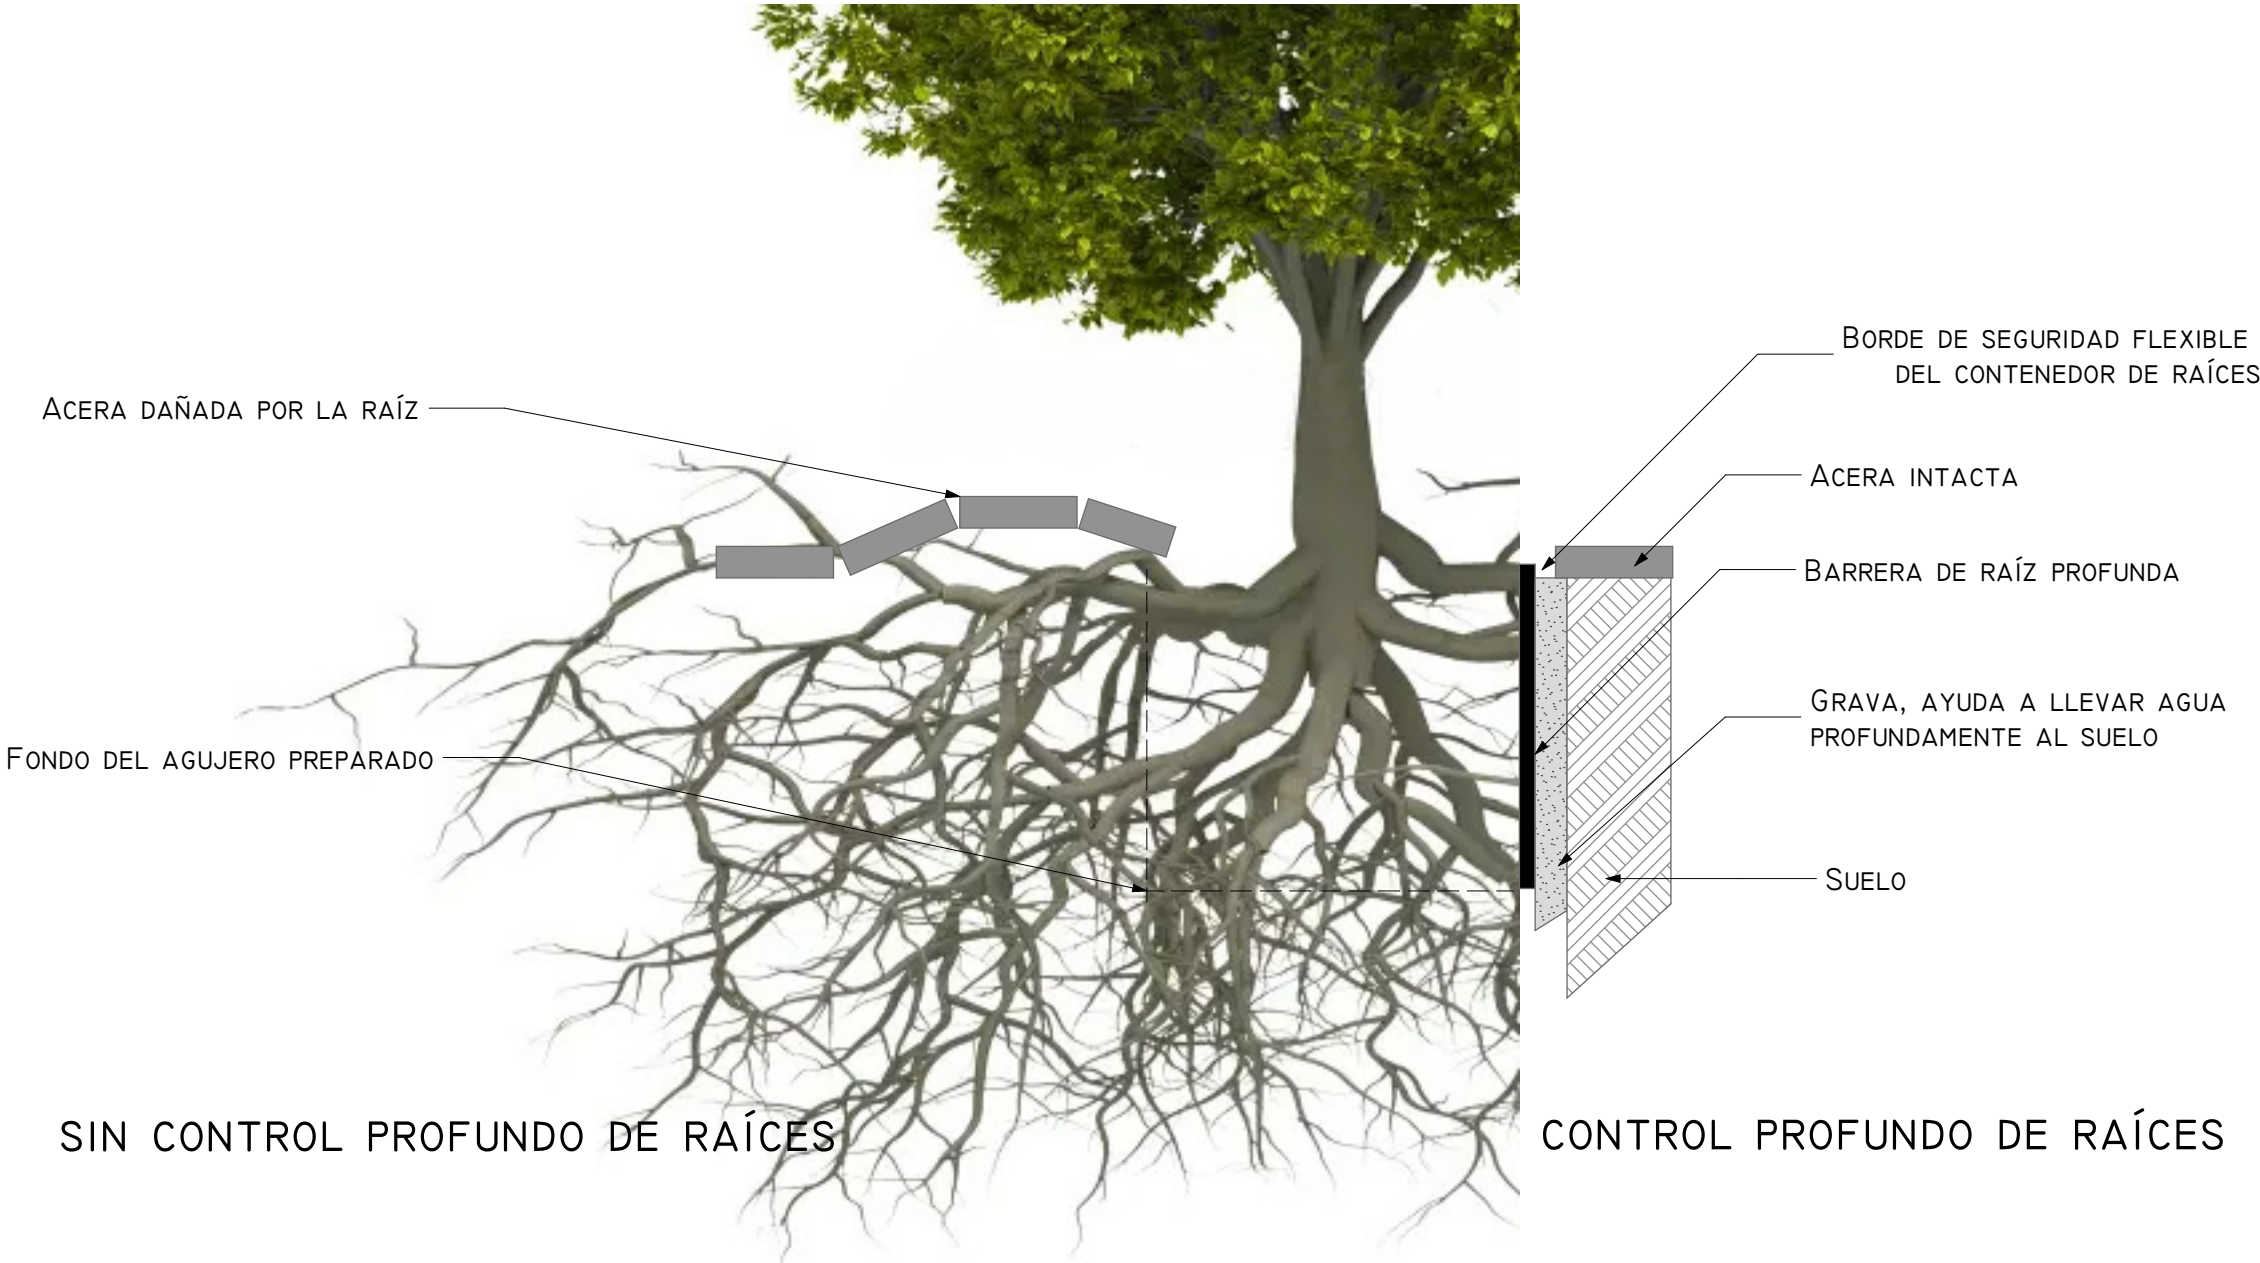

D-3. CALADOS

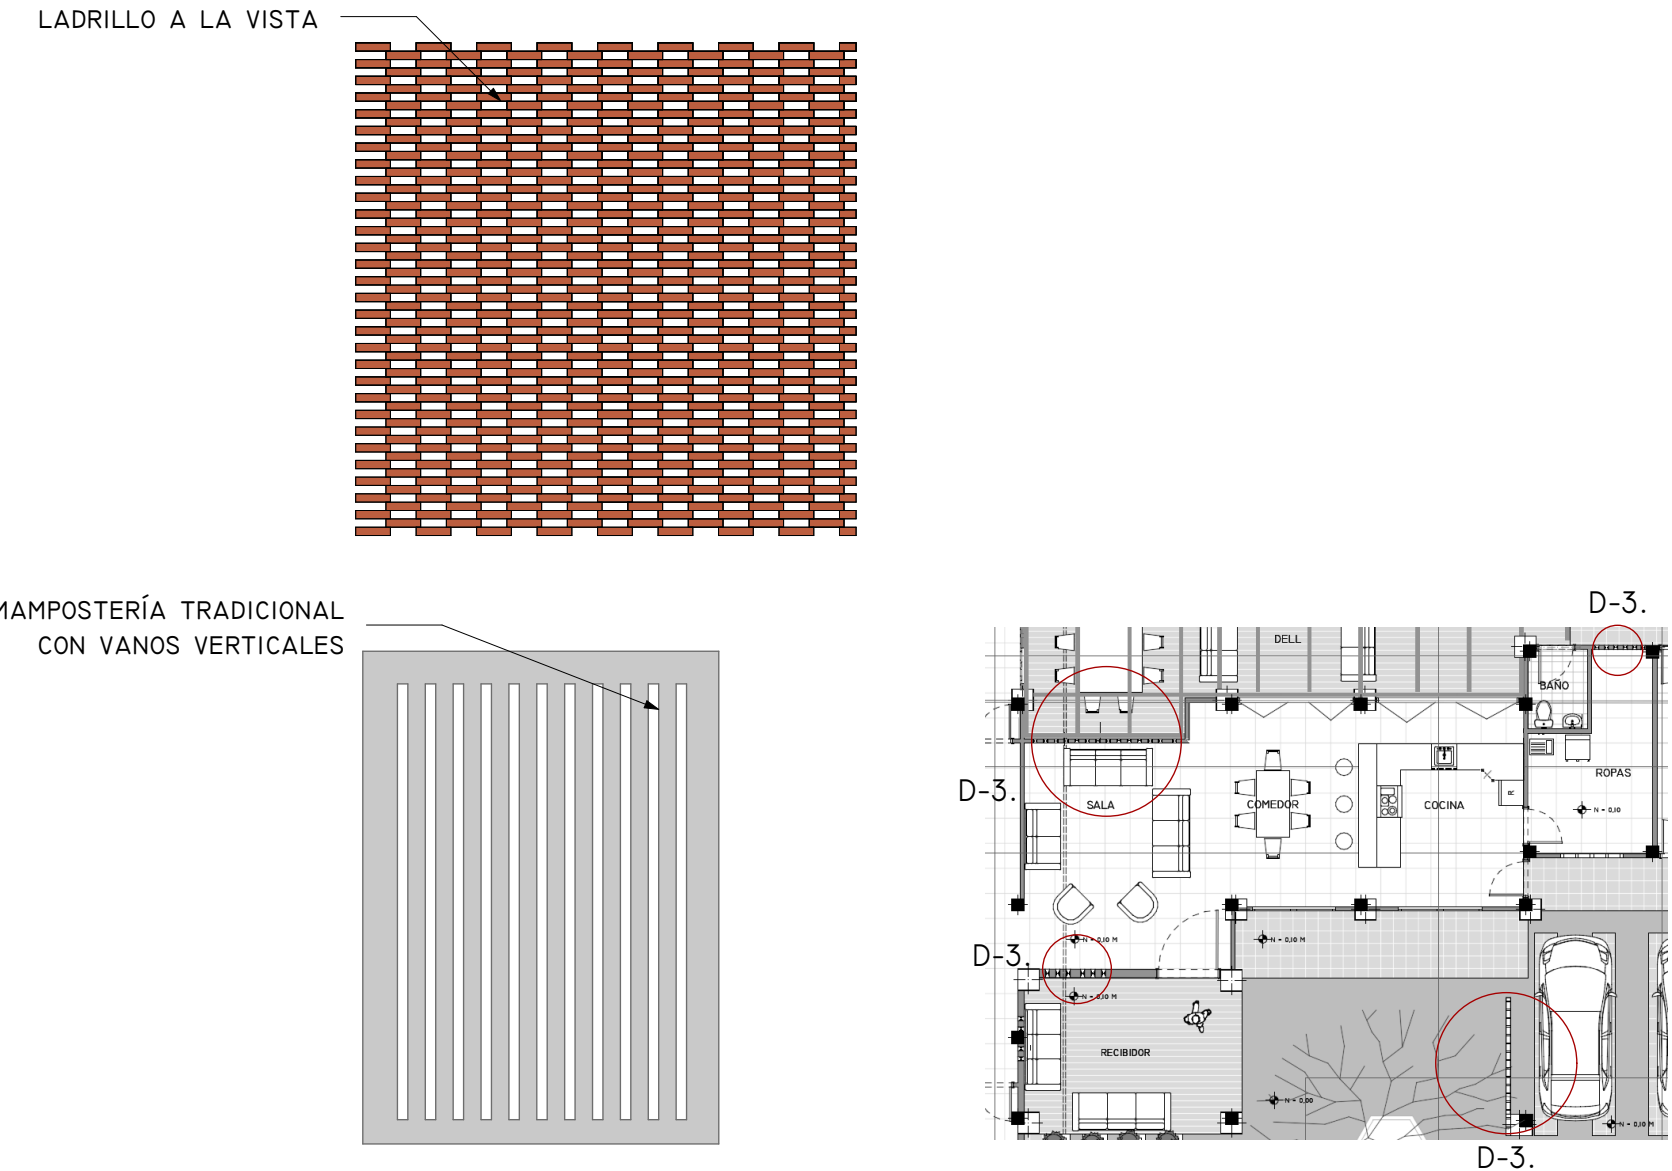

D-4. PISCINA TIPO INFINITA

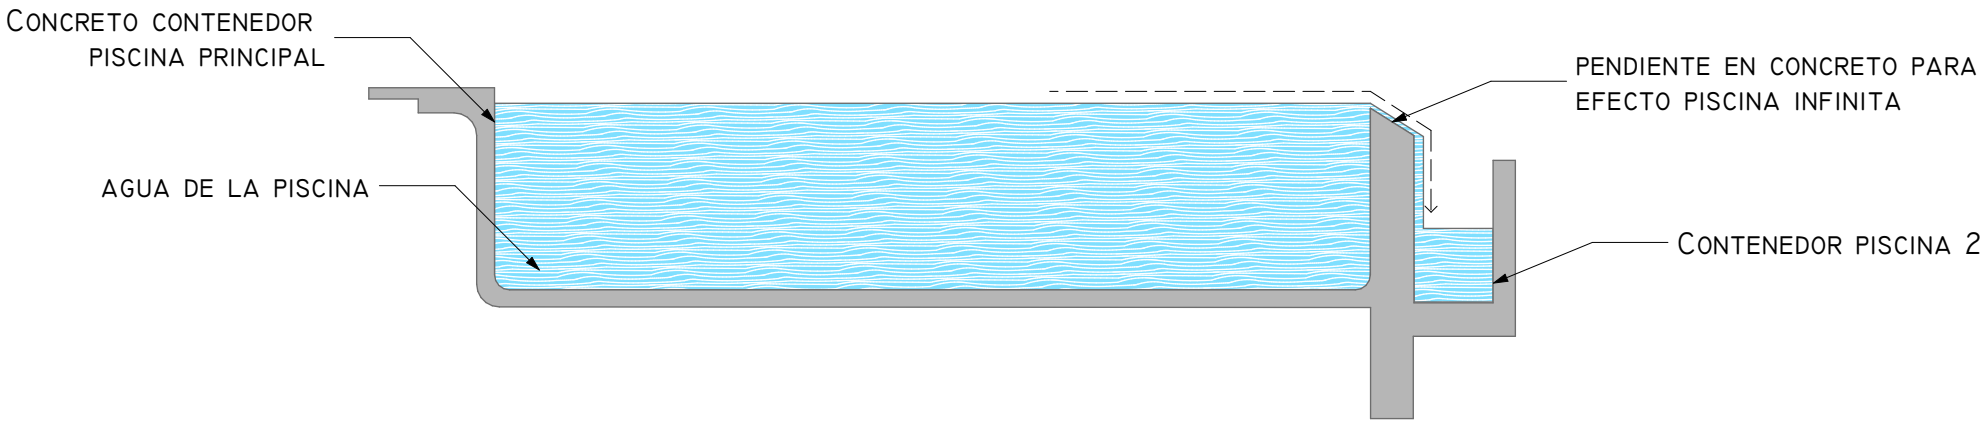

PROPIETARIOS:	DIRECCIÓN:	DISEÑO:	CONTIENE:	FECHA:	OBSERVACIONES
ANDERSON MEJIA IRIS CAROLINA REYES	FINCA MIRABELLA VILLANUEVA, SANTANDER		PLANO DE CUBIERTAS FACHADA LATERAL IZQUIERDA	ENERO 2024	
			TRAMITE:	ESCALA:	OBSERVACIONES
			CONSTRUCCIÓN VIVIENDA NUEVA	1:50	
				PLANO:	OBSERVACIONES
				1 DE 1	