


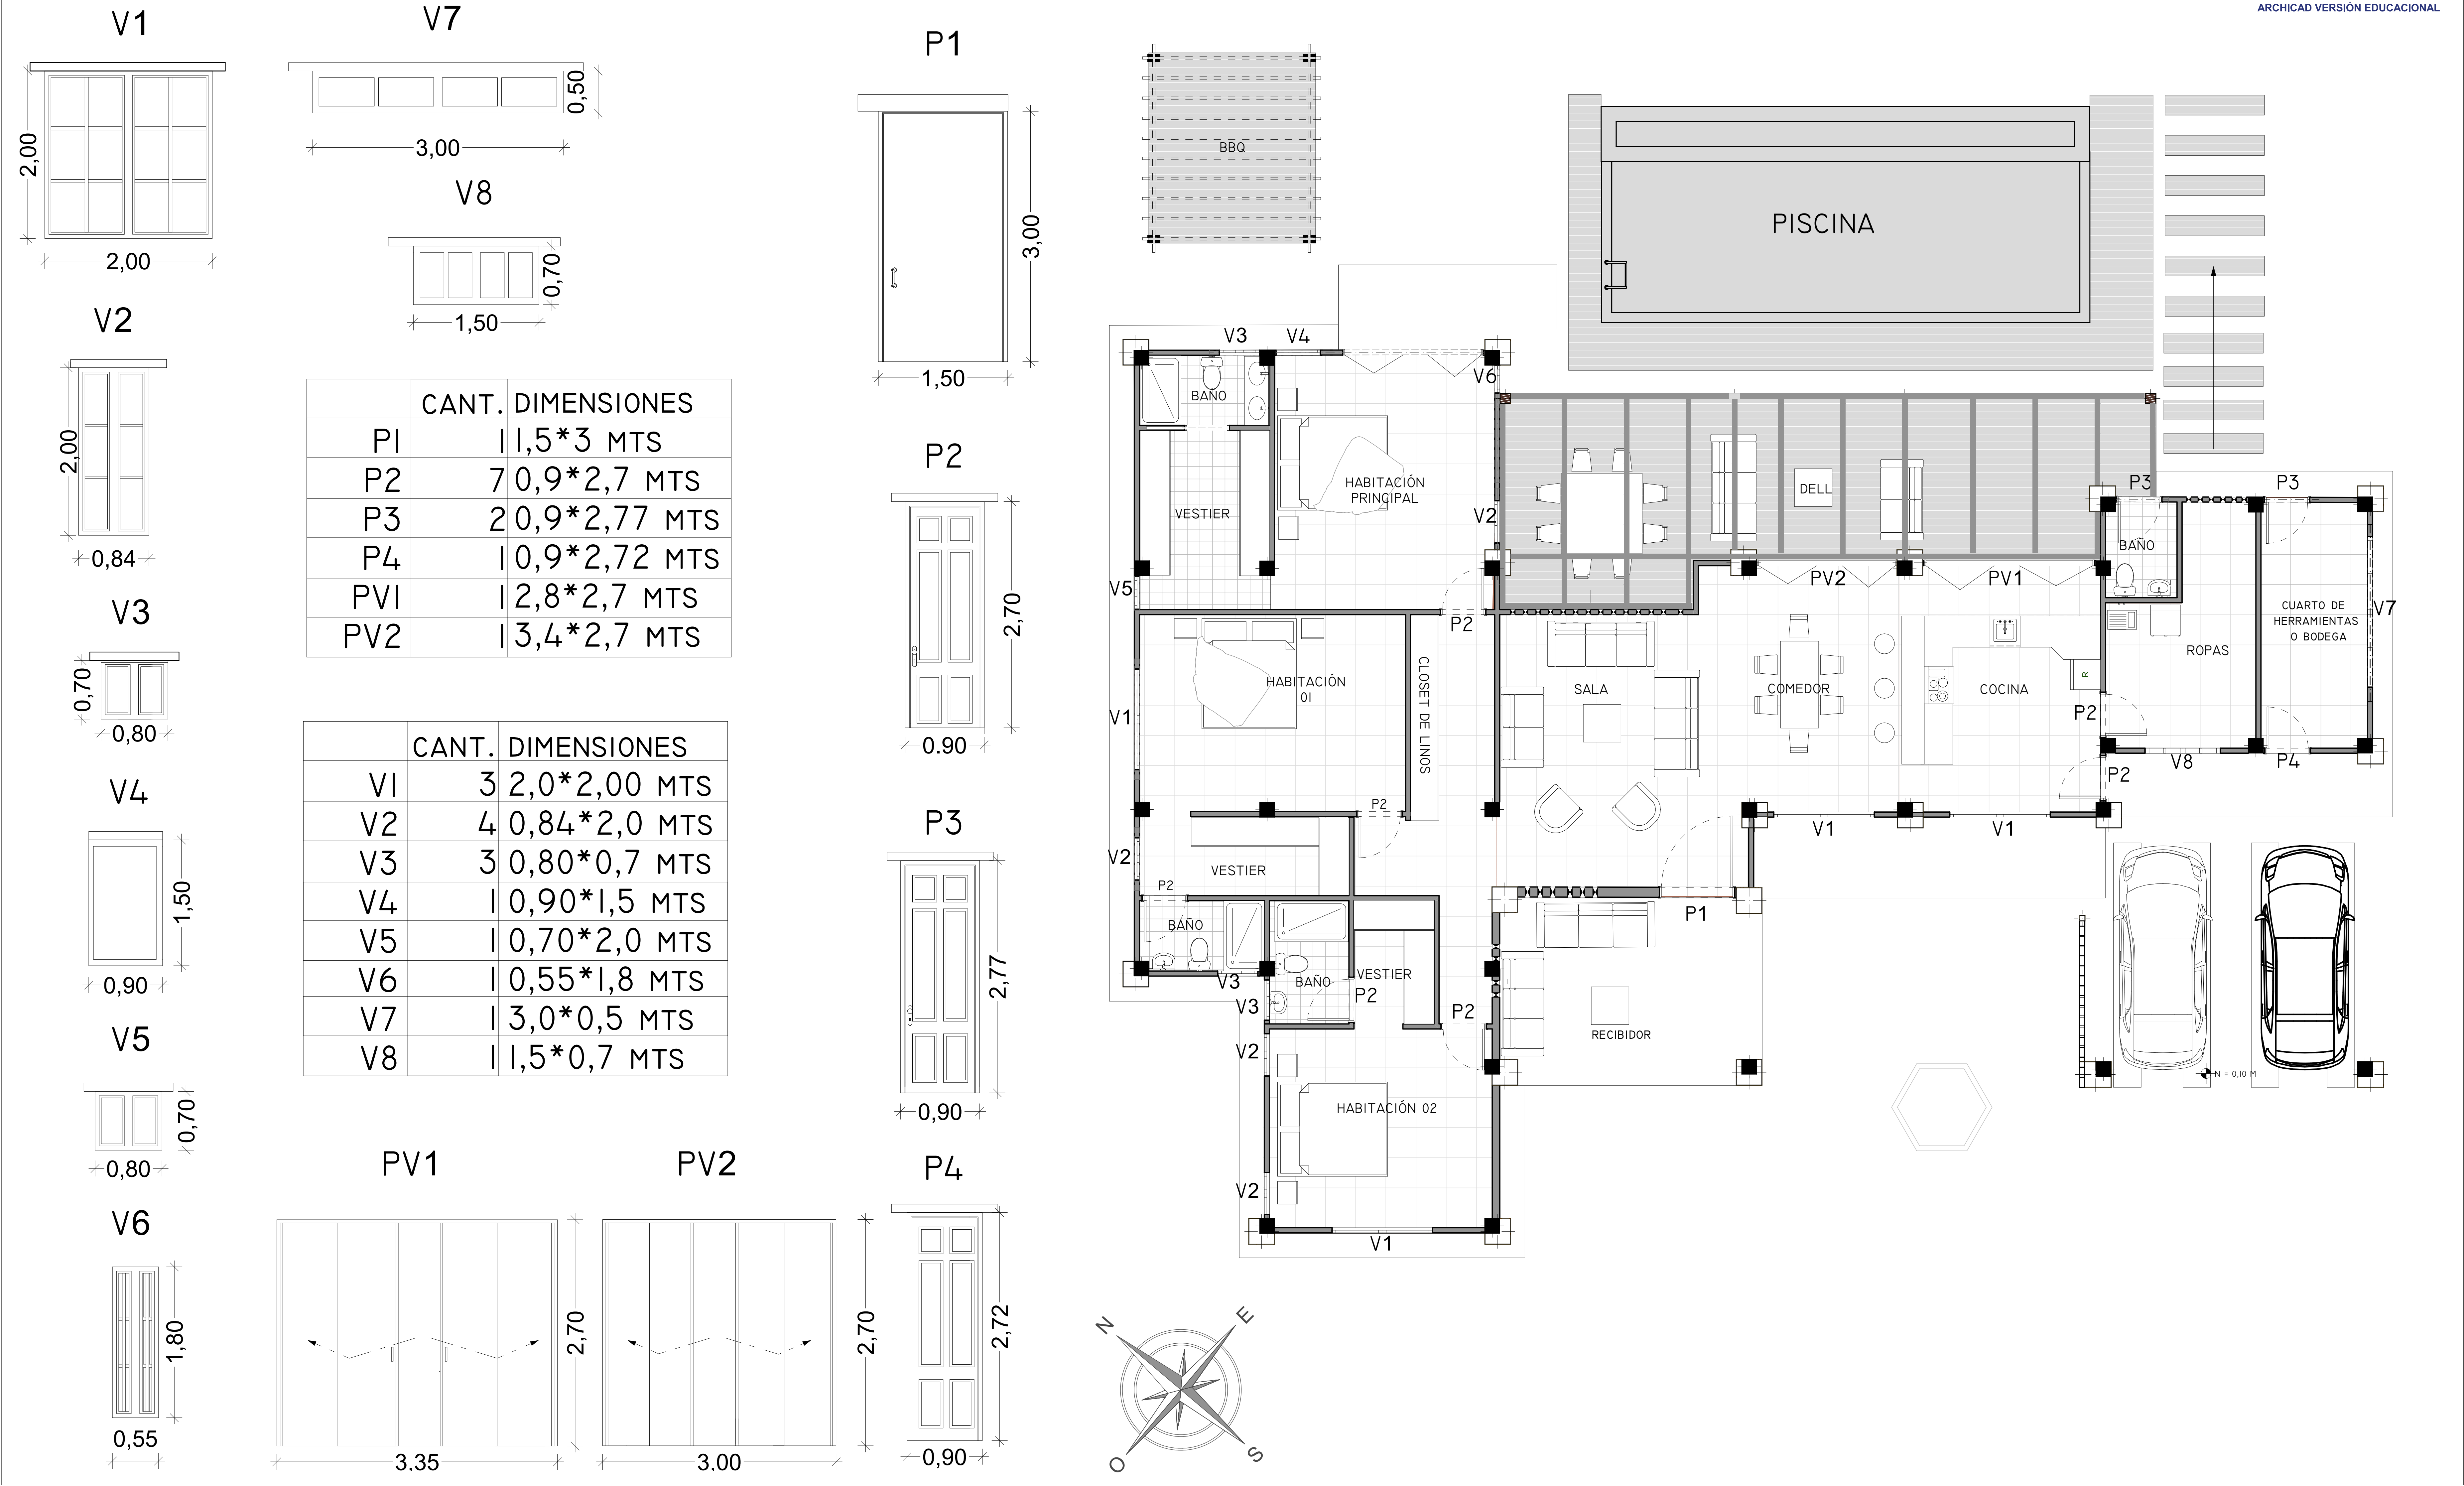

V4

V5

V6

V7

V8

P1

P2

P3

P4

PV1

PV2

Architectural floor plan of a house. The plan includes a swimming pool (PISCINA) and a BBQ area. The main living area consists of a living room (SALA), dining room (COMEDOR), and kitchen (COCINA). There are two bedrooms (HABITACIÓN 01 and HABITACIÓN 02), a main bedroom (HABITACIÓN PRINCIPAL), and a bathroom (BAÑO). A closet (CLOSET DE LINOS) is located between the bedrooms. A reception area (RECIBIDOR) is at the entrance. A utility room (CUARTO DE HERRAMIENTAS O BODEGA) and a laundry room (ROPAS) are also shown. The plan is annotated with window (V1-V8) and door (P1-P4, PV1-PV2) labels and dimensions. A north arrow is present.

PROPIETARIOS: ANDERSON MEJIA IRIS CAROLINA REYES	DIRECCIÓN: FINCA MIRABELLA VILLANUEVA, SANTANDER	DISEÑO: Arq. Jessica Viviana Rangel Espinosa MAT. A30632018-1098735889	CONTIENE: PLANO ARQUITECTONICO PLANTA 1	FECHA: MARZO 2024	OBSERVACIONES:
			TRAMITE: CONSTRUCCIÓN VIVIENDA NUEVA	ESCALA: 1:50	