




PLANTA PRIMER PISO

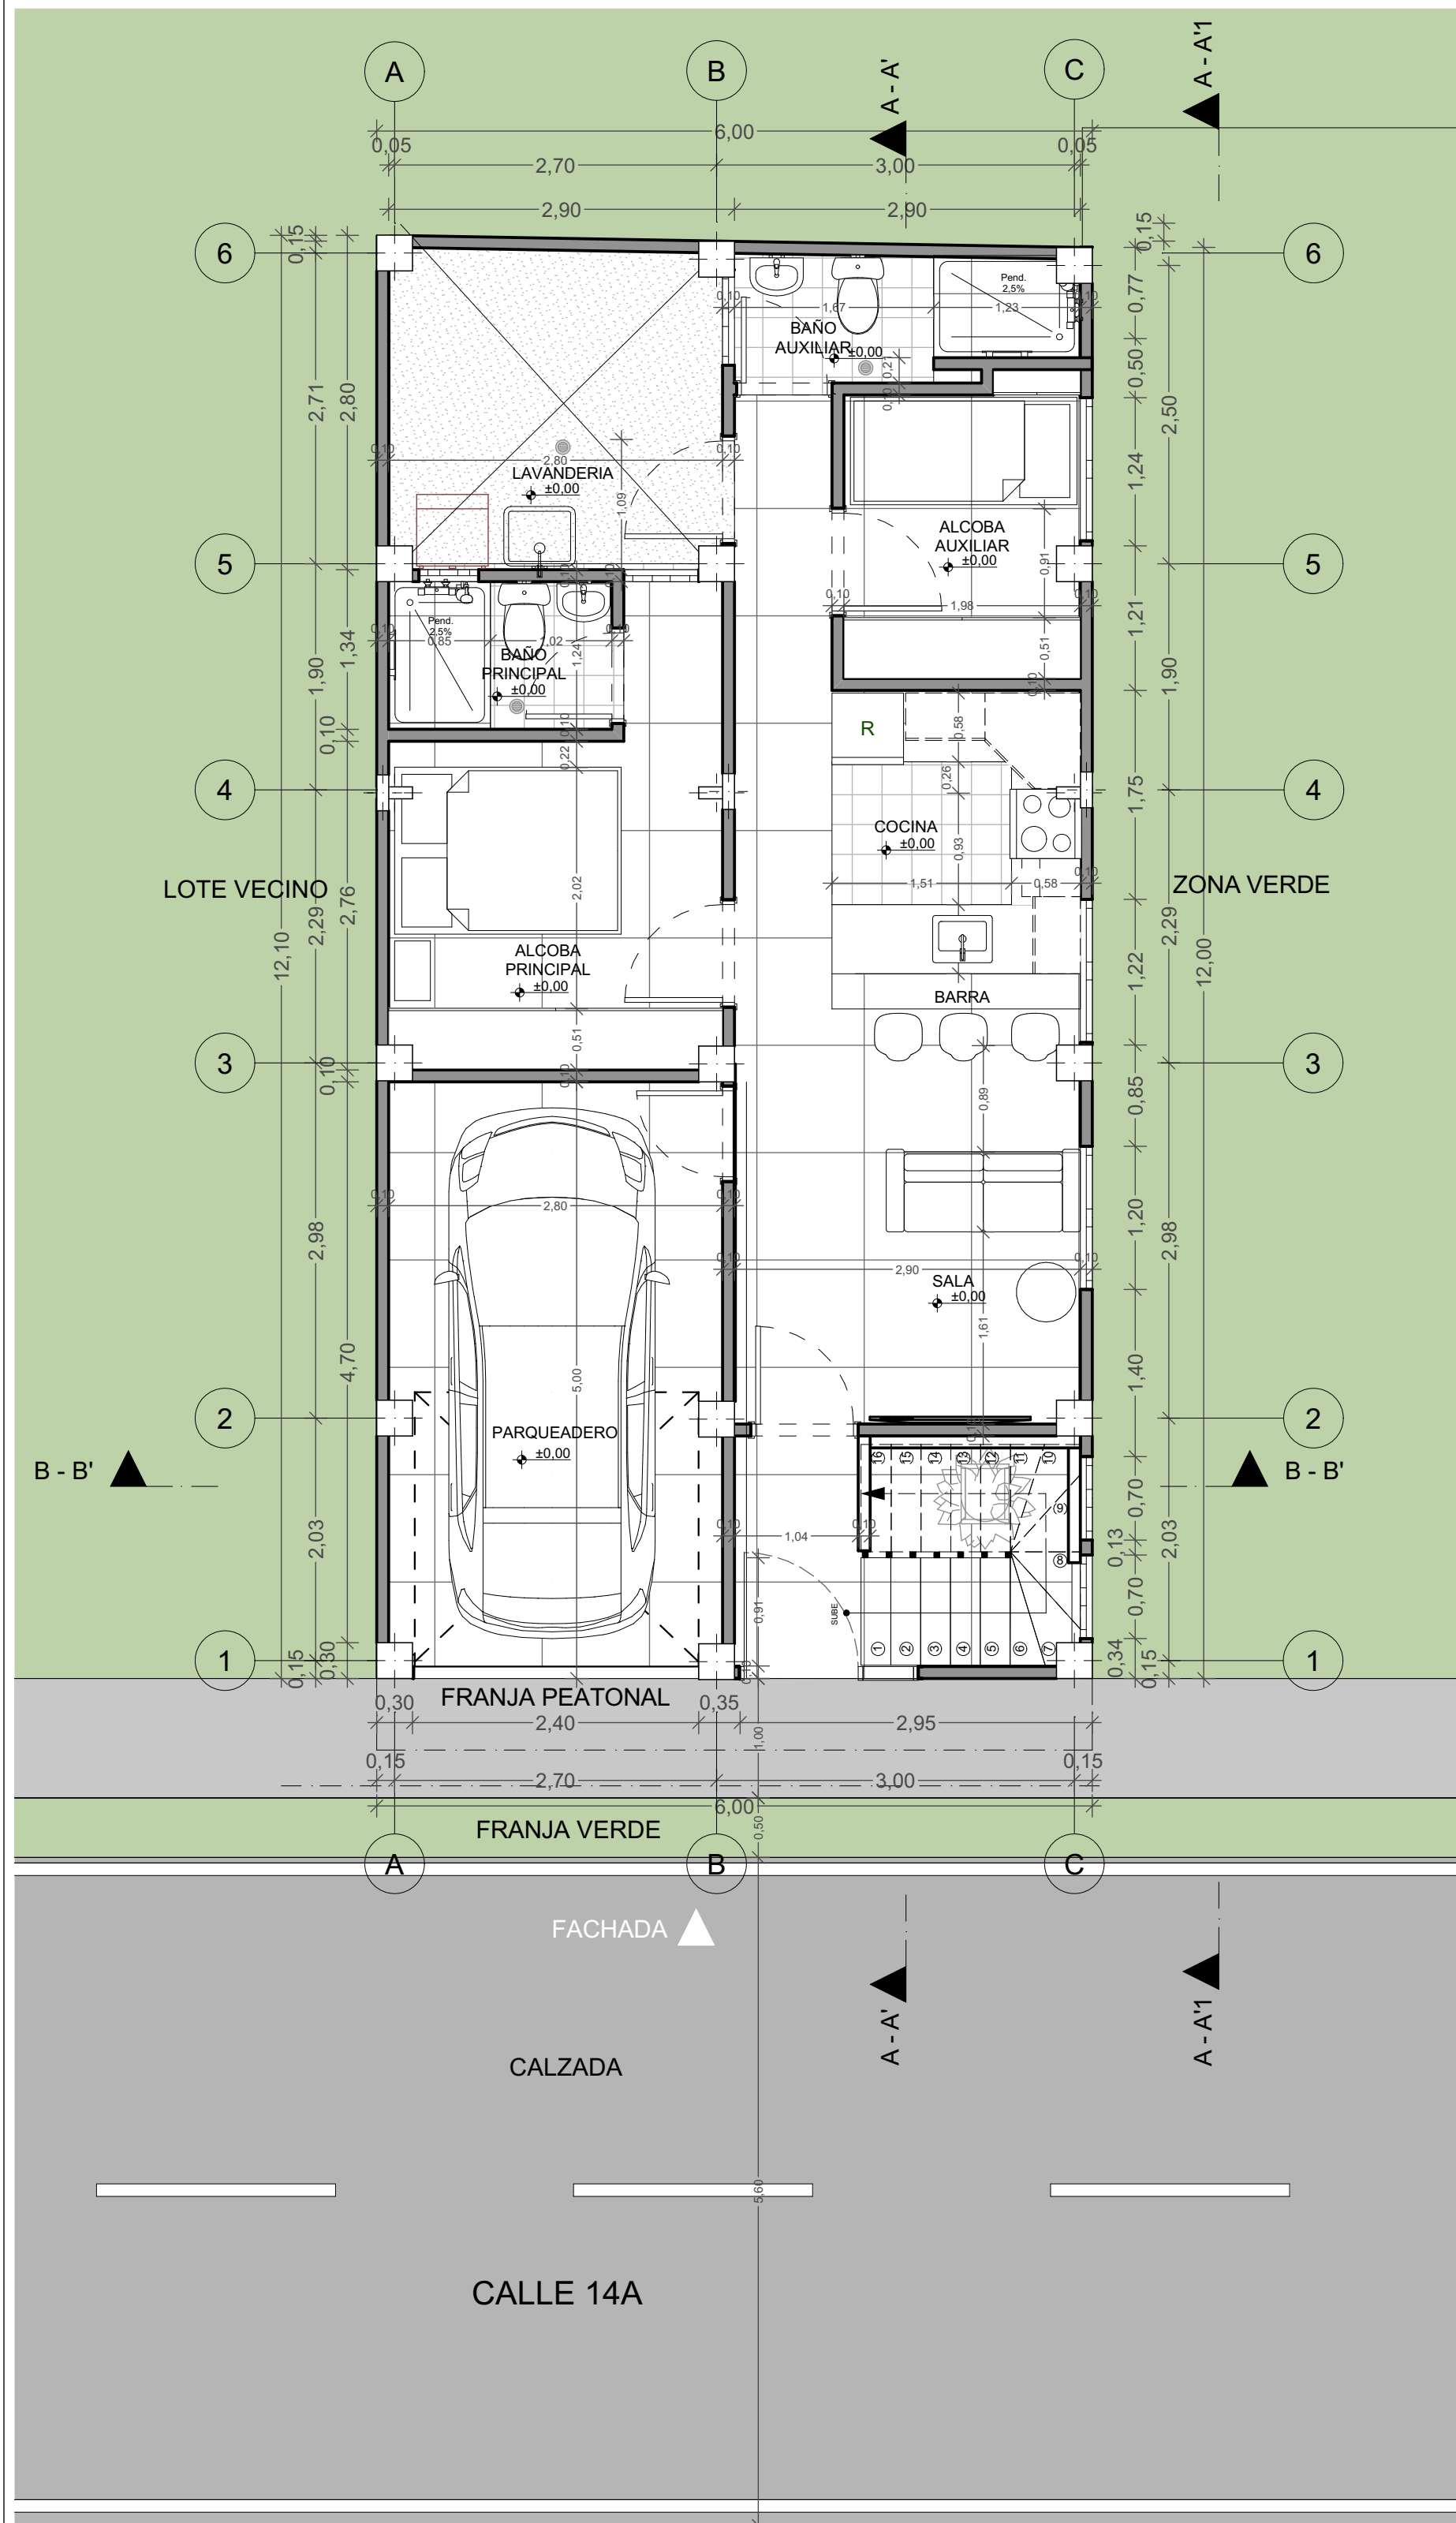


PLANTA SEGUNDO PISO

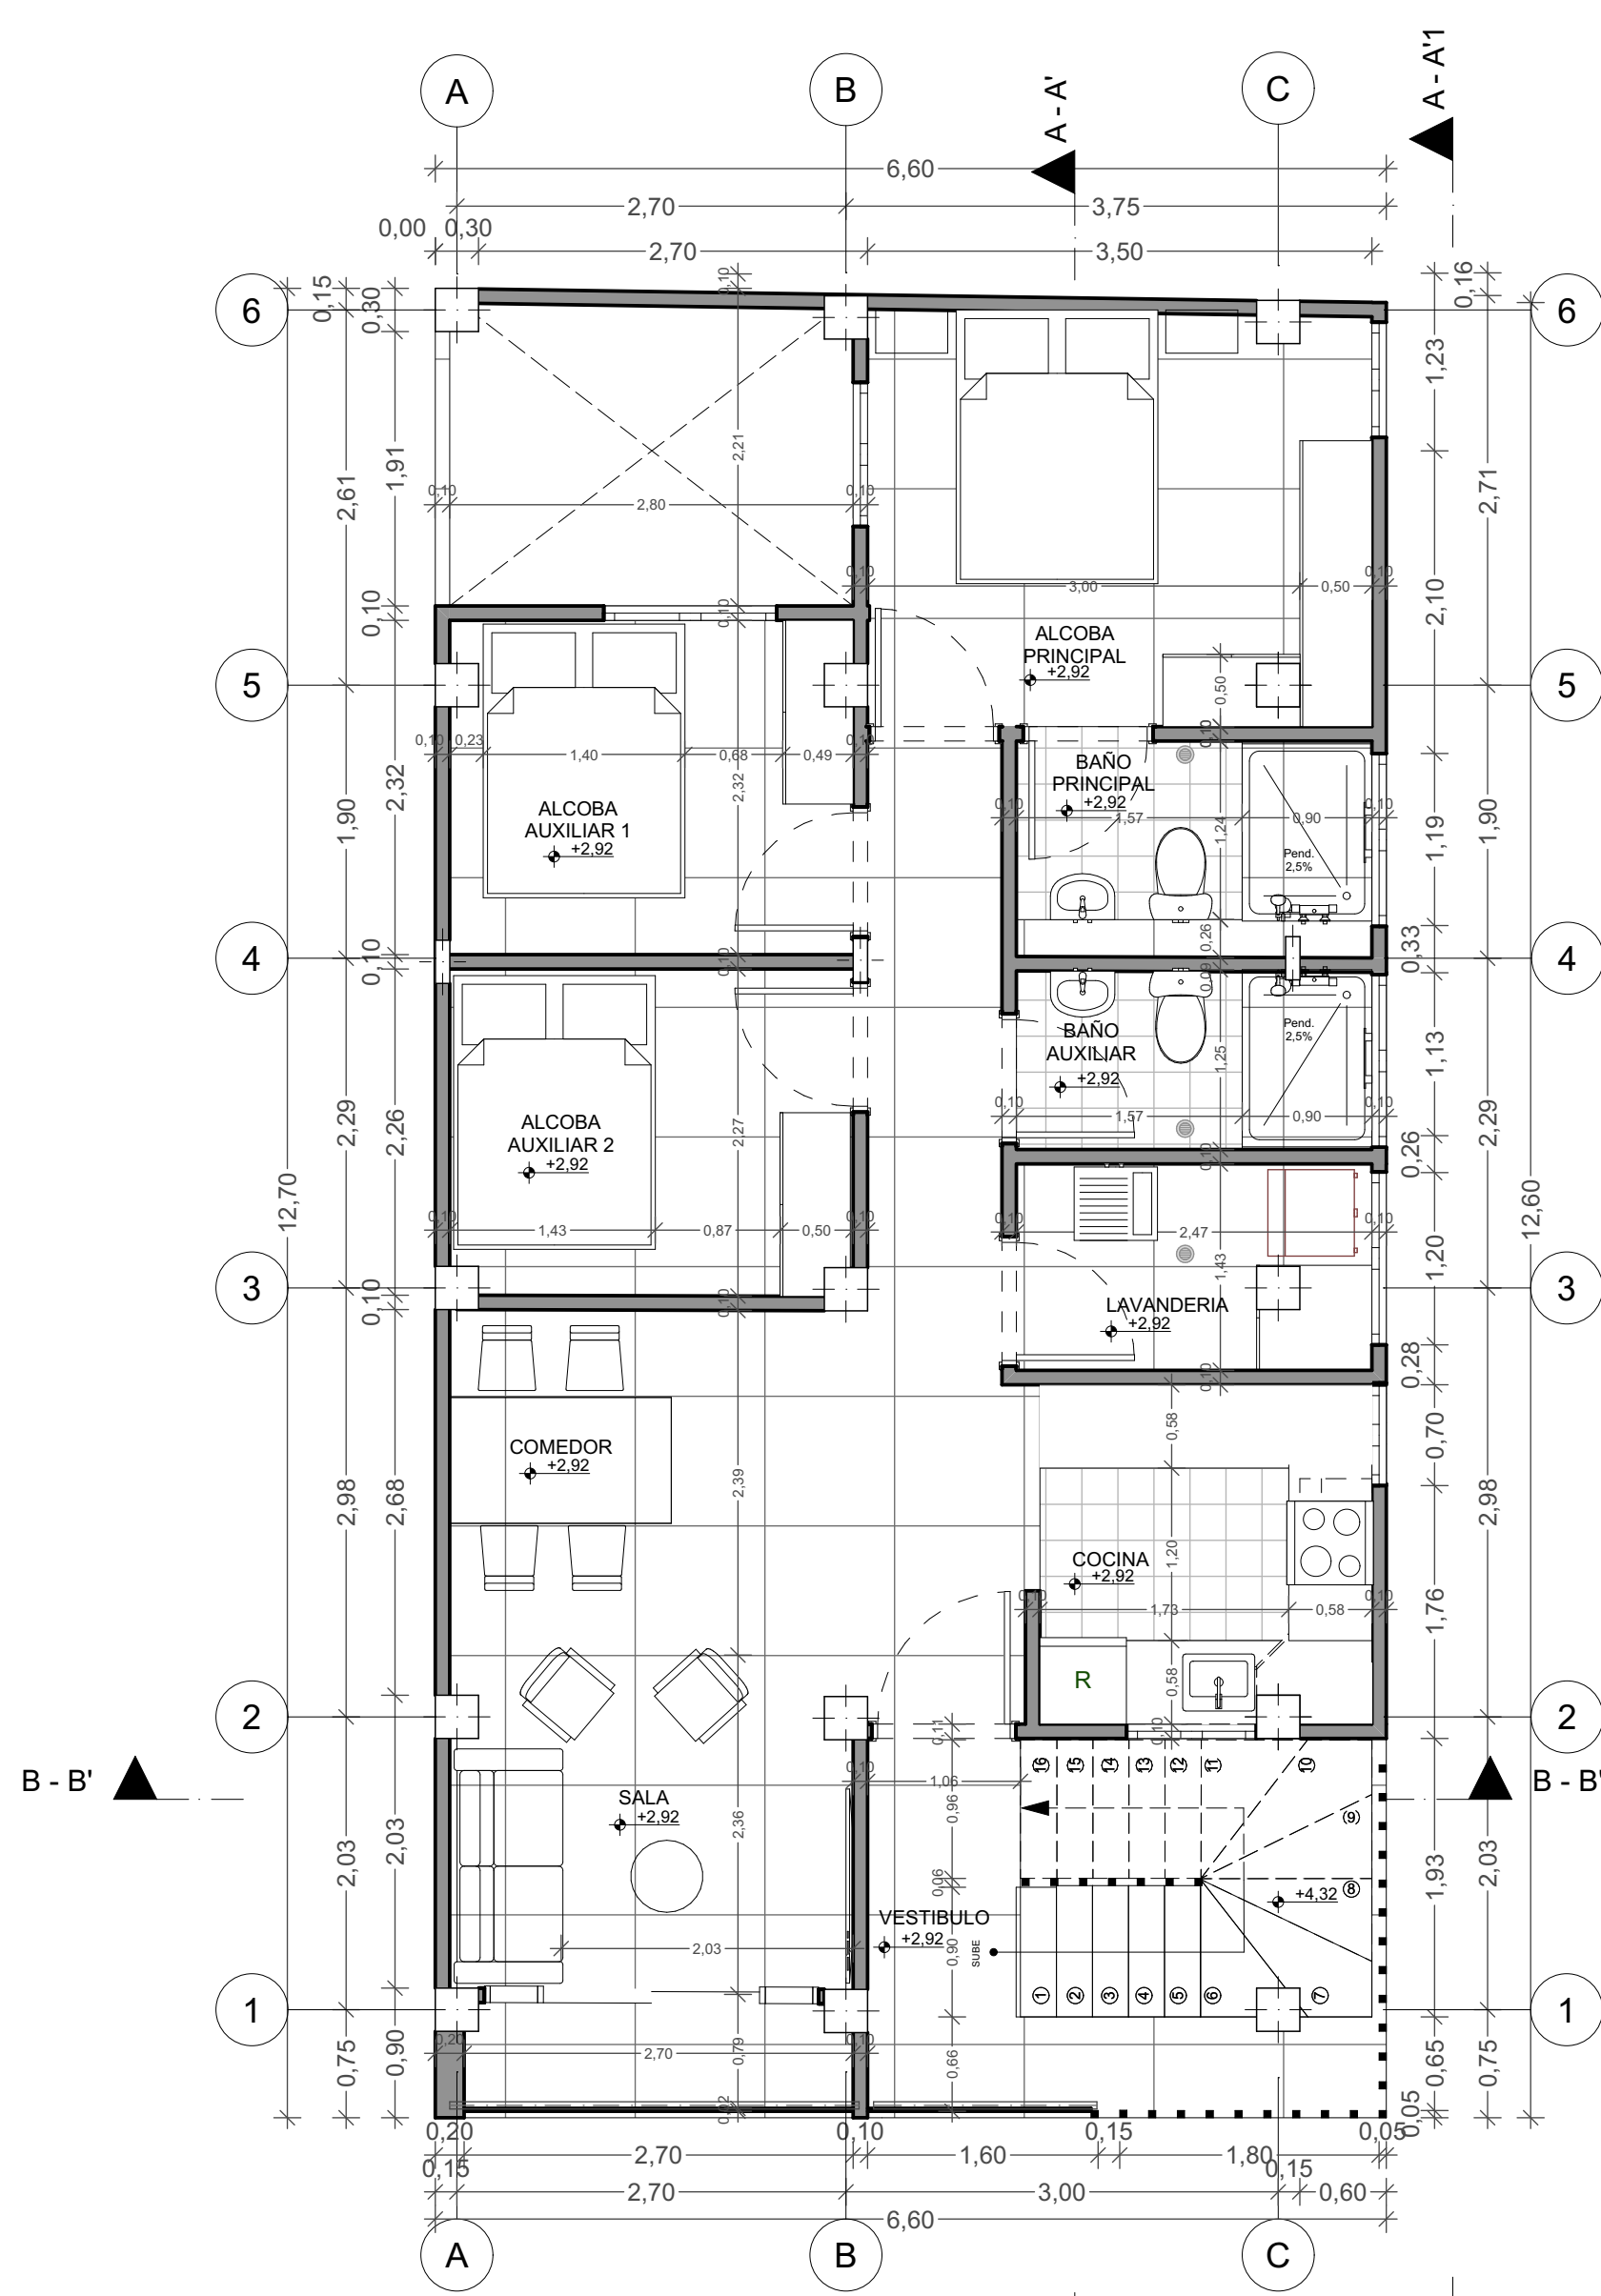

PLANTA TERCER PISO

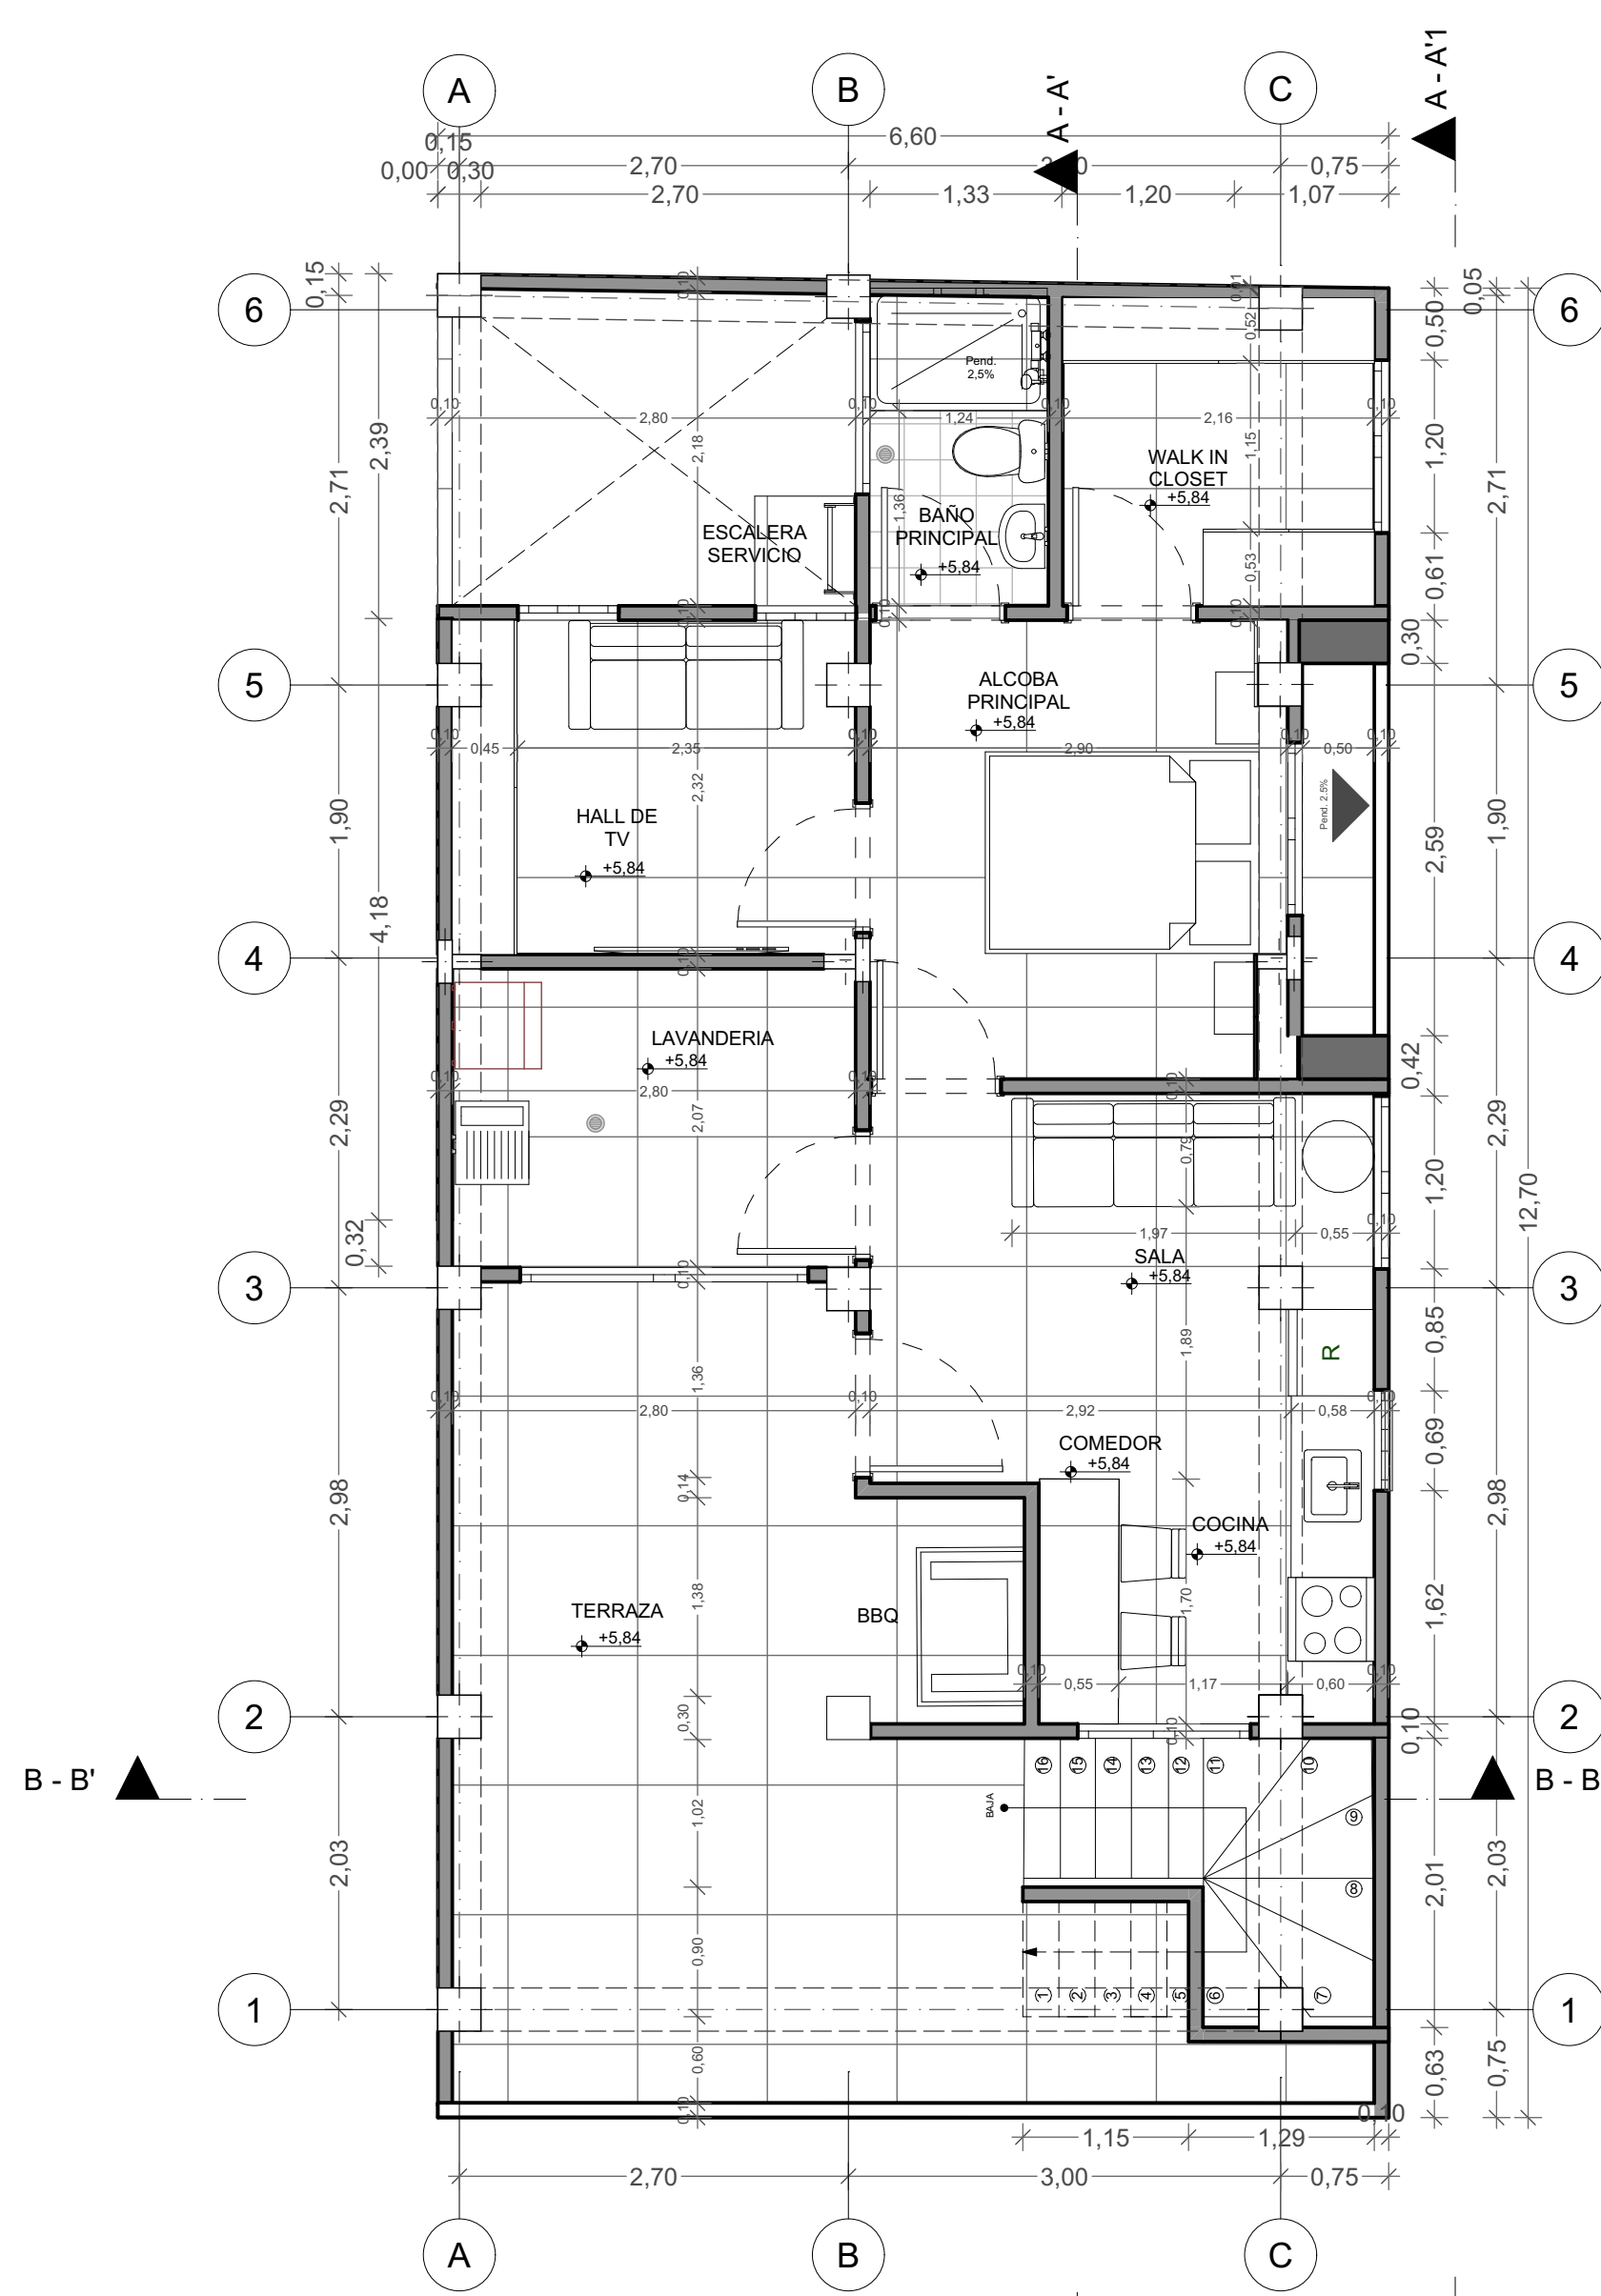


PLANTA DE CUBIERTA

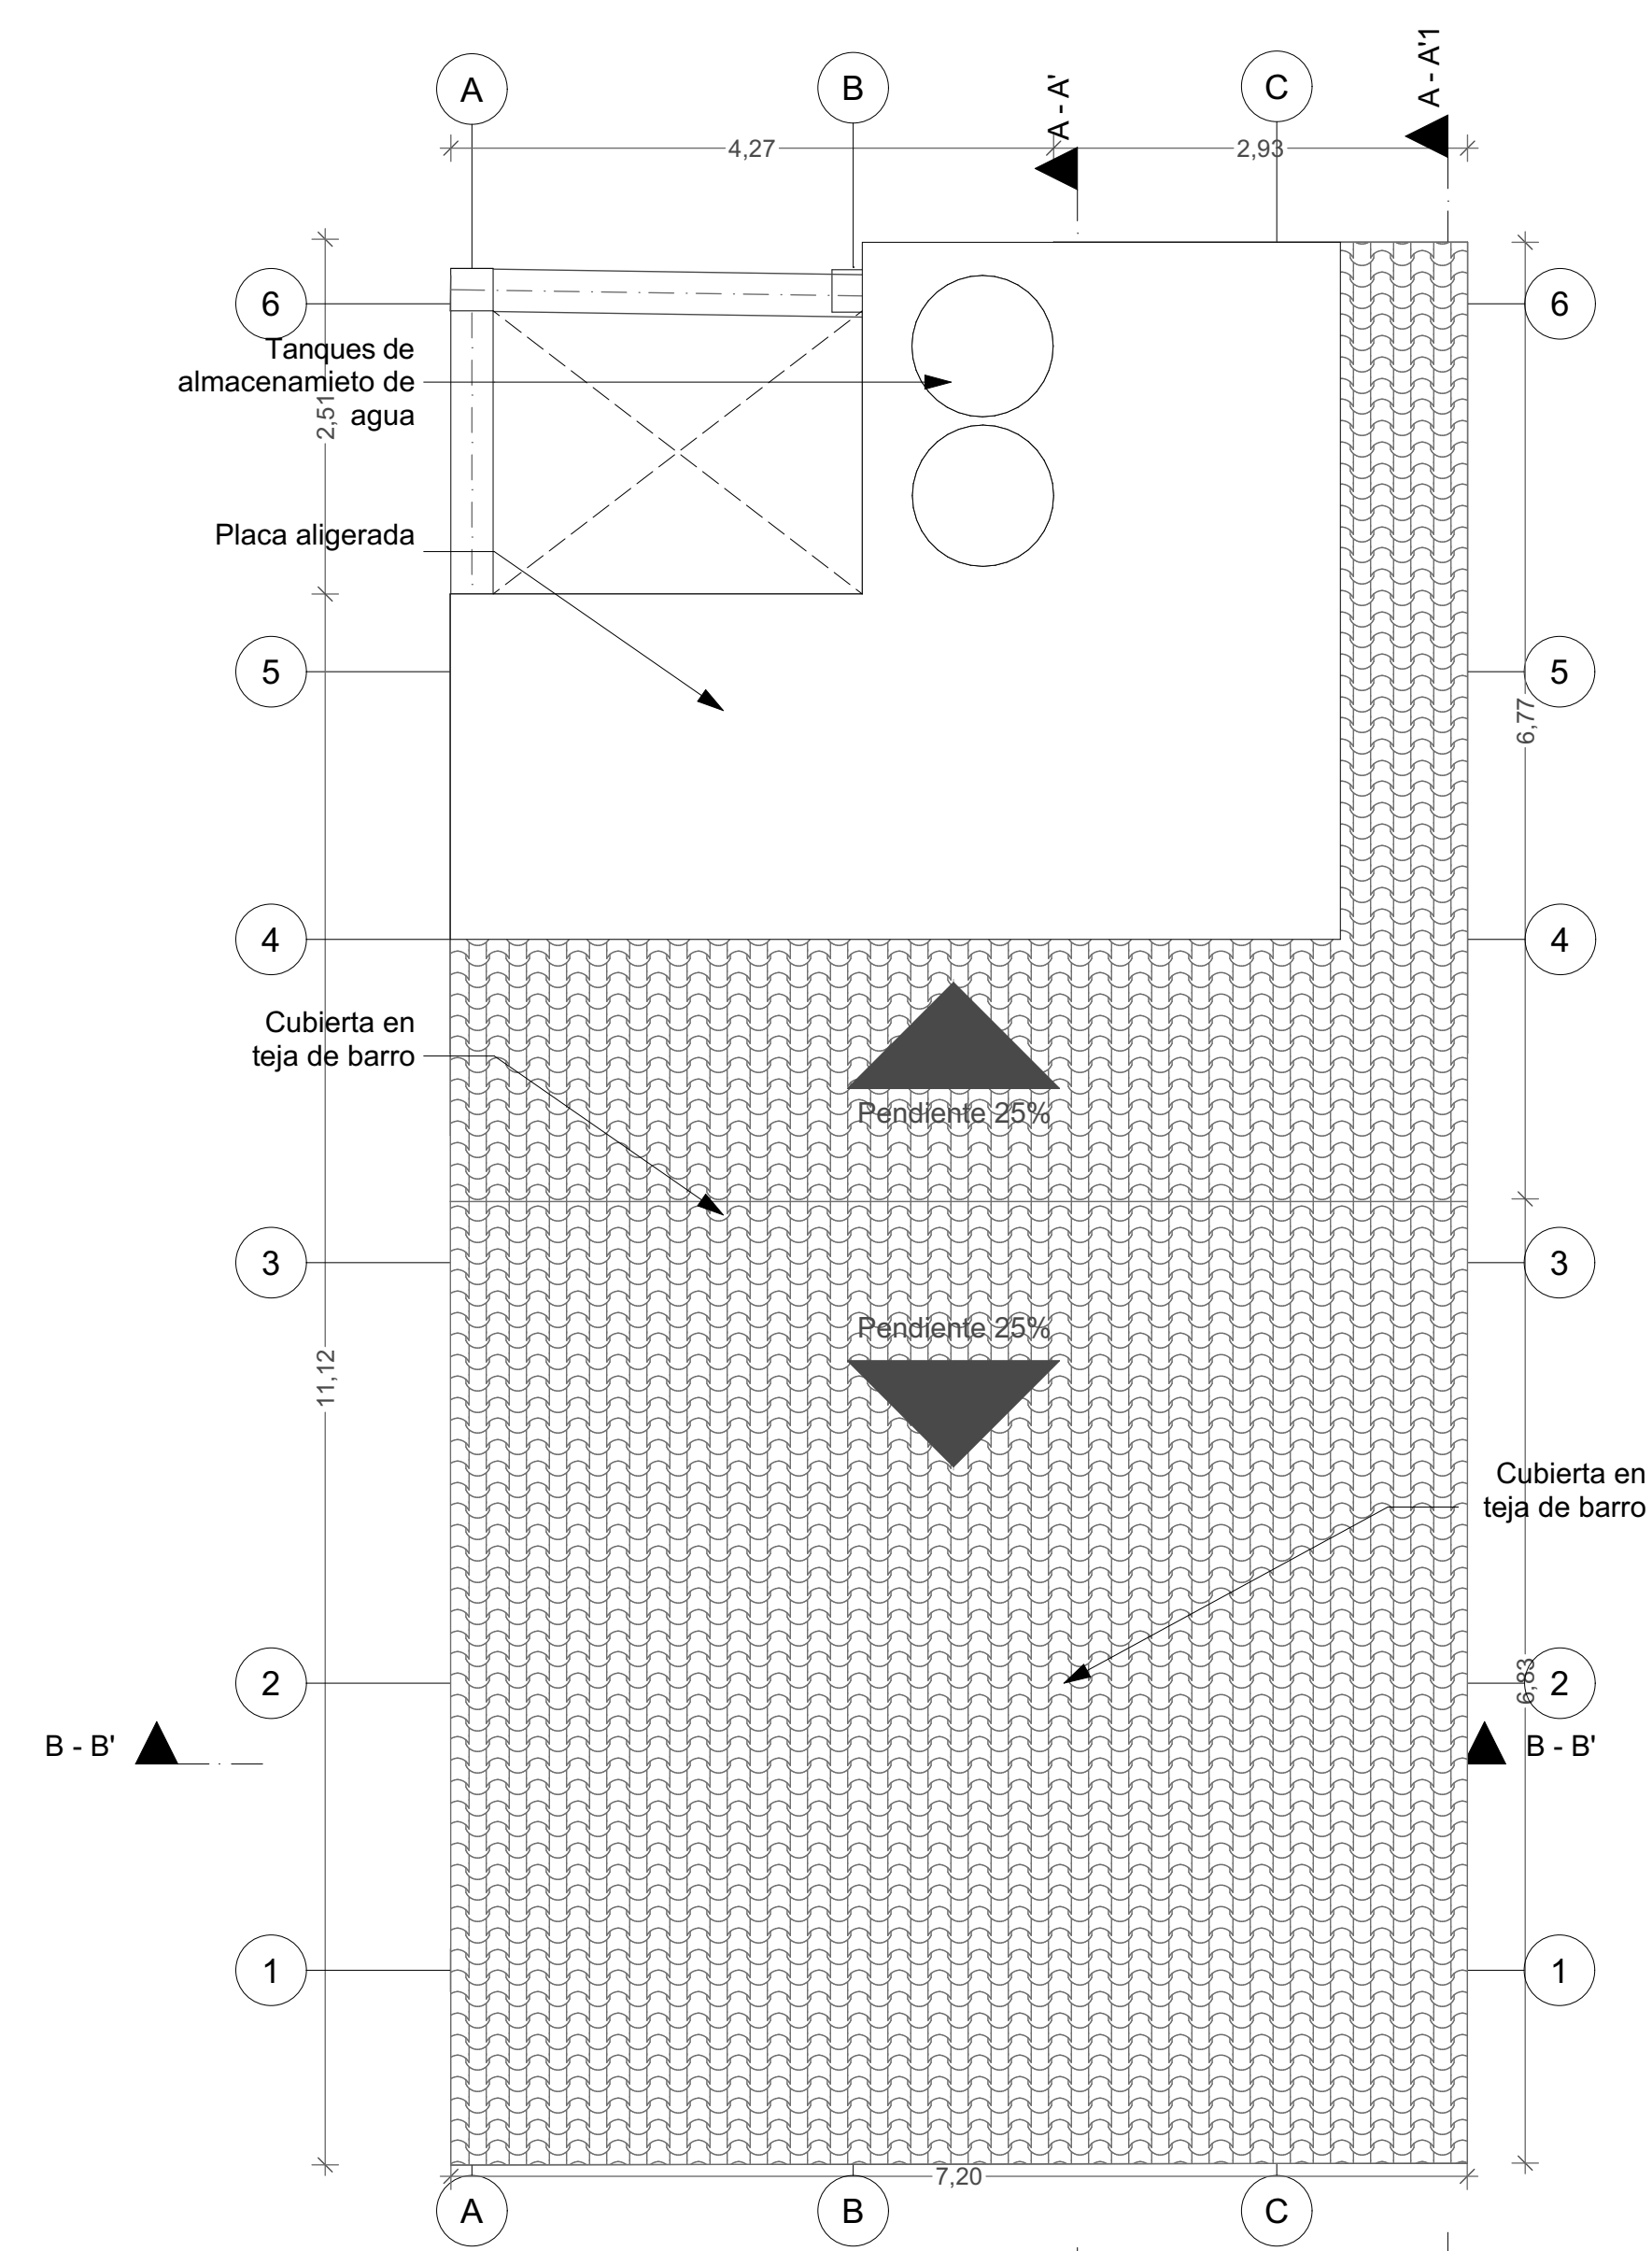


FACHADA LATERAL




FACHADA FRONTAL

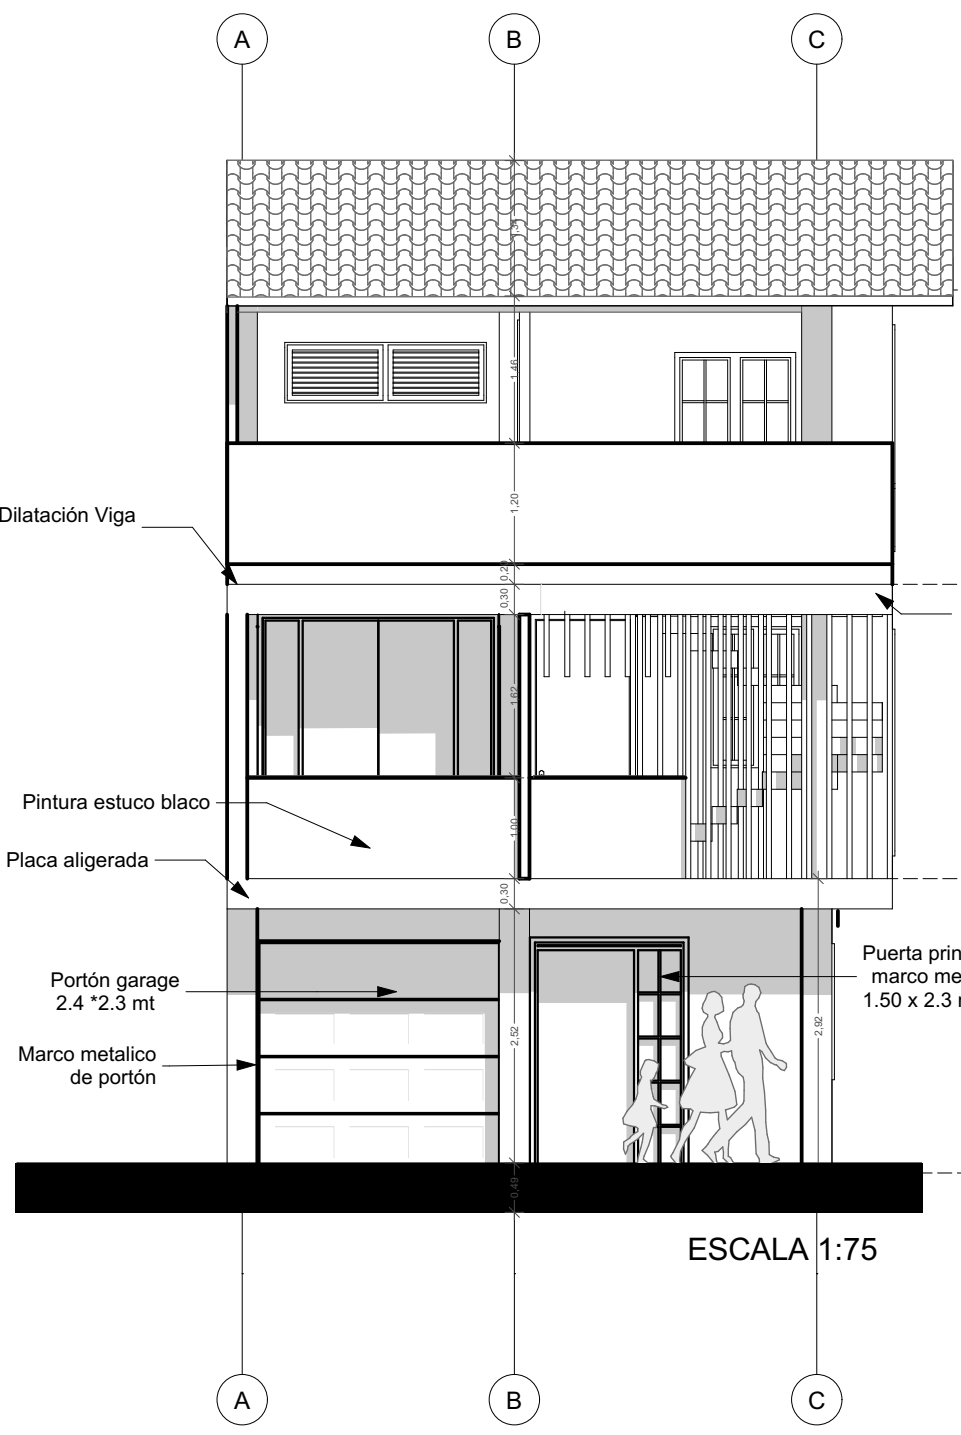

CORTE LONGITUDINAL

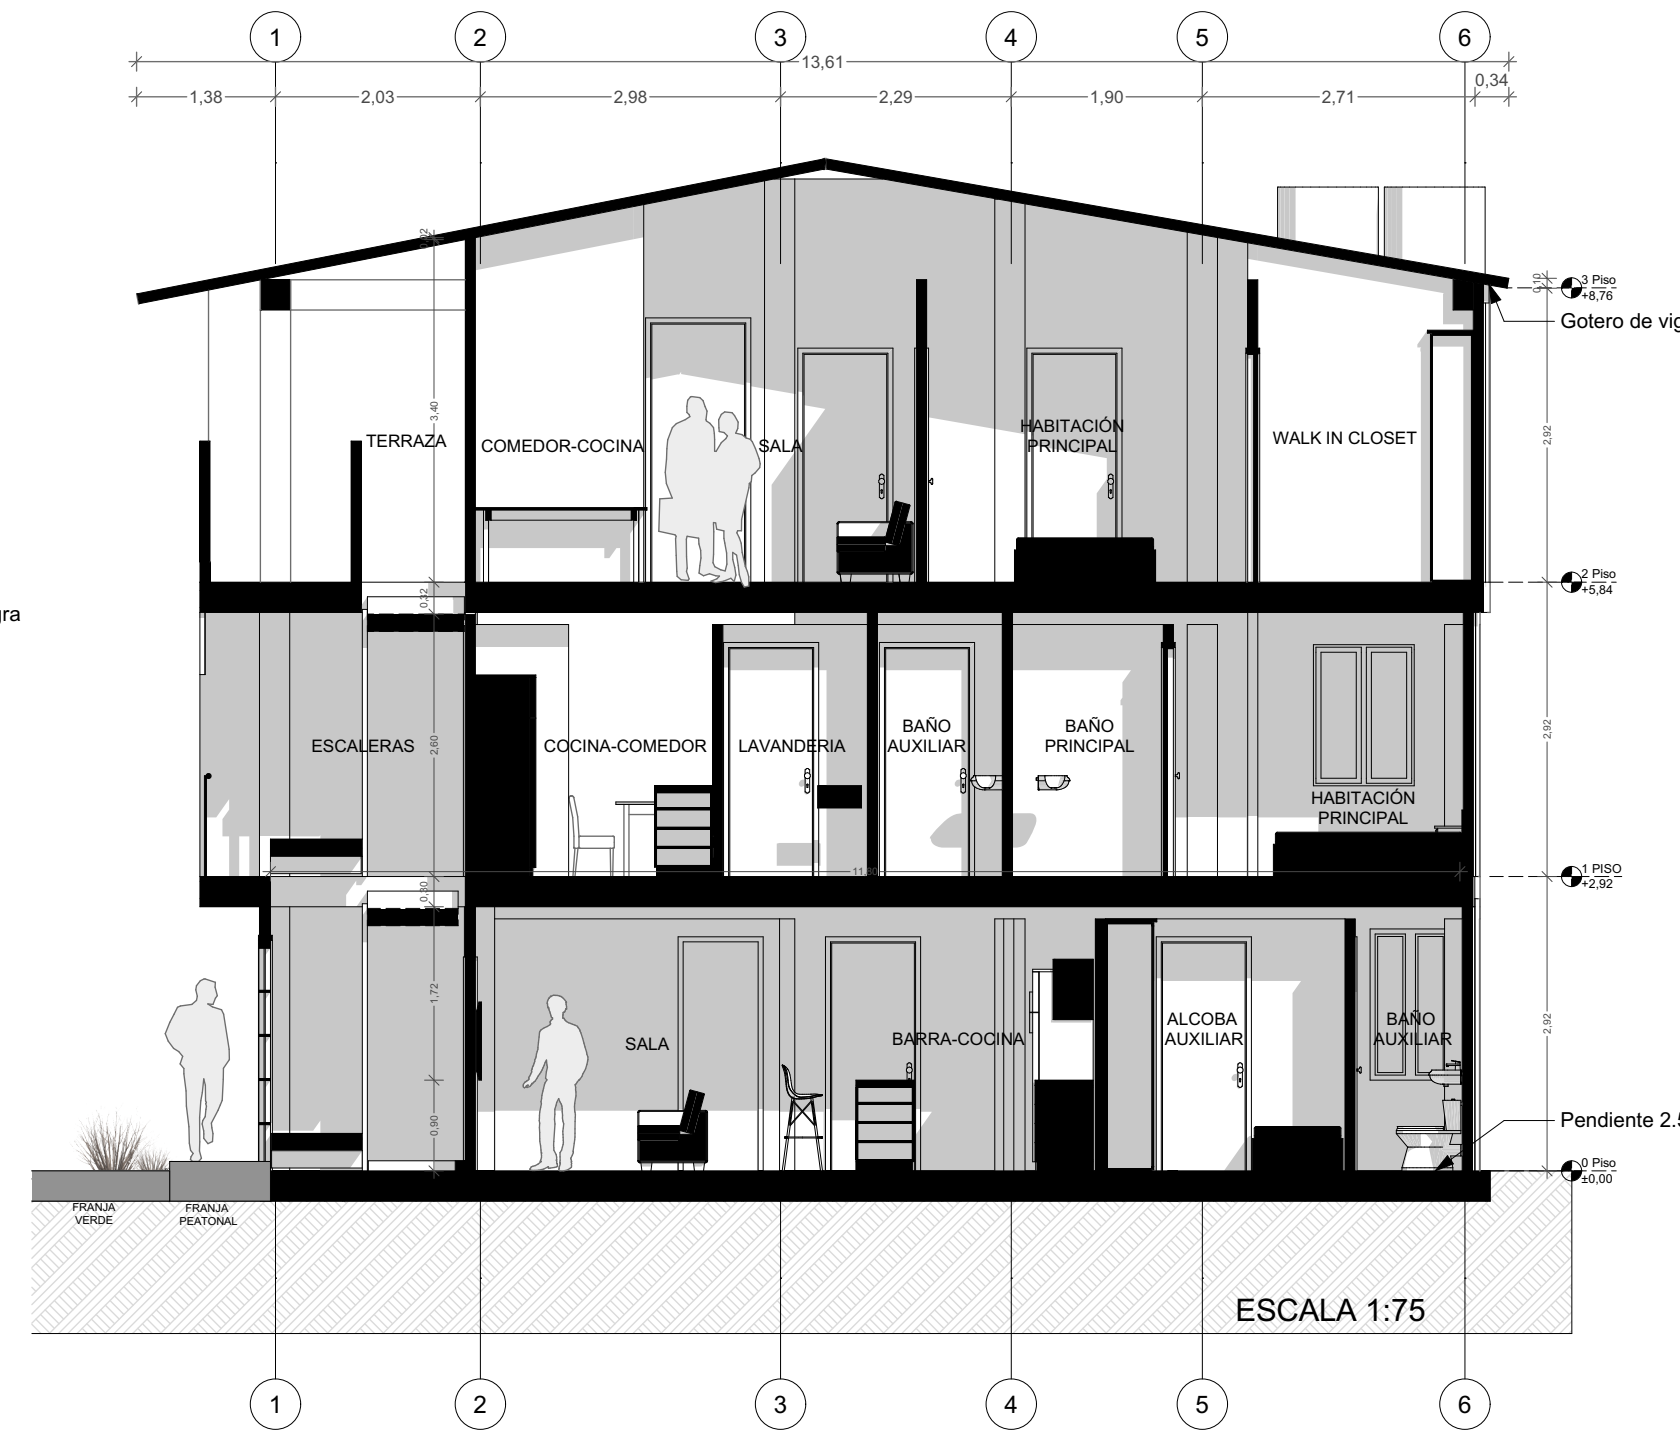

CORTE TRANSVERSAL

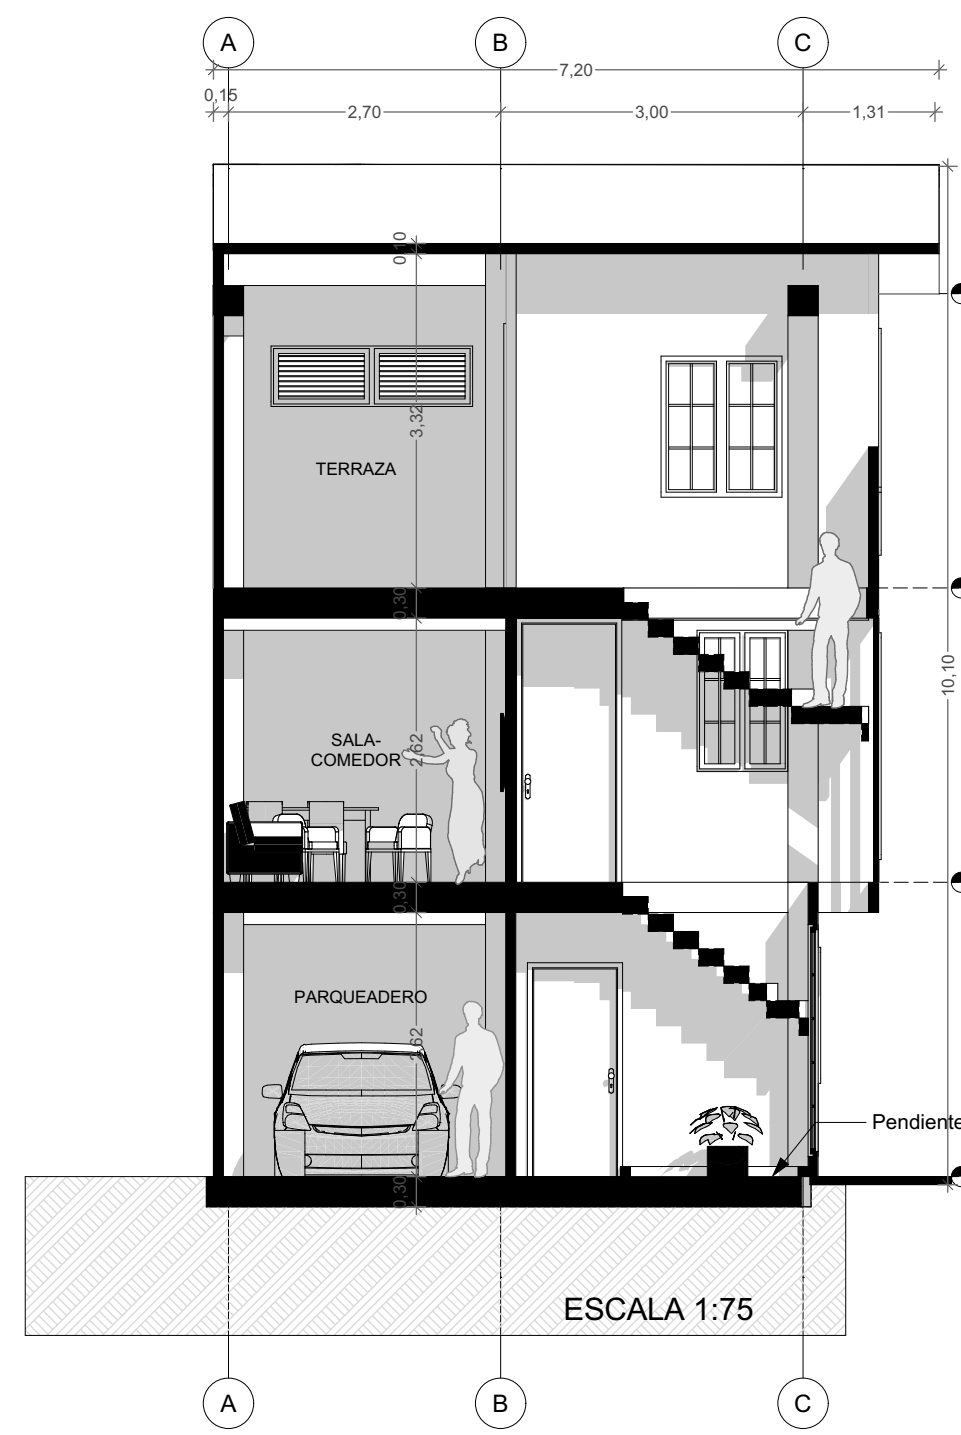

LOCALIZACIÓN



CUADRO DE ÁREAS

ÁREA TOTAL DEL LOTE	72.20 M2
ÁREA PRIVADA CONSTRUIDA 1 PISO	57.5 M2
ÁREA PRIVADA CONSTRUIDA 2 PISO	67.5 M2
ÁREA PRIVADA CONSTRUIDA 3 PISO	43.3 M2
ÁREA PRIVADA TOTAL CONSTRUIDA	168.3 M2
ÁREAS COMUNES	47.7 M2
ÁREA LIBRE	8.6 M2

PROPIETARIOS:

MARIA EUGENIA DURAN BARON

DIRECCIÓN:

LOTE I MANZANA A URBANIZACIÓN VIL
LA REAL
CARRERA 1A No 14 -18
SOCORRO, SANTANDER

DISEÑO:

ÁRQ. JESSICA VIVIANA RANGEL ESPINOSA
M. A30632018-I09873588



JESSICA VIVIANA RANGEL E.
CONSTRUCCIÓN - ARQUITECTURA - DISEÑO

CONTIENE:

PLANTAS ARQUITECTÓNICAS, CORTES,
FACHADA, CUADRO DE ÁREAS Y
LOCALIZACIÓN

TRAMITE:

LICENCIA DE CONSTRUCCIÓN NUEVA

FECHA

JUNIO 2025

ESCALA

1:50

PLANO

I DE I

APROBÓ: